


LEVANTAMIENTO PLANIMÉTRICO ALVAREZ CEDEÑO JUSTO XAVIER - LOTE 2

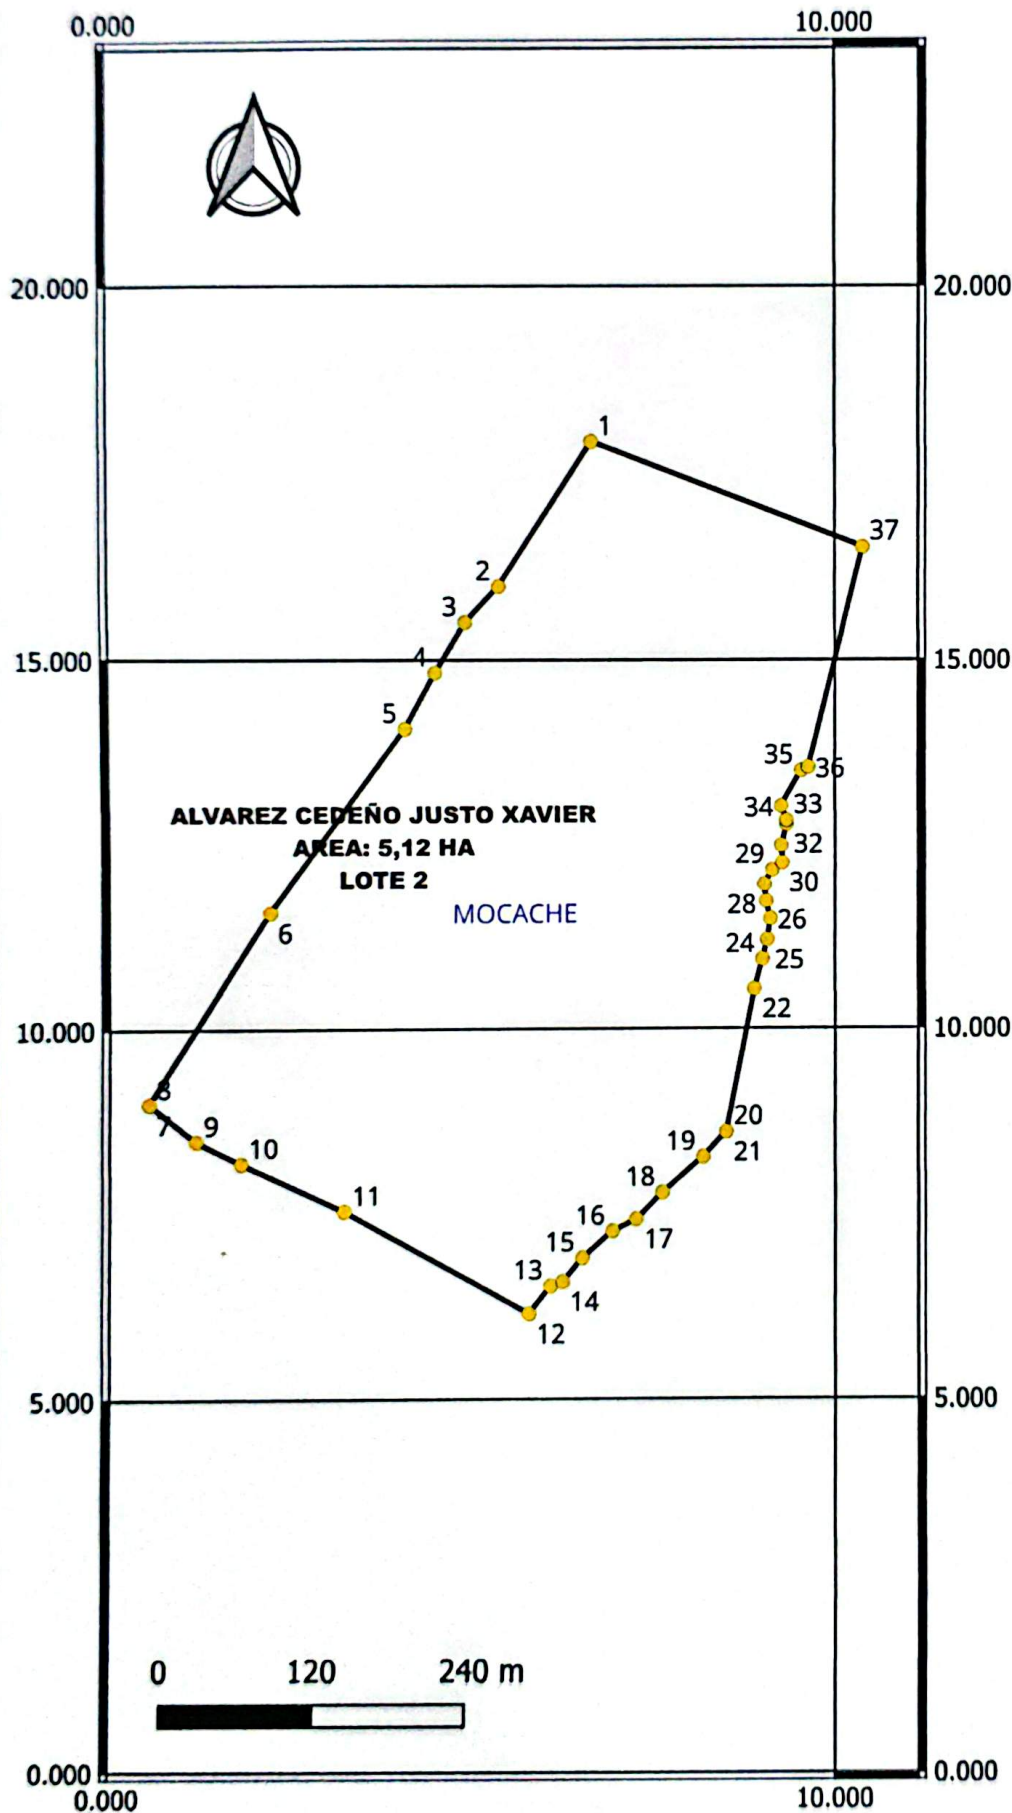


COORDENADAS GEOGRÁFICAS

PUNTO	X	Y
1	-79,4871042	-1,2995251
2	-79,4874365	-1,3000235
3	-79,4875548	-1,3001479
4	-79,4876625	-1,300323
5	-79,4877704	-1,3005179
6	-79,4882472	-1,3011575
7	-79,4886743	-1,3018235
8	-79,4886743	-1,3018235
9	-79,4885084	-1,3019522
10	-79,4883501	-1,3020303
11	-79,4879857	-1,3021972
12	-79,4873309	-1,3025539
13	-79,487255	-1,302458
14	-79,487211	-1,302443
15	-79,487142	-1,302361
16	-79,487035	-1,302268
17	-79,486951	-1,302227
18	-79,4868581	-1,3021342
19	-79,486713	-1,302011
20	-79,486631	-1,301924
21	-79,486631	-1,301924
22	-79,486531	-1,301426
23	-79,486531	-1,301426
24	-79,486502	-1,301322
25	-79,486485	-1,301255
26	-79,486475	-1,301181
27	-79,48649	-1,30112
28	-79,486496	-1,301062
29	-79,486468	-1,301012
30	-79,486432	-1,300987
31	-79,486435	-1,300926
32	-79,486417	-1,300852
33	-79,486417	-1,300838
34	-79,486436	-1,300788
35	-79,486364	-1,300664
36	-79,486338	-1,300652
37	-79,4861446	-1,2998878

AREA DEL PREDIO: 5,12 Ha
ESCALA: 1: 2800
Coordenadas Geograficas
[Longitud (X) Latitud (Y)]
Datum: WGS 84
Zona 17S

AVIER - LOTE 2

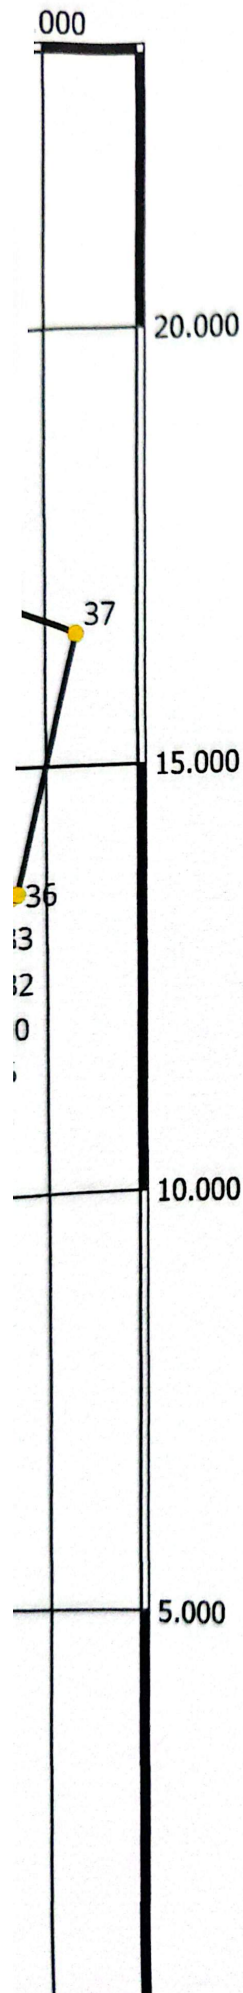

COORDENADAS GEOGRÁFICAS		
PUNTO	X	Y
1	-79,4871042	-1,2995251
2	-79,4874365	-1,3000235
3	-79,4875548	-1,3001479
4	-79,4876625	-1,300323
5	-79,4877704	-1,3005179
6	-79,4882472	-1,3011575
7	-79,4886743	-1,3018235
8	-79,4886743	-1,3018235
9	-79,4885084	-1,3019522
10	-79,4883501	-1,3020303
11	-79,4879857	-1,3021972
12	-79,4873309	-1,3025539
13	-79,487255	-1,302458
14	-79,487211	-1,302443
15	-79,487142	-1,302361
16	-79,487035	-1,302268
17	-79,486951	-1,302227
18	-79,4868581	-1,3021342
19	-79,486713	-1,302011
20	-79,486631	-1,301924
21	-79,486631	-1,301924
22	-79,486531	-1,301426
23	-79,486531	-1,301426
24	-79,486502	-1,301322
25	-79,486485	-1,301255
26	-79,486475	-1,301181
27	-79,48649	-1,30112
28	-79,486496	-1,301062
29	-79,486468	-1,301012
30	-79,486432	-1,300987
31	-79,486435	-1,300926
32	-79,486417	-1,300852
33	-79,486417	-1,300838
34	-79,486436	-1,300788
35	-79,486364	-1,300664
36	-79,486338	-1,300652
37	-79,4861446	-1,2998878

AREA DEL PREDIO: 5,12 Ha
 ESCALA: 1: 2800
 Coordenadas Geograficas
 [Longitud (X) Latitud (Y)]
 Datum: WGS 84
 Zona 17S