



1695



GOBIERNO AUTÓNOMO DESCENTRALIZADO
MUNICIPAL DEL CANTÓN EL EMPALME
DIRECCIÓN DE PLANIFICACIÓN URBANA
ORDENAMIENTO TERRITORIAL Y LEGALIZACIÓN DE TIERRAS
SECCIÓN AVALUOS Y CATASTROS
CATASTRO ZONA RURAL

COD CAT 151995800
FECHA 21 Enero 2013
AREA TERRENO 6.2396 has
ELABORA



NOTARÍA PRIMERA DEL CANTON EL EMPALME

TESTIMONIO DE LA E S C R I T U R A



De: Protocolización

Otorgado por: SUBSECRETARÍA DE TIERRAS Y

REFORMA AGROPECUARIA

A favor de: Velez Zambrano Pedro Pablo

Notaría Pública Interina
Ab. Ma. Marlene Velez Macías



GOBIERNO AUTÓNOMO DESCENTRALIZADO
MUNICIPAL DEL CANTÓN EL EMPALME
DIRECCIÓN DE PLANIFICACIÓN URBANA
ORDENAMIENTO TERRITORIAL Y LEGALIZACIÓN DE TIERRAS

El Empalme 3/enero del 2013 Marlon G. Alvarado Solórzano
JEFE DE SECCION AVALUOS Y CATASTROS

AB. MARLENE VÉLEZ MACIAS

NOTARIA INTERINA

Av. Quevedo No. 141 y Auhing.

Telefax: 04-2961850

El Empalme - Guayas - Ecuador



PROTOCOLIZACION: ABOGADA MARLENE VELEZ MACIAS, NOTARIA INTERINA DEL CANTON EL EMPALME, PROVINCIA DEL GUAYAS, REPUBLICA DEL ECUADOR, PREVIA PETICION QUE ANTECEDE Y EN EJERCICIO DE LA FACULTAD QUE ME CONCEDE EL NUMERAL DOS DEL ARTICULO DIECIOCHO DE LA LEY NOTARIAL, DOY FE. QUE EN LA PRESENTE FECHA, PROTOCOLIZO, INCORPORANDO AL PROTOCOLO DE DILIGENCIAS PUBLICAS A MI CARGO, LA PROVIDENCIA DE ADJUDICACIÓN NÚMERO UNO DOS CERO SIETE G CERO UNO SEIS CERO DOS, SIN HIPOTECA, DICTADA POR LA SUBSECRETARIA DE TIERRAS Y REFORMA AGRARIA, MEDIANTE PROVIDENCIA DICTADA EN GUAYAQUIL, EL VEINTISIETE DE SEPTIEMBRE DEL AÑO DOS MIL DOCE, A LAS ONCE HORAS VEINTISIETE MINUTOS VEINTINUEVE SEGUNDOS, A FAVOR DEL SEÑOR PEDRO PABLO VELEZ ZAMBRANO, RESPECTO A UN LOTE DE TERRENO, CON SUPERFICIE DE SEIS HECTAREAS DOS MIL TRESCIENTOS NOVENTA Y SEIS AREAS, UBICADO EN EL SECTOR PAVONES, DE LA PARROQUIA GUAYAS, CANTON EL EMPALME, PROVINCIA DEL GUAYAS, EN SEIS FOJAS UTILES, EL EMPALME, ENERO DOS DEL AÑO DOS MIL TRECE. - -

CUANTIA.- INDETERMINADA. - - - -

Y.C.CH.


AB. MARLENE VELEZ MACIAS
NOTARIA INTERINA



GOBIERNO NACIONAL
DE LA REPUBLICA
DEL ECUADOR

REPÚBLICA DEL ECUADOR

MINISTERIO DE AGRICULTURA, GANADERÍA, ACUACULTURA Y PESCA



Ministerio de
Agricultura, Ganadería,
Acuacultura y Pesca



PROVIDENCIA DE ADJUDICACIÓN No. 1207G01602

PROVINCIA: GUAYAS

SECTOR: PAVONES

UBICADO EN S/N

DISTRITO: OCCIDENTAL

CANTÓN: EL EMPALME

LOTE No.: S/N

O NOMBRE: S/N

PROYECTO:

PARROQUIA: GUAYAS

SUPERFICIE: 6.2396 HAS

SUBSECRETARÍA DE TIERRAS Y REFORMA AGRARIA

1. Guayaquil, 27 de Septiembre del 2012 a las 11:27:29 VISTOS.- VELEZ ZAMBRANO PEDRO PABLO con cédula(s) de ciudadanía número(s) 1303749756 de nacionalidad(es) ECUATORIANA de estado(s) civil(es) SOLTERO conforme señala(n) el(los) interesado(s), quien(es) ha(n) presentado la Solicitud tramitada con el expediente N° 1207G01602, para obtener la adjudicación del lote de terreno cuyas características y ubicación se detallan a continuación:

PROVINCIA: GUAYAS

SECTOR: PAVONES

CANTÓN: EL EMPALME

LOTE No.: S/N

O NOMBRE: S/N

PARROQUIA: GUAYAS

SUPERFICIE: 6.2396 HAS

2. El predio es patrimonio del Ministerio de Agricultura, Ganadería, Acuacultura y Pesca - Subsecretaría de Tierras y Reforma Agraria según Decreto Ejecutivo No. 373 del 28 de mayo del 2010 ; L.D.A. Y LEY TIERRAS BALDIAS ART. 1, NUMERAL 1 Protocolizada el e inscrita en el Registro de Propiedad del Cantón el

3. El precio para la adjudicación de la tierra objeto de esta providencia, es: el siguiente:

	PRECIO UNITARIO		TOTAL
Tierra, por HAS.	\$ 21.60	X 6.2396 HAS	\$ 134.80
Linderación y/o verificación-			\$ 0.00
Intereses	0 %		\$ 0.00
-Mejoras			\$ 0.00
		PRECIO TOTAL	\$ 134.80

SON: CIENTO TREINTA Y CUATRO DOLARES CON OCHENTA CENTAVOS
El avalúo de la tierra y mejoras lo fijó: STRA OFICIO S/N DEL 31-05-2012

Ab. Mariene Vélez Macías
NOTARIA INTERINA

4. Para la cancelación de la cantidad señalada en el numeral 3, el (los) peticionario(s) acepta (n) la siguiente forma de pago:

DEPÓSITO POR TIERRA

Comprobante ingreso y/o Recibo Caja Gral.No(s).
#6791

FECHA(S)
18-Jun-2012

VALOR(ES)
\$ 134.80

DEPÓSITO POR LINDERACIÓN Y/O VERIFICACIÓN

\$ 0.00

DEPÓSITO POR MEJORAS

\$ 0.00

TOTAL PAGADO

\$ 134.80

Nº 0042332



5. Por haber cumplido los requerimientos legales ADJUDICASE a: VELEZ ZAMBRANO PEDRO PABLO el lote de terreno ya expresado, con la superficie que se deja establecida y con los linderos constantes en el Informe de linderación No. S/N de fecha MARZO 2012 y que a continuación se detalla:

NORTE: VERA CEDENO JEBIO EN 55.07 M. R N 60 38 32 E. EN 166.27 M. R N 79 01 36 E. CON ANCHO DEL CARRETERO PUBLICO EN 12.00 M. CON HURTADO COBEÑA MARLEI EMPERATRIZ EN 144.28 M. R N 76 00 36 E.

SUR: VERA CEBALLOS ARTURO EN 175.25 M. R S 80 48 23 O. CON ESCUELA ANTONIO JOSE DE SUCRE EN 83.05 M. R N 02 04 47 O. EN 106.17 M. R S 86 45 37 O. CON CARRETERO PUBLICO EN 27.16 M SIGUIENDO SU TRAZADO CON ANCHO DEL CAMINO PUBLICO EN 6.00 M. CON GOMEZ CECILIA MARIA EN 129.06 M. R S 88 43 28 O.

ESTE: CAMINO PUBLICO EN 273.35 M. SIGUIENDO SU TRAZADO.

OESTE: ESTERO S/N EN 115.50 M. SIGUIENDO SU CURSO.

SE ADJUNTA COPIA DEL PLANO, INFORME DE LINDERACIÓN Y PLAN DE MANEJO

6. La presente Adjudicación se revertirá por el Incumplimiento de las siguientes obligaciones: A) Que el adjudicatario impida el libre acceso o tránsito por las servidumbres que hubiere o que estableciere La Subsecretaría de Tierras y Reforma Agraria u otra autoridad competente. B) Que el adjudicatario no cumpla el plan de manejo sustentable del área aprobado por La Subsecretaría de Tierras y Reforma Agraria o el Ministerio del Ambiente (MAE), según el caso. C) Por dolo es decir por engaño, fraude o trampa que distorsione o provoque equivocación a los servidores públicos que deben informar o decidir sobre la Adjudicación. Se entenderá la misma causal cuando el dolo provenga de los servidores públicos que intervengan en el trámite. La apreciación del dolo será probada dentro del trámite de reversión a la Adjudicación, sin perjuicio de la acción, ante el Tribunal de lo Contencioso Administrativo.

7. Esta adjudicación no da derecho a Saneamiento por Evicción y se realiza en relación a la cabida; sin embargo de lo cual, si la superficie fuere mayor a la expresada en esta providencia, el exceso continuará perteneciendo al Estado, que dispondrá libremente aún cuando estuviere cultivado, pero si la superficie fuere inferior a la expresada, ello no da derecho al adjudicatario para formular ninguna reclamación, debiendo conformarse con la superficie que existiere.

**ESPACIO
EN BLANCO**

REPÚBLICA DEL ECUADOR

MINISTERIO DE AGRICULTURA, GANADERÍA, ACUACULTURA Y PESCA



GOBIERNO NACIONAL
DE LA REPÚBLICA
DEL ECUADOR



Ministerio de
Agricultura, Ganadería,
Acuacultura y Pesca



PROVIDENCIA DE ADJUDICACIÓN No.: 1207G01602

EXPEDIENTE No.: 1207G01602

PROVINCIA: GUAYAS

CANTÓN: EL EMPALME

SECTOR: PAVONES

LOTE No.: S/N

UBICADO EN S/N

O NOMBRE: S/N

DISTRITO: OCCIDENTAL

PROYECTO:

PARROQUIA: GUAYAS
SUBSECRETARÍA DE TIERRAS Y REFORMA AGRARIA
GUAYAS - ECUADOR

8. La Subsecretaría de Tierras y Reforma Agraria se reserva el derecho de verificar técnicamente la cabida y linderos del predio adjudicado.

9. Mientras el adjudicatario no cumpla el plan de manejo en el plazo establecido, no podrá enajenar el predio.

10. Cuando se ha producido transferencia de dominio a favor de terceros la adjudicación puede ser objeto de reversión por las mismas causas que habrían afectado al adjudicatario original. Los terceros adquirentes necesariamente se subrogarán en los derechos y obligaciones del adjudicatario.

11. El adjudicatario ó quien lo subrogue en el derecho de dominio no podrá alegar plazo total pendiente en caso de incumplimiento del plan de manejo aprobado para la adjudicación, que haya considerado plazos parciales.

12. En caso de revertirse esta adjudicación, el predio volverá al estado anterior libre de todo gravamen a menos que estuviere en poder de terceros a cualquier título, quienes deberán atenerse a la resolución dictada.

13. El adjudicatario deberá entregar a La Subsecretaría de Tierras y Reforma Agraria en un plazo máximo de 120 días después de la fecha de entrega de la Providencia de Adjudicación, una copia auténtica debidamente protocolizada e inscrita en el respectivo Registro de la Propiedad. De no hacerlo, se podrá dejar sin efecto o se resolverá la misma, según sea el caso.

La presente providencia, una vez anotada en el Registro Catastral General de tierras de La Subsecretaría de Tierras y Reforma Agraria, protocolícese en una Notaría Pública, e inscribáse en el Registro de la Propiedad Cantonal correspondiente, conjuntamente con el plano y el plan de manejo que forman parte de esta Adjudicación, a costa del adjudicatario.

NOTIFÍQUESE y CÚMPLASE...

Nº 0042332



VELEZ ZAMBRANO PEDRO PABLO

1207G01602



ABG. EDICSON AROCA LIMONES

DIRECTOR DISTRITAL OCCIDENTAL DE LA
SUBSECRETARIA DE TIERRAS Y REFORMA AGRARIA



CERTIFICO.-


NELSON LEONARDO FRANCO CHAVEZ

SECRETARIO AD-HOC DISTRITO OCCIDENTAL DE LA
SUBSECRETARIA DE TIERRAS Y REFORMA AGRARIA

La presente providencia queda anotada en esta fecha en el Registro Catastral General de Tierras de
La Subsecretaria de Tierras y Reforma Agraria en el Folio No. 121 Tomo No. 3570
Guayaquil, 30-10-2012

CERTIFICO.-


NELSON LEONARDO FRANCO CHAVEZ

SECRETARIO AD-HOC DISTRITO OCCIDENTAL DE LA
SUBSECRETARIA DE TIERRAS Y REFORMA AGRARIA



ELABORADO POR: ALFREDO CASTILLO

Alfredo Castillo

INFORME DE LINDERACION

Posesionario : VELEZ ZAMBRANO PEDRO PABLO

Provincia : Guayas
Cantón : El Empalme
Parroquia : Guayas
Sector : Pavones
Escala : 1:2500



LINDEROS

NORTE: Vera Cedeño Ulbio en 55.70 m R.N. 60°38'32" E. en 166.27 m R.N. 70°00'36" E. con ancho de carretero publico en 12.00 m con Hurtado Cobeña Marlei Emperatriz en 131.42 m R.N. 76°00'36" E.

SUR: Vera Cevallos Arturo en 175.25 m R.S. 80°48'23" O. con Escuela Antonio Jose De sucre en 83.05 m R.N. 02°04'12" O. en 106.17 m R.S. 86°45'37" O. con Carretero publico en 27.16 m siguiendo su trazado con ancho del camino publico en 6.00 m con Gomez Cecilia Maria en 129.06 m R.S. 88°13'26" O.

ESTE: Camino publico en 273.35 m siguiendo su trazado

OESTE: Estero S/n en 115.50 m siguiendo su curso

SUPERFICIE: 6,2396 Has.

CUADRO DE COORDENADAS


COORDENADAS		
Vértice	X (m)	Y (m)
1	648161,00	9896387,00
2	648324,23	9896418,85
3	648336,00	9896421,00
4	648476,00	9896455,88
5	648490,00	9896446,00
6	648459,00	9896408,00
7	648473,00	9896327,00
8	648488,00	9896285,00
9	648502,00	9896262,00
10	648518,00	9896211,00
11	648345,00	9896183,00
12	648342,00	9896266,00
13	648236,00	9896260,00

COORDENADAS		
Vértice	X (m)	Y (m)
14	648244,14	9896285,91
15	648239,00	9896289,00
16	648110,00	9896285,00
17	648083,00	9896312,00
18	648084,00	9896324,00
19	648101,00	9896325,00
20	648094,00	9896343,00
21	648105,00	9896344,00
22	648113,00	9896380,00

Datos tomados con GPS
Datum: PSAD56
Coordenadas UTM
Zona 17 Sur

Fecha: Marzo 2012
Levanto y Dibujo: Ing. Wilton Moran
Licencia Profesional: 751849
Firma: *[Signature]*


Revisó y Aprobó
Firma: *[Signature]*
30-05-2012

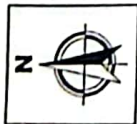

CUADRO DE AREAS

Area 1	1.8533 Has.
Area 2	4.3863 Has.
Area Correlativa	0.1551 Has.
Area Total	6.3947 Has.
Area Ajustada	6.2396 Has.

PLANO PREDIAL

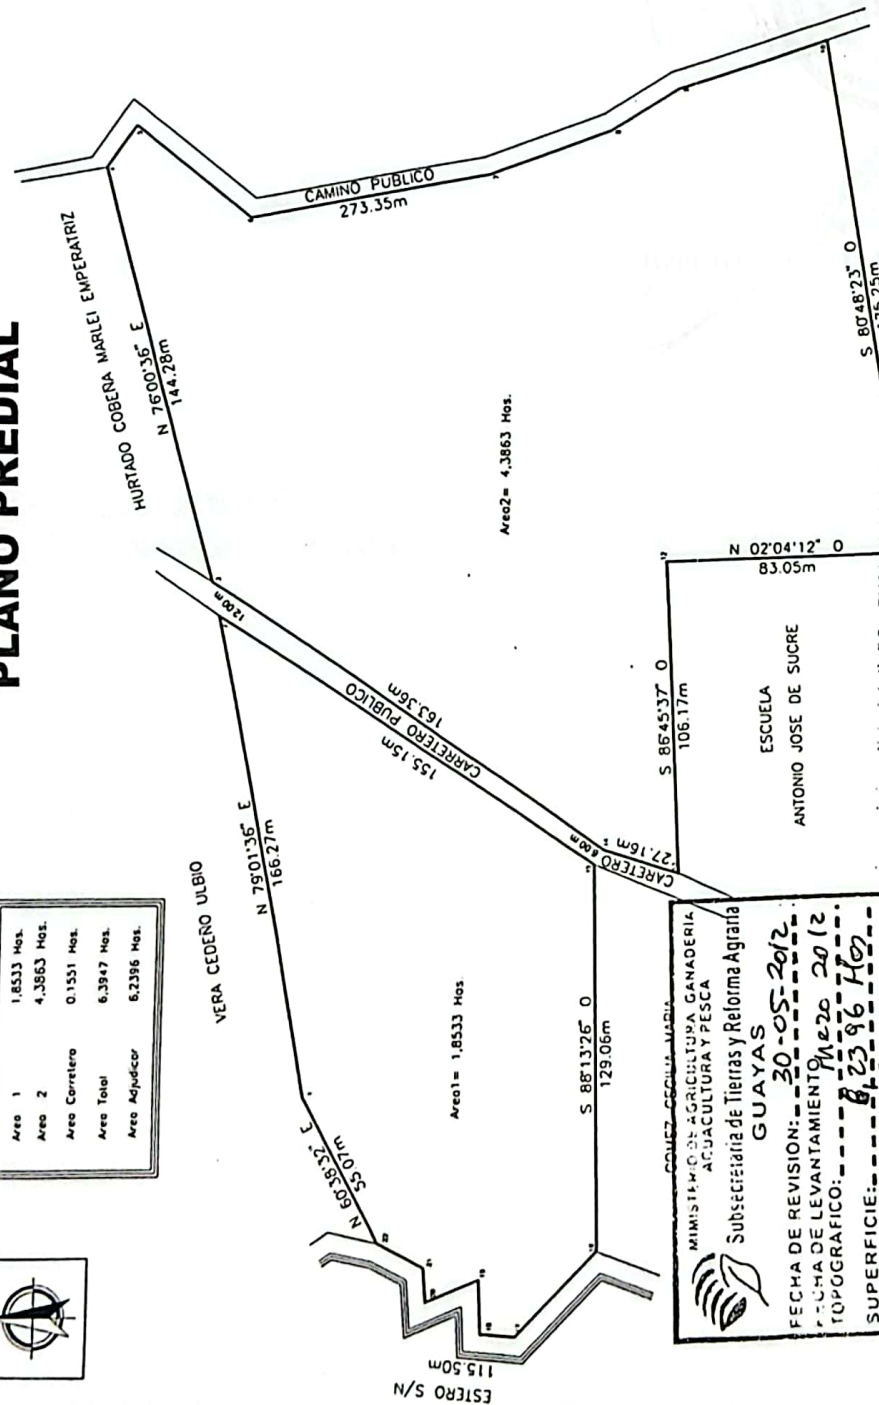

Area2= 4,3863 Has.

Area1= 1,8533 Has

MINISTERIO DE AGRICULTURA GANADERIA ACUICULTURA Y PESCA

Subsecretaría de Tierras y Reforma Agraria

GUAYAS

FECHA DE REVISION: 30-05-2012

FECHA DE LEVANTAMIENTO: 19-02-2012

TOPOGRAFICO: 6-23-96 H07


SUPERFICIE: 6,2396 Has.

FECHA DE APROBACION: 30-05-2012

APROBADO: 14-140-6012362-

621-46(C)POR: 14-140-6012362-

UBICACION

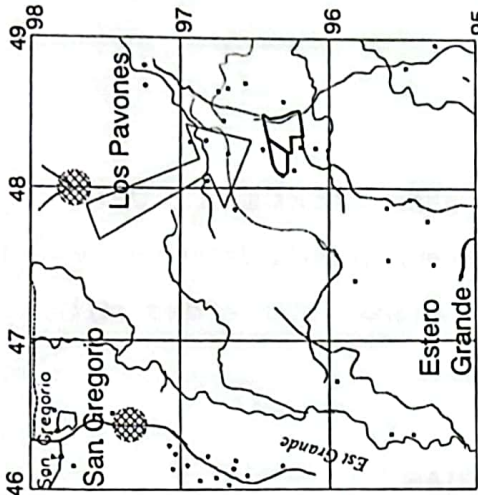

ESCALA 1:50,000
CARTA TOPOGRAFICA GUAYAS
CODIGO NIIE-4

V	COORDENADAS	
	Y	X
1	9,896,387.00	648,161.00
2	9,896,418.65	648,324.23
3	9,896,421.00	648,336.00
4	9,896,435.88	648,476.00
5	9,896,446.00	648,490.00
6	9,896,408.00	648,459.00
7	9,896,327.00	648,473.00
8	9,896,285.00	648,488.00
9	9,896,262.00	648,502.00
10	9,896,211.00	648,518.00

Datos tomados con GPS
Datum: PABLO
Elevación: 177m
Zona 17 Sur

NOMBRE:

VELEZ ZAMBRANO PEDRO PABLO

Provincia:

GUAYAS

Cantón:

EL EMPALME

Parroquia:

GUAYAS

Sector:

PAVONES

Fecha:

MARZO/2012

Escala:

1:2500

Superficie:

6,2396 Has.

Posesionario:

VELEZ ZAMBRANO PEDRO PABLO

Levantó y Dibujo:

ING. AGRI. WILTON MORA M.

Revisó y Aprobó:

ING. AGRI. WILTON MORA M.





ESCALA 1:50.000
CARTA TOPOGRAFICA GUAYAS
CODIGO NIII-E4

V	C O O R D E N A D A S	
	Y	X
1	9,896,387.00	648,161.00
2	9,896,418.65	648,324.23
3	9,896,421.00	648,336.00
4	9,896,455.88	648,476.00
5	9,896,446.00	648,490.00
6	9,896,408.00	648,459.00
7	9,896,327.00	648,473.00
8	9,896,285.00	648,488.00
9	9,896,262.00	648,502.00
10	9,896,211.00	648,518.00
Datos tomados con GPS		
Datum: PSAD56		
Coordenadas UTM		

Datos tomados con GPS
 Datum: PSAD56
 Coordenadas UTM
 Zona 17 Sur

VONES

Revisó y Aprobó:

[Handwritten signatures]

