


LEVANTAMIENTO PLANIMÉTRICO ALVAREZ VELIZ CARLOS FREDDY

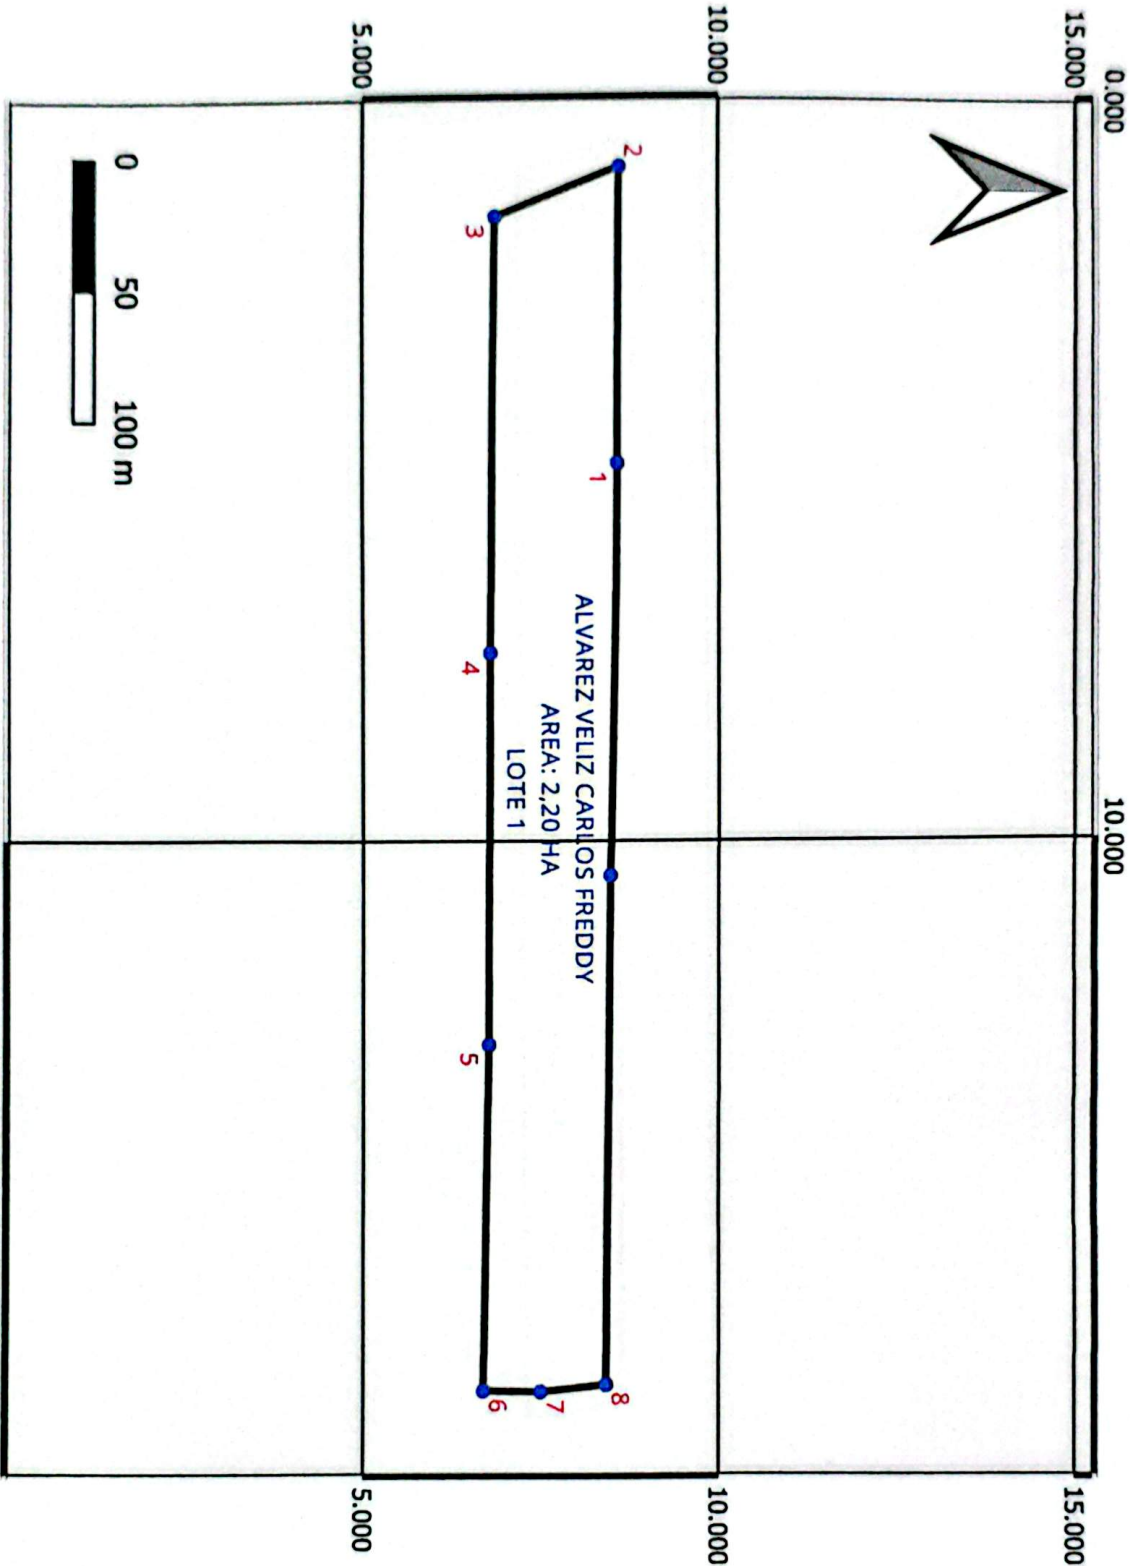

COORDENADAS GEOGRÁFICAS		
PUNTO	X	Y
1	-79,477074	-1,302564
2	-79,478083	-1,302555
3	-79,477914	-1,302996
4	-79,47643	-1,303018
5	-79,47509	-1,303025
6	-79,473898	-1,303044
7	-79,473894	-1,30284

●

ALVAREZ VELIZ CARLOS FREDDY


□

ALVAREZ VELIZ CARLOS FREDDY

OSM Standard

PROPIETARIO:
 ALVAREZ VELIZ CARLOS FREDDY
AREA DEL PREDIO:
 2,20 HECTAREAS
CANTÓN: MOCACHE
PROVINCIA: LOS RIOS
ESCALA: 1: 2750
 Coordenadas Geográficas
 [Longitud (X) Latitud (Y)]
 Datum: WGS 84
 Zona 17S

LEVANTAMIENTO PALNIMETRICO CACAO
ALVAREZ VELIZ CARLOS FREDDY - LOTE 2

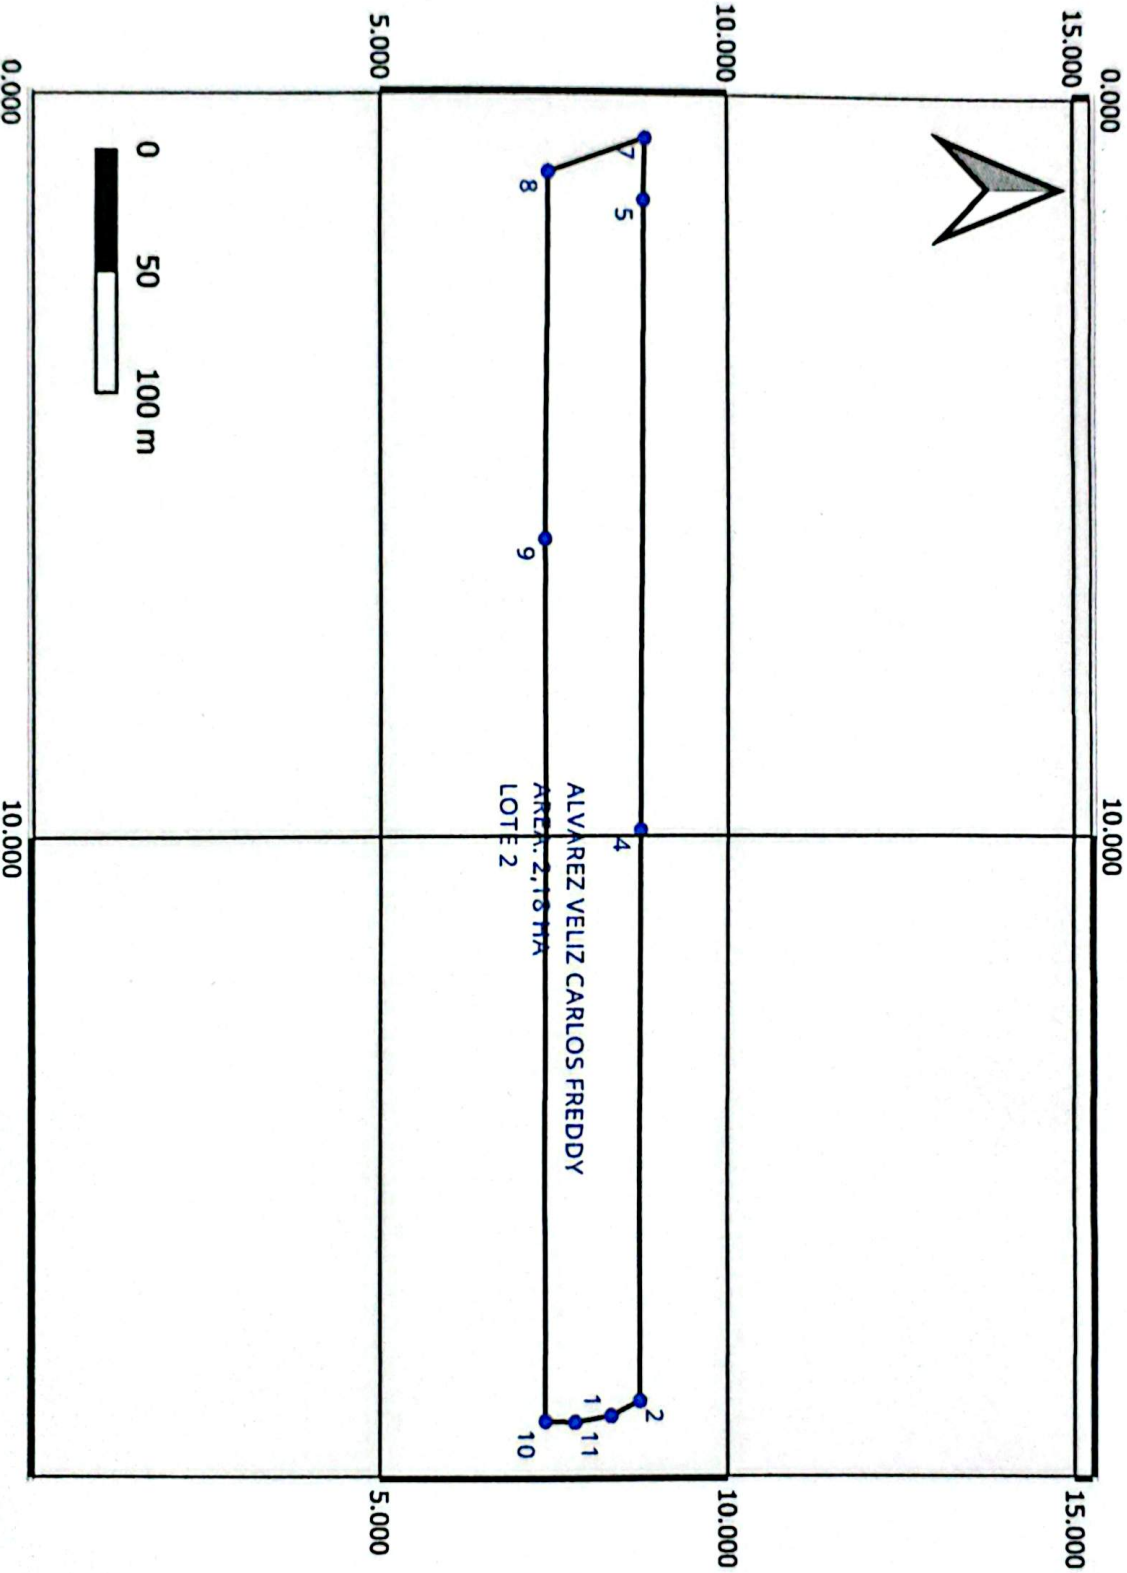

COORDENADAS GEOGRÁFICAS		
PUNTO	X	Y
1	-79,473518	-1,30416
2	-79,473573	-1,304046
3	-79,473572	-1,304046
4	-79,475688	-1,304046
5	-79,478026	-1,304032
6	-79,478256	-1,304025
7	-79,478256	-1,304025
8	-79,478129	-1,304409

LEYENDA

● ALVAREZ VELIZ CARLOS FREDDY - LOTE 2

□ ALVAREZ VELIZ CARLOS FREDDY - LOTE 2

OSM Standard

PROPIETARIO:
 ALVAREZ VELIZ CARLOS FREDDY

AREA DEL PREDIO:
 2.18 HECTAREAS

CANTON: MOCACHE

PROVINCIA: LOS RIOS

ESCALA: 1: 3000

Coordenadas Geográficas
 [Longitud (X) Latitud (Y)]

Daturn: WGS 84

Zona 17S