

224/15

REPÚBLICA DEL ECUADOR



MUNICIPALIDAD DEL EMPALME
DIRECCIÓN FINANCIERA
SECCIÓN VALORES Y CATASTROS
CATASTROS ZONA RURAL
REGISTRO 50209400
FECHA 4. ENO. 2012
ÁREA TERRENO 1,5427 Has
ELABORO



NOTARIA PÚBLICA DEL CANTON EL EMPALME



"Primera y Segunda"

TESTIMONIO DE LA ESCRITURA

Venta de derechos y acciones hereditarias que
hace la Señora Eusebia Domitila García Briones
y hermanos a favor del Señor Noé Aladino
Castro Cuervo y Señora.

Ab. Ma. Marlene Vélez Macías
NOTARIA INTERINA

El Empalme, 20 de Diciembre del 2011

Ab. Marlene Vélez Macías

NOTARIA INTERINA

Anda, Quevedo No. 141 Auhing.

Telefax: 04-2961850

El Empalme - Guayas - Ecuador




ESCRITURA #



VENTA DE DERECHOS Y ACCIONES HEREDITARIAS QUE HACEN LOS SEÑORES EUSEBIA DOMITILA, EULALIA AUXILIADORA, ROSA FILADELFIA, LAUREANO CLAUDIO, SOLANDA MARGARITA Y RAMÓN EDUARDO GARCIA BRIONES, A FAVOR DE LOS CÓNYUGES SEÑOR NOE ALADINO CASTRO CARREÑO Y DOÑA LUCIA VICTORIA GARCIA BRIONES.-

CUANTÍA:- S. 2.228.09.-

En el cantón El Empalme, provincia de Guayas, República del Ecuador, a los OCHO días del mes de DICIEMBRE del año DOS MIL ONCE, ante mí, **Abogada MARLENE VELEZ MACIAS, NOTARIA INTERINA** de este cantón, comparecen a la celebración de la presente escritura, por una parte los señores: EUSEBIA DOMITILA GARCIA BRIONES, casada, ejecutiva del hogar; EULALIA AUXILIADORA GARCIA BRIONES, viuda, ejecutiva del hogar; ROSA FILADELFIA GARCIA BRIONES, soltera, ejecutiva del hogar; LAUREANO CLAUDIO GARCIA BRIONES, soltero, estudiante; SOLANDA MARGARITA GARCIA BRIONES, casada, estudiante; y RAMÓN EDUARDO GARCIA BRIONES, soltero, estudiante; y por otra parte los cónyuges señor NOE ALADINO CASTRO CARREÑO y doña LUCIA VICTORIA GARCIA BRIONES, comerciante y ejecutiva del hogar, en su orden. Los comparecientes son ecuatorianos, mayores de edad, domiciliados en este cantón, hábiles para contratar y a quienes de conocerlos por medio de este acto doy fe. Bien instruidos en el objeto y resultados de esta escritura de pública de **VENTA DE DERECHOS Y ACCIONES HEREDITARIAS** a cuyo otorgamiento proceden con amplia y entera libertad, de una manera

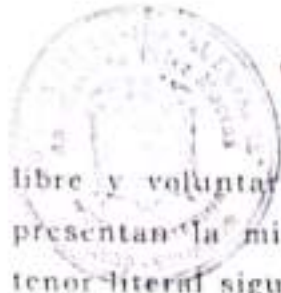

libre y voluntaria a fin de que surtan los efectos legales, me presentan la minuta y los documentos habilitantes que son del tenor literal siguiente: **Señora Notaria:** En el registro de escrituras públicas a su muy digno cargo, sirvase autorizar una, por la cual conste la de VENTA DE DERECHOS Y ACCIONES HEREDITARIAS de conformidad con las cláusulas que a continuación se expresan:

PRIMERA:- Intervinientes:- Comparecen a la celebración de la presente escritura, por una parte, por sus propios derechos, los señores EUSEBIA DOMITILA, EULALIA AUXILIADORA, ROSA FILADELFIA, LAUREANO CLAUDIO, SOLANDA MARGARITA y RAMÓN EDUARDO GARCIA BRIONES, quienes intervienen en calidad de "Vendedores"; y, por otra, los cónyuges señor NOE ALADINO CASTRO CARREÑO y doña LUCIA VICTORIA GARCIA BRIONES, en calidad de "Compradores". Todos con capacidad legal para obligarse y contratar.- SEGUNDA:- Antecedentes:- El señor RAMON GARCIA VELIZ, conjuntamente con la señora Delia Briones Mantuano adquirieron un lote de terreno, denominado "Sarita", ubicado en la parroquia Velasco Ibarra, del cantón El Empalme, provincia del Guayas, comprendido dentro de los siguientes linderos y medidas: POR EL NORTE: Con Eusebia García, con noventa y ocho metros trece centímetros rumbo variable, con Laureano García, en doscientos cuarenta y seis metros cinco centímetros rumbo variable, ochenta y dos metros sesenta y un centímetros R.N., treinta y ocho grados siete minutos seis segundos E, con Amado García, en ciento diecinueve metros cuarenta y un centímetros R.S., setenta grados diez minutos treinta y nueve segundos E, cuarenta metros once centímetros R.N., cuatro grados diecisiete minutos veintiún segundos E, con Galo Palacios, en cuatrocientos veintisiete metros sesenta y cuatro centímetros rumbo variable, POR EL SUR: Con Donato García, en veintisiete metros treinta y nueve centímetros R.N., cuarenta y ocho grados ocho minutos veintiún segundos W, cincuenta y tres metros cincuenta y cinco centímetros rumbo

Ab. Marlene Vélez Macías

NOTARIA INTERINA

Avda. Quevedo No. 141 Auhing

Telefax: 04-2961850

El Empalme - Guayas - Ecuador



variable, cincuenta metros un centímetro R.N., setenta y cinco grados cuarenta y cuatro minutos cuarenta y cinco segundos W, ciento cincuenta y ocho metros diez centímetros R.N., cincuenta y un grados diez minutos trece segundos W, treinta y cuatro metros ochenta y dos centímetros R.S., treinta y nueve grados diez minutos veinticinco segundos W, setenta y dos metros once centímetros R.N., setenta grados treinta y tres minutos treinta y seis segundos W, ciento ochenta y nueve metros sesenta y dos centímetros R.N., sesenta y tres grados cuarenta y dos minutos diecinueve segundos W, ciento veinticinco metros veinticinco centímetros R.N., cincuenta y un grados veintiocho minutos cincuenta y nueve segundos W, doscientos cincuenta y nueve metros noventa y dos centímetros N., ochenta grados un minuto cuarenta y nueve segundos W, cincuenta y dos metros tres centímetros R.N., ochenta y siete grados cuarenta y siete minutos cincuenta y un segundos W, sesenta y dos metros treinta y seis centímetros R.S., setenta y siete grados cincuenta y ocho minutos diez segundos W, POR EL ESTE: Con el río Maçul, en seiscientos cuarenta y siete metros tres centímetros siguiendo su curso; y, POR EL OESTE: Con carretero Balzar - El Empalme, en cuarenta y cuatro metros veintiocho centímetros, R.N., treinta y siete grados ocho minutos cuarenta y ocho segundos E.- Todo lo cual encierra una superficie total de DIECIOCHO HECTAREAS CON MIL NOVECIENTOS TREINTA Y SEIS AREAS.- Esta propiedad la adquirió por venta que le hizo el señor Horacio Camino Ochoa y cónyuge, según escritura pública celebrada ante el Notario del cantón Balzar, señor Luis Aldas Montoya, el dieciocho de marzo de mil novecientos setenta y cuatro, inscrita en el Registro de la Propiedad del cantón Balzar, y reinscrita posteriormente en el Registro de la Propiedad del cantón El Empalme, el cuatro de junio de mil novecientos noventa y tres, con el número ciento ochenta y cinco.- TERCERA:- Sucesión.- Al fallecimiento de los cónyuges señor Ramón García Veliz y doña Delia Briones Mantuano,

Marlene Vélez Macías
NOTARIA INTERINA



hechos ocurrido el quince de noviembre de mil novecientos noventa y ocho y el treinta de abril de mil novecientos ochenta y siete, en el cantón El Empalme y la ciudad de Guayaquil, respectivamente, le sucedieron en sus bienes a sus hijos, los señores: EUSEBIA DOMITILA, EULALIA AUXILIADORA, ROSA FILADELFIA, LAUREANO CLAUDIO, LUCIA VICTORIA, SOLANDA MARGARITA y RAMÓN EDUARDO GARCIA BRIONES, quienes han cumplido con el trámite pertinente relacionado el impuesto a la herencia ante el Servicio de Rentas Internas, con el que justifican su intervención, en este instrumento publico.-

CUARTA.- Venta y Desmembración:- Con los antecedentes expuestos y de conformidad con los mismos, los señores EUSEBIA DOMITILA, EULALIA AUXILIADORA, ROSA FILADELFIA, LAUREANO CLAUDIO, SOLANDA MARGARITA y RAMÓN EDUARDO GARCIA BRIONES, libres y voluntariamente, sin presión de ninguna naturaleza, tienen a bien otorgar en venta real y enajenación perpetua, a favor de los cónyuges señor NOE ALADINO CASTRO CARREÑO y doña LUCIA VICTORIA GARCIA BRIONES, cuatro lotes de terrenos que desmembran del lote de mayor extensión, circunscritos dentro de los siguientes linderos y medidas: PRIMER LOTE DE TERRENO:- POR EL NORTE: Con callejón público, en veintidós metros, POR EL SUR: Con propiedad del señor Donato García, en veintidós metros, POR EL ESTE: Con área de reserva, con cincuenta y siete metros; y, POR EL OESTE: Con propiedad del señor Donato García, en cuarenta y tres metros ochenta y cinco centímetros, cuatro metros sesenta centímetros y cinco metros ochenta y siete centímetros.- Todo lo cual encierra una superficie total de MIL CIENTO ONCE METROS CUADRADOS; SEGUNDO LOTE DE TERRENO:- POR EL NORTE: Con área de reserva, en trescientos ochenta y ocho metros cincuenta y seis

Ad. Marlene Vélez Macías

NOTARIA INTERINA

Rioa, Quevedo No. 141 Auhung.

Teléfono: 01-2961850

C. Esmeraldas - Guayas - Ecuador.



centímetros, POR EL SUR: Con propiedad de la señora Solanda Margarita García Briones, en cuatrocientos diecinueve metros veinte centímetros, POR EL ESTE: Con el Río Macul, en veintiocho metros cuarenta y nueve centímetros; y, POR EL OESTE: Con propiedad del señor Amable Briones Mantuano, en veintitrés metros diez centímetros.- Todo lo cual encierra una superficie total de OCHO MIL OCHOCIENTOS CUARENTA Y CINCO METROS CUADRADOS; TERCER LOTE DE TERRENO:- POR EL NORTE: Con área de reserva, en treinta metros quince centímetros, POR EL SUR: Con propiedad del señor Donato García, en cuarenta y cuatro metros sesenta y dos centímetros, POR EL ESTE: Con área de reserva, en ochenta y cuatro metros veinticinco centímetros; y, POR EL OESTE: Con propiedad de la señora Solanda García Briones, en sesenta y nueve metros sesenta y ocho centímetros.- Todo lo cual encierra una superficie total de DOS MIL TRESCIENTOS DIECINUEVE METROS CUADRADOS; CUARTO LOTE DE TERRENO:- POR EL NORTE: Con propiedad del señor Amable Briones Mantuano, en treinta y cinco metros veintitrés centímetros, POR EL SUR: Con río Macul, en treinta metros noventa y tres centímetros, POR EL ESTE: Con área de reserva, en cuarenta y tres metros noventa y dos centímetros; y, POR EL OESTE: Con propiedad de la señora Solanda García Briones, en sesenta y cuatro metros dos centímetros.- Todo lo cual encierra una superficie total de TRES MIL CIENTO CINCUENTA Y DOS METROS CUADRADOS, reservándose los "Vendedores" la parte no comprendida en esta venta, transfiriéndole a favor de los "Compradores", todos los derechos, usos, goces y más beneficios que existan sobre los mencionados bienes.- QUINTA:- Precio:- El Precio pactado y convenido por la venta de los lotes de terrenos, que contiene el presente contrato, es el de venta, es la cantidad de DOS MIL DOSCIENTOS VEINTIOCHO DOLARES CON NUEVE CENTAVOS DE DÓLAR AMERICANOS, valor que declaran los "Vendedores", haberlos recibido en su totalidad en dinero en efectivo)

Ad. Marlene Vélez Macías
NOTARIA INTERINA



hechos ocurrido el quince de noviembre de mil novecientos noventa y ocho y el treinta de abril de mil novecientos ochenta y siete, en el cantón El Empalme y la ciudad de Guayaquil, respectivamente, le sucedieron en sus bienes a sus hijos, los señores: EUSEBIA DOMITILA, EULALIA AUXILIADORA, ROSA FILADELFIA, LAUREANO CLAUDIO, LUCIA VICTORIA, SOLANDA MARGARITA y RAMÓN EDUARDO GARCIA BRIONES, quienes han cumplido con el trámite pertinente relacionado el impuesto a la herencia ante el Servicio de Rentas Internas, con el que justifican su intervención, en este instrumento público.-

CUARTA.- Venta y Desmembración:- Con los antecedentes expuestos y de conformidad con los mismos, los señores EUSEBIA DOMITILA, EULALIA AUXILIADORA, ROSA FILADELFIA, LAUREANO CLAUDIO, SOLANDA MARGARITA y RAMÓN EDUARDO GARCIA BRIONES, libres y voluntariamente, sin presión de ninguna naturaleza, tienen a bien otorgar en venta real y enajenación perpetua, a favor de los cónyuges señor NOE ALADINO CASTRO CARREÑO y doña LUCIA VICTORIA GARCIA BRIONES, cuatro lotes de terrenos que desmembran del lote de mayor extensión, circunscritos dentro de los siguientes linderos y medidas: PRIMER LOTE DE TERRENO:- POR EL NORTE: Con callejón público, en veintidós metros, POR EL SUR: Con propiedad del señor Donato García, en veintidós metros, POR EL ESTE: Con área de reserva, con cincuenta y siete metros; y, POR EL OESTE: Con propiedad del señor Donato García, en cuarenta y tres metros ochenta y cinco centímetros, cuatro metros sesenta centímetros y cinco metros ochenta y siete centímetros.- Todo lo cual encierra una superficie total de MIL CIENTO ONCE METROS CUADRADOS; SEGUNDO LOTE DE TERRENO:- POR EL NORTE: Con área de reserva, en trescientos ochenta y ocho metros cincuenta y seis

Ab. Marlene Vélez Macías

NOTARIA INTERINA

Calle Quevedo No. 141 Auhing


Teléfono: 04-2961830

El Empalme - Guayas - Ecuador



centímetros, POR EL SUR: Con propiedad de la señora Solanda Margarita García Briones, en cuatrocientos diecinueve metros veinte centímetros, POR EL ESTE: Con el Río Macul, en veintiocho metros cuarenta y nueve centímetros; y, POR EL OESTE: Con propiedad del señor Amable Briones Mantuano, en veintitrés metros diez centímetros.- Todo lo cual encierra una superficie total de OCHO MIL OCHOCIENTOS CUARENTA Y CINCO METROS CUADRADOS; TERCER LOTE DE TERRENO:- POR EL NORTE: Con área de reserva, en treinta metros quince centímetros, POR EL SUR: Con propiedad del señor Donato García, en cuarenta y cuatro metros sesenta y dos centímetros, POR EL ESTE: Con área de reserva, en ochenta y cuatro metros veinticinco centímetros; y, POR EL OESTE: Con propiedad de la señora Solanda García Briones, en sesenta y nueve metros sesenta y ocho centímetros.- Todo lo cual encierra una superficie total de DOS MIL TRESCIENTOS DIECINUEVE METROS CUADRADOS; CUARTO LOTE DE TERRENO:- POR EL NORTE: Con propiedad del señor Amable Briones Mantuano, en treinta y cinco metros veintitrés centímetros, POR EL SUR: Con río Macul, en treinta metros noventa y tres centímetros, POR EL ESTE: Con área de reserva, en cuarenta y tres metros noventa y dos centímetros; y, POR EL OESTE: Con propiedad de la señora Solanda García Briones, en sesenta y cuatro metros dos centímetros.- Todo lo cual encierra una superficie total de TRES MIL CIENTO CINCUENTA Y DOS METROS CUADRADOS, reservándose los "Vendedores" la parte no comprendida en esta venta, transfiriéndole a favor de los "Compradores", todos los derechos, usos, goces y más beneficios que existan sobre los mencionados bienes.- QUINTA:- Precio:- El Precio pactado y convenido por la venta de los lotes de terrenos, que contiene el presente contrato, es el de venta, es la cantidad de DOS MIL DOSCIENTOS VEINTIOCHO DOLARES CON NUEVE CENTAVOS DE DÓLAR AMERICANOS, valor que declaran los "Vendedores", haberlos recibido en su totalidad en dinero en efectivo

Ab. Marlene Vélez Macías
NOTARIA INTERINA

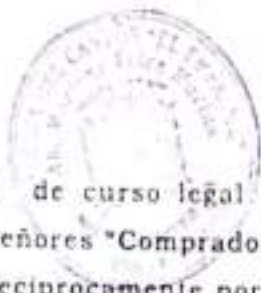

y de curso legal y a su entera satisfacción de manos de los señores "Compradores", sin que las partes nada tengan que reclamarse reciprocamente por este ni por ningún otro concepto, aclarando los "Vendedores", que renuncian a intentar acción legal alguna por la lesión enorme que pudiere existir, ya que el precio fijado y pagado es el justo.- SEXTA.- Saneamiento.- Los señores "Vendedores", declaran que sobre los lotes de terrenos, que es objeto de esta venta no pesa ni existe ningún gravamen, prohibición de enajenar, hipoteca o embargo que impida su traspaso, no obstante de aquello, se obliga al saneamiento por evicción o vicios redhibitorios, en todos los casos contemplados en la Ley, transferencia que comprende el dominio, posesión y señorío, con todas sus entradas y salidas, aumentos de superficie, costumbres, servidumbres, plantaciones, árboles de madera de diferentes especies, árboles frutales, cultivos, cerramientos, viviendas, construcciones, establos, mejoras introducidas y cualquier otro derecho inherente a la propiedad objeto de esta compraventa.- SÉPTIMA.- Gastos y Facultad para Inscribir.- Todos los gastos que demande la celebración y suscripción de la presente escritura pública, corre de cuenta y cargo de los "Compradores", quien además queda facultada o autorizada para solicitar la inscripción, de este contrato traslativo en el Registro de la Propiedad pertinente.- OCTAVA.- Aceptación.- Los cónyuges señor NOE ALADINO CASTRO CARREÑO y doña LUCIA VICTORIA GARCIA BRIONES, acepta la presente venta por ser a su favor, por convenir a sus intereses. Usted señora Notaria, sírvase agregar las demás cláusulas de estilo necesario para la completa y perfecta validez de la presente escritura pública. f) Abogado Lenin García Parraga con Registro número nueve mil cuatrocientos seis de Colegio de Abogados del Guayas. HASTA AQUÍ LA MINUTA QUE SE ELEVA A ESCRITURA PÚBLICA. Se dio fiel cumplimiento con el pago de impuestos de Alcabalas y sus Adicionales. LEIDA que fue esta escritura de principio a fin a los

El Registrador de la Propiedad de este Cantón, **CERTIFICA:** Que revisados los Registros de esta oficina, según sus índices, desde el dos de Enero de mil novecientos noventa y tres, hasta esta fecha, aparece que: **RAMON GARCIA VELIZ**, es propietario de un lote de terreno denominado "Sarita", ubicado en la Parroquia Velasco Ibarra, Cantón El Empalme, Provincia del Guayas, comprendido dentro de los siguientes linderos y medidas: **POR EL FRENTE:** Carretero Empalme Balzar; **POR ATRAS:** Propiedad de Antonio Carriel Montoya; **POR EL COSTADO DERECHO:** Propiedad del señor Segundo Idrovo López, en la actualidad del señor Suarez Litardo, en parte con la de Víctor Vicente Carriel; y, **POR EL COSTADO IZQUIERDO:** Propiedad que fue de Genaro Hernández, hoy los señores Ramón Veliz Garcia y Marcial Veliz.- Esta propiedad la adquirió mediante venta que le hizo el señor Horacio Camino Ochoa y cónyuge, según escritura celebrada ante el Notario del Cantón Balzar, Sr. Luis Aldás Montoya, el 18 de Marzo de 1974, inscrita en el Registro de la Propiedad del cantón Balzar y reinscrita posteriormente en el Registro de la Propiedad del Cantón El Empalme, el 4 de Junio de 1993, con el número 185.- Es todo cuanto puedo informar en honor a la verdad y fidelidad del archivo que se encuentra a mi cargo.- El Empalme, Octubre 27 del 2011.- El Registrador de la Propiedad.

Y*Z*V



REGISTRO DE LA PROPIEDAD Y MERCANTIL
DEL CANTÓN EL EMPALME

[Firma]
Sr. Johnny Alcivar Veliz
REGISTRADOR

[Firma]
D. Marlene Vélez N.
NOTARIA INTER



AREA
18,1936 Has.



ACION

del Guayas
El Empalme
Velasco Ibarra
El Porvenir

LEVANTAMIENTO PLANIMETRICO

Sr. RAMON GARCIA VELIZ

Lev y Cálculo

Ing. Guido Conzong V.

Fecha

Enero del 2011

Escala

1:4500

INSCRIPCION DE DEFUNCION

Tomo 81 Pág. 23

En El Cuzco, hoy día Diez de Noviembre del año 1968

Yo Guillermo Huerta Ponce, Jefe de Registro Civil, en

virtud de la presente acta de inscripción de la defunción de:

NOMBRES Y APELLIDOS DEL FALLECIDO.

Jose Leon Cerezo Uña

Sexo: Varón Estado Civil: Unido Edad: Setenta y seis años

Nombres y Apellidos de la madre: María Uña

Lugar del fallecimiento: El Cuzco Fecha: Noviembre 1968

de El Cuzco de mil novecientos sesenta y ocho El Conyuge su

breviamente se llama: Guillermo Huerta Ponce

Causa de la muerte: Defecto cardíaco

Solicitó esta inscripción: Guillermo Huerta Ponce con Cédula

de Identidad No 10011495-9 domiciliado en El Cuzco

León Huerta Ponce

Observaciones:

Se declara la defunción de María Leon Cerezo Uña



FIRMAS:

Guillermo Huerta Ponce

CERTIFICADO DE DECLARATORIA DE PRESCRIPCIÓN

NO. HER- N° 112012011CATN000143

Nombre del Causante: **DELIA BRIONES MANTUANO**

Fecha de Fallecimiento: **30 DE ABRIL 1987**

Clase de Sucesión: Testada () Intestada (X)

Por cuanto de los datos que anteceden se deduce que ha prescrito la acción del Fisco, no hay lugar al pago de Impuesto a la Renta Sobre Ingresos Provenientes de Herencias y/o Legados en la presente sucesión de Conformidad con la ley. Confiero por **DUPLICADO** la presente Declaratoria de Prescripción.

OBSERVACIONES:

La presente Declaratoria fue emitida al amparo de la Ley de Régimen Tributario Interno, en concordancia con el Código Tributario, por cuanto a la fecha de sucesión se encontraban vigentes y regían para el cálculo y Prescripción, respectivamente del impuesto referido.

Harlene Vélez Macías
SECRETARIA INTERINA

Cecilia Caicedo Astudillo
Ing. Cecilia Caicedo Astudillo
Directora Provincial del
Servicio de Rentas Internas Los Ríos



Lugar y Fecha: **Babahoyo, 30 de marzo del 2011**

N°. 112052011000962

La emisión de este certificado ha sido conferido sin costo alguno.

UNIDAD DE SUCESIONES

CERTIFICADO DE PRESCRIPCION

Nombre del Causante: JOSE RAMON GARCIA VELIZ


Fecha de Fallecimiento: 15 DE NOVIEMBRE DE 1998

Clase de Sucesión: Testada () Intestada (X)

Por cuanto de los datos que anteceden se deduce que ha caducado la acción del Fisco, no hay lugar al pago de impuestos a la Renta Sobre Ingresos Provenientes de Herencias y/o Legados en la presente sucesión de conformidad con la Ley. Confiero por DUPLICADO la presente Declaratoria de Prescripción.

OBSERVACIONES:

La presente Declaratoria fue emitida al amparo de la Ley de Régimen Tributario Interno, en concordancia con el Código Tributario, por cuanto a la fecha de sucesión se encontraban vigentes y regían para el cálculo y Prescripción, respectivamente del impuesto referido.

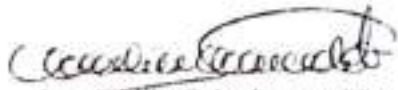
Ing. Cecilia Caicedo Astudillo
Directora Provincial del
Servicio de Rentas Internas Los Ríos

Lugar y Fecha: Babahoyo, 30 de marzo del 2011

N°. 112052011000963

La emisión de este certificado ha sido conferido sin costo alguno.

AVISO DE PAGO DE ALCABALAS Y ADICIONALES

Aviso No. 891

El Empalme, 27 de Octubre del 2011

Señor.

TESORERO MUNICIPAL DEL CANTÓN EL EMPALME.

Presente.

Sírvase encontrar usted la información y el detalle de los Impuestos De la transferencia de dominio que se va a celebrar en la Notaria a Mi cargo y que a continuación se detalla:

OTORGANTE: JOSE RAMÓN GARCIA VELIZ. C.C. No. 090286574-0

BENEFICIARIO: LUCIA V. GARCIA BRIONES Y CONY. C. C. No. 120252715-4

VALOR DEL CONTRATO \$ 2.228.09

AVALUO COMERCIAL \$ 2.228.09

IMPUESTO A PAGAR SOBRE \$ 2.228.09

UBICACIÓN DEL INMUEBLE: El Porvenir, de la parroquia Velasco
Cantón El Empalme, Provincia del Guayas.

ALCABALAS:	1%	\$ 22.28
Junta de Beneficencia de Guayaquil	0,3%	\$ 6.68

TOTAL A PAGAR..... \$ 28.96



OBSERVACIONES: -


Ab. Marlene Vélez Macías
Notaria Interina
Cantón El Empalme



Ab. Marlene Vélez Macías
NOTARIA INTERINA

COMPROBANTE DE INGRESO A CAJA

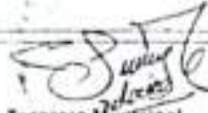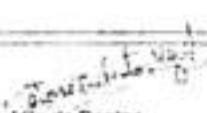Contribuyente:	Cédula: RUC - Código Catastral	Código de Transacción
TÍTULO DE CERTIFICADO DE AVALUO No. 011079 AÑO: 2011		
Concepto: PARA SOLICITUD DE AVALUOS		
A Feliciano (socio) Sr. interesado CERTIFICAR: Que revisados los expedientes de esta Dependencia Municipal a mi cargo se ha emitido el AVALUO Comercial con los siguientes datos: DIRECCIÓN DEL PREDIO: VILLARCO IBARRA-EL PORVENIR CLAVE CATASTRAL: 0000001661 Es importante hacer notar en honor a la verdad y en mérito al instrumento que tengo a su disposición para el deslinde de las fincas: AVALUO COMERCIAL DEL AÑO 2011 US\$ 1277.46 SUPERFICIE: 0.8845MAS. NOMBRE DEL PREDIO: FINCA SANITA AVALUO PROPORCIONAL - LOSE # 6		
		
 Director Financiero	 Tesorero Municipal	 Jefe de Rentas

\$2,0



N° 0067224.....0,00
 DESCUENTO:0,00
 RECARGO-INTERES:0
 VALOR TOTAL:2,00
 DEUDA ANTERIOR:0,00
 TOTAL COBRADO:2,00



ILUSTRE MUNICIPALIDAD DE EL EMPALME

COMPROBANTE DE INGRESO A CAJA

Mes: 10	Día: 7	Año: 2011	Cajero: VILLARCO	N°: 0007
---------	--------	-----------	------------------	----------

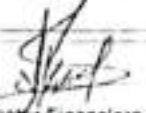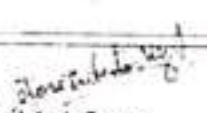Contribuyente:	Cédula: RUC - Código Catastral	Código de Transacción
TÍTULO DE ALCABALA No. 007081 AÑO: 2011		
Concepto: COSTO DE PROCESO Y EMISIÓN		
ALCABALAS		
JUNTA DE BENEFICENCIA GUAYAQUIL		
ALCABALA Y SUS ADICIONALES COMPRA-VENTA (PREDIO RURAL): BENEFICIARIO: GARCIA BRIONES-LUCIA VICTORIA 1202527154 LUGAR: SITIO EL PORVENIR NOTARIA: DE EL EMPALME AVISO: 1001 B.IMP: 2228,69		
		
 Director Financiero	 Tesorero Municipal	 Jefe de Rentas

N° 0087645.....10,96
 DESCUENTO:0,00
 RECARGO-INTERES:0
 VALOR TOTAL:10,96
 DEUDA ANTERIOR:0,00
 TOTAL COBRADO:10,96

RECIBO PAGO

Fecha: 10/10/11
 Lugar: El Empalme
 Cliente: 100-10 1245485004
 Nombre: C. RUC: 0000001661
 Documento: 24/10/11
 Efectivo: 2,00
 Total: 2,00
 Recibo: 2,00
 Oficina: 100-10 1245485004
 Fecha: 10/10/11
 Control: 100-10 1245485004
 Oficina: 100-10
 Valor: 2,00

E 124612622

Alta victoria *Saunders* 1910

2000-2001

LUI CARRENO

HALTAP

29/09/2016

COMPTON-RECORDS 37E 8187-100

NUMBER OF DAYS TO 100% PATIENTS

24 JUN 1954

100% 0.47% 0.00% 0.00%

[illegible]

4245751

15

CBI

INSTITUTO NACIONAL DE
CERTIFICADO DE V

253-0018
NUMERO

1301048318
CFCU-A

CASTRO CARRENO NOE ALADINO

DISCUSSION

EL ENFERMEDAD

INDEX

Case 20

WILLIAMS, J. H. 1993.

1997

© 1998 Lippincott Williams & Wilkins

ILUSTRE MUNICIPALIDAD DE EL EMPALME

COMPROBANTE DE INGRESO A CAJA

Mes 01	Dia 24	Año 2011	Cajero AFALCONI	Nº 03021
--------	--------	----------	-----------------	----------

Contributors:

Código FISCAL - Código Catastral	Código de Transacción
----------------------------------	-----------------------

TITULO DE CERTIFICADO DE AVALUO No: 011076 AÑO: 2011

Concepto	PARA SOLICITUD DE AVALUOS
----------	---------------------------

*****2.00

A petición verbal del interesado CERTIFICO:
Que revisado los archivos de esta Dependencia Municipal a mi cargo
se ha constatado que existe el Avaluo Comercial con los siguientes datos
DIRECCION DEL PREDIO: VELASCO IDARRA-EL PORVENIR.
CLAVE CATASTRAL: 09085501641
Así todo cuanto puerdo informar en honor a la verdad y en mérito al
juramento que tengo prestado para el desempeño de mis funciones.
AVALUO COMERCIAL DEL AÑO 2011 USD\$ 160.46 SUPERFICIE: 0.1111HAS.
NOMBRE DEL PREDIO: FINCA BANITA
AVALUO PROPORCIONAL - LOTE # 3

\$2,00

Nº	0067221...
UBTOTAL	0067221...
DESCUENTO:	*****0,00
RECARGO-INTERES:	*****0,00
VALOR TOTAL +	*****2,00
LEUDA ANTERIOR:	*****0,00
TOTAL CORRADO:	*****2,00



1. 空位与空位型态之关系如下:

2000年12月

[illegible]

Director Financiero

Tesoro Municipal

Jefe de Rentas



ILUSTRE MUNICIPALIDAD DE EL EMPALME

COMPROBANTE DE INGRESO A CAJA

EMPALME VELIZ JOSE RANCOS

Mes 03	Dia 24	Año 2011	Cajero/FALCONI	N° 0002
--------	--------	----------	----------------	---------

Contribuyente:

Cedula: RUC Código Catastral Código de Trámite

TITULO DE CERTIFICADO DE AVALUO No. 011083 AÑO: 2011

Concepto: PARA SOLICITUD DE AVALUOS *****2,00

A Petición Verbal del interesado CERTIFICO:
 Que revisado los archivos de esta Dependencia Municipal a mi cargo
 se ha constatado que existe el Avaluo Comercial con los siguientes datos:
 DIRECCION DEL PREDIO: VELASCO IBARRA-EL PORVENIR
 CLAVE CATASTRAL: 09085501641
 Es todo cuanto puedo informar en honor a la verdad y en merito al
 juramento que tengo prestado para el desempeño de mis funciones.
 AVALUO COMERCIAL DEL AÑO 2011 US\$ 334.93 SUPERFICIE: 0.2319HAS.
 NOMBRE DEL PREDIO :FINCA SARITA
 :: AVALUO PROPORCIONAL - LOTE # 10

\$2,00

N° VISTOTA 0067228

DESCUENTO:
 RECARGO-INTERES:
 VALOR TOTAL :
 DEUDA ANTERIOR:
 TOTAL COBRADO:



2011139011083

219417 11-04-2011

 Director Financiero

 Tesorero Municipal

 Jefe de Rentas

DIRECCION FINANCIERA - TESORERIA

.....
 n. Martene Vélez IB
 NOTARIA INTER



ILUSTRE MUNICIPALIDAD DE EL EMPALME

COMPROBANTE DE INGRESO A CAJA

EMPALME VELIZ JOSE RANCOS

Mes 03	Dia 24	Año 2011	Cajero/FALCONI	N° 00030
--------	--------	----------	----------------	----------

Contribuyente:

Cedula: RUC Código Catastral Código de Trámite

TITULO DE CERTIFICADO DE AVALUO No. 011085 AÑO: 2011

Concepto: PARA SOLICITUD DE AVALUOS *****2,00

A Petición verbal del interesado CERTIFICO:
 Que revisado los Archivos de esta Dependencia Municipal a mi cargo,
 se ha constatado que existe el Avaluo Comercial con los siguientes datos:
 DIRECCION DEL PREDIO: VELASCO IBARRA-EL PORVENIR
 CLAVE CATASTRAL: 09085501641
 Es todo cuanto puedo informar en honor a la verdad y en merito al
 juramento que tengo prestado para el desempeño de mis funciones.
 AVALUO COMERCIAL DEL AÑO 2011 US\$ 455.24 SUPERFICIE: 0.3152HAS.
 NOMBRE DEL PREDIO :FINCA SARITA
 :: AVALUO PROPORCIONAL - LOTE # 12

\$2,00

N° VISTOTA 0067230

DESCUENTO:
 RECARGO-INTERES:
 VALOR TOTAL :
 DEUDA ANTERIOR:
 TOTAL COBRADO:



2011139011085

219417 11-05-10:00

 Director Financiero

 Tesorero Municipal

 Jefe de Rentas

DIRECCION FINANCIERA - TESORERIA



UBICACION

Prov. del Guayas
Cantón El Empalme
Parroquia Velasco Ibarra
Sector El Porvenir



[Signature]
Mariene Vélez Mac
NOTARIA INTERINA

DESMEMBRACION

LOTE No. 10
LUCIA VICTORIA GARCIA BRIONES

Lev. y Calculo:

[Signature]
Fco. Guido Brindley
Ing. Civil

Fecha

Enero del 2011

Escala

1:600

CORESEP 1006-10-1004523




LOte No. 5
AMABLE ALCIDES BRIONES MANTUANO



UBICACION

Prov. del Gu.
Cantón El Em
Parroquia Velas
Sector El Po.

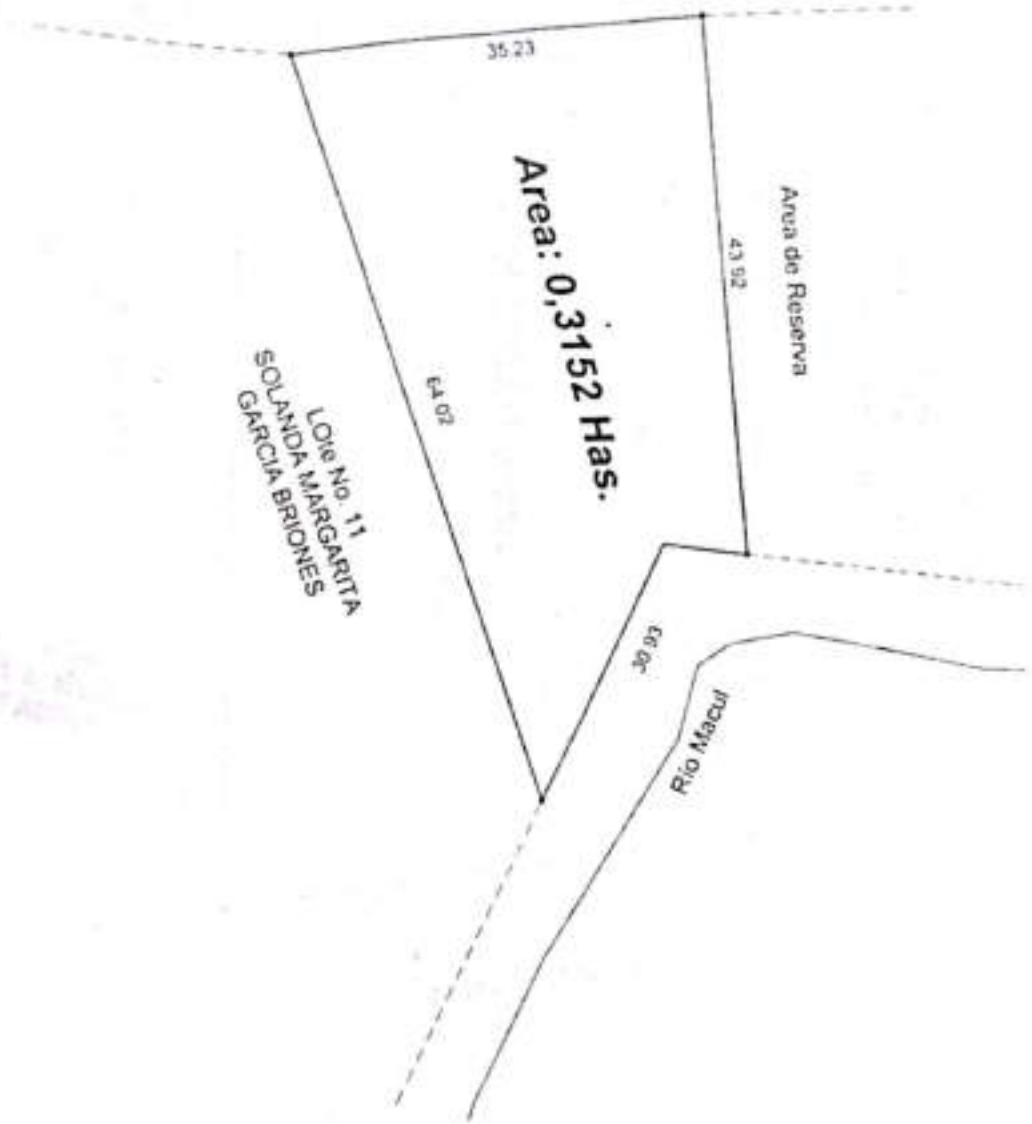

DESMEMBRACION

LOTE No. 12
LUCIA VICTORIA GARCIA BRIONES

Lev. y Calculo

[Signature]
[Signature]

Fecha

Enero

Escala

Reg. Prof. 02-2162

CINESUP 1006-10-100457



UBICACION

Prov. del Guayas
Cantón El Empalme
Parroquia Velasco Ibarra
Sector El Porvenir



DONATO GARCIA

Callejón Público

22.00

43.85

Area: 0,1111Has.

57.00

Area de Reserva

5.87
4.60

22.00

DONATO GARCIA

DESMEMBRACION

LOTE No. 3

NOE ALADINO CASTRO CARREÑO

Lev. y Cálculo

[Signature]
[Signature]

Fecha


Enero de 2011

Escala

1:500

CONF.SUP 1006-10-1004

S
UBICACION
 Prov. del Guayas
 Canton El Empalme
 Parroquia Velasco Ibarra
 Sector El Porvenir

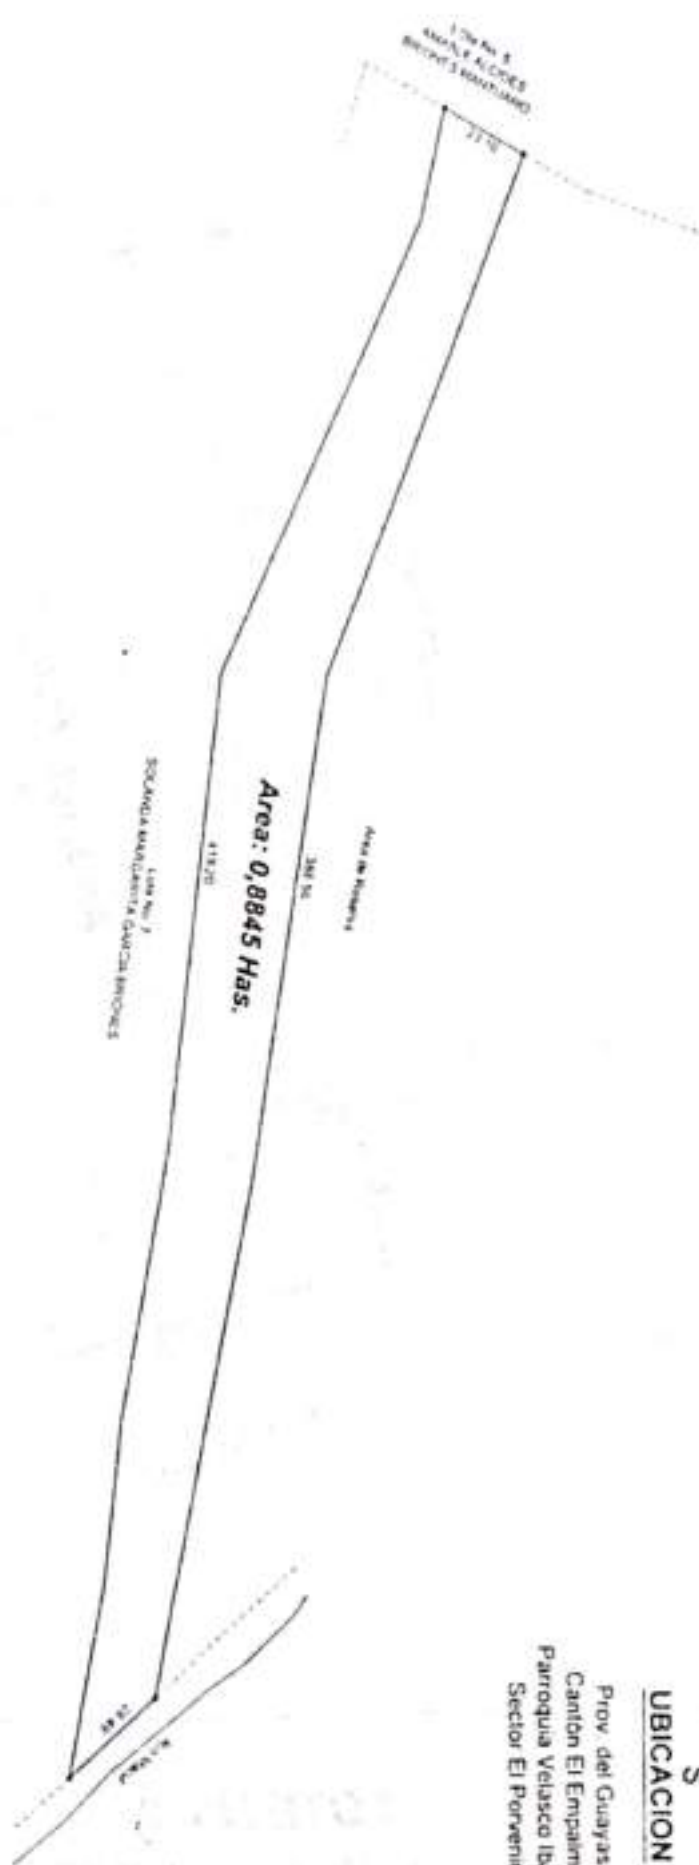

DESMEMBRACION		Lev. y Clave	Fecha
LOTE No. 6 LUCIA VICTORIA GARCIA BRIONES		<i>[Signature]</i> Ing. Guido Cordero O. Ing. Guido Cordero O. Ing. Guido Cordero O.	Enero del 2011 Encal.
		CONF-SUP-1006-10-100423	1 1750

REPÚBLICA DEL ECUADOR
CONSEJO NACIONAL ELECTORAL
CERTIFICADO DE VOTACIÓN
REFERENDUM Y CONSULTA POPULAR 17/05/2011

120-0024
NUMERO
1202029003
CEDULA
GARCIA BRIONES RAMON EDUARDO

CANTON
EL EMPALME
PICHINZA
CANTON
PICHINZA
CANTON



Marlene Vélez Macías
NOTARIA INTERINA

CELESTANIA 090930940-3
GARCIA BRIONES SOLANDA MARGARITA
EL EMPALME/BUYAS (PUEBLO NUEVO)
1961
201-2 0199 00396 F
BALDAR
1961



EQUATORIANA***** V444314442
CASADO MARCELINO CRISTOBAL CERVANTES
SECUNDARIA ESTUDIANTE
RAMON GARCIA
DELIA BRIONES
EL EMPALME 20/10/2011
20/10/2023

4197298

REPÚBLICA DEL ECUADOR
CONSEJO NACIONAL ELECTORAL
CERTIFICADO DE VOTACIÓN
REFERENDUM Y CONSULTA POPULAR 17/05/2011

186-0120
NUMERO
0909309403
CEDULA

GARCIA BRIONES SOLANDA
MARGARITA

CANTON
PICHINZA
CANTON
PICHINZA
CANTON

[Signature]
PICHINZA





CERTIFICADO DE VOTACION

1311071094
CÉDULA

CASTRO GARCIA MARLON REINALDO

QUATE
PRINCIPAL
VELASCO BARRA
PARTICULAR

EL EMPALME
CONTINUA

1. *Phragmites australis* (Cav.) Trin. ex Steud.

**ESPACIO
EN BLANCO**

Beard

14/04/2019

1751938



1. Not a student
 2. Not a student

Marlene Vélez
STARRA INTF

**ESPACIO
EN BLANCO**

13-0214495-5

GARCIA CLAUDIO GARCIA BRIONES

1 DE MAYO DE 1.953

QUILÓMETROS PARQUE 1.462 922

PARQUE PARQUE 1.953



ECUATORIANA Y 4443 Y 4447

SAN TERA

SECUNDARIA ESTUDIANTE

BAUTIZO GARCIA

RELA BRIONES

NOTA 23 ENERO 1.997

Intestado rba

1557900

[Signature]



REPÚBLICA DEL ECUADOR
CONSEJO NACIONAL ELECTORAL
CERTIFICADO DE VOTACIÓN

135-0026 1302144959


NÚMERO CÉDULA

GARCIA BRIONES LAUREANO CLAUDIO

CANTÓN EL EMPALME

PROVINCIA DEL CANTÓN

PARROQUIA

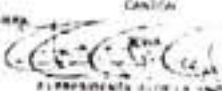

El Presidente del CNE

**ESPACIO
EN BLANCO**

GUADANA 130312661-7
 GARCIA BRIONES EUSEBIA DOMITILA
 VOTANTE
 1947
 0168 01931 F
 1947



ECUATORIANA*****
 CASADO LUIS CASTRO
 ELEMENTAL QUEHACER, DOMESTICOS
 RAMON GARCIA
 DOLIA BRIONES
 EL EMPALME
 20/04/2023


3805557



REPUBLICA DEL ECUADOR
 CONSEJO NACIONAL ELECTORAL
 CERTIFICADO DE VOTACION
 REFERENDUM Y CONSULTA POPULAR OTOS 2011
 088-0024 1303126617
 NUMERO CEDULA
 GARCIA BRIONES EUSEBIA DOMITILA
 CUARTAS EL EMPALME
 PROVINCIA CANTON
 VELASCO BARRA ZONA
 PARTICIPACION
 1. REPRESENTANTE DE LA JUNTA

A. Marlene Vélaz Macías
 NOTARIA INTERINA

ESPACIO
 EN BLANCO

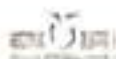

REPÚBLICA DEL ECUADOR

MINISTERIO DEL INTERIOR
DIRECCIÓN GENERAL DE ADMINISTRACIÓN
DIRECCIÓN DE IDENTIFICACIÓN



CIUDADANÍA
GARCIA BRIONES
EULALIA AUXILIADORA
NOMBRE Y APELLIDOS
MANABÍ
PORTOVELLO
ABDÓN CALCÉN
FECHA DE NACIMIENTO: 1945-02-20
NACIONALIDAD: ECUATORIANA
SEXO: F
VIRGEN
WILSON DIONISIO
CARRERO MÍO

090253403-1



ACTUACIÓN
ELEMENTAL

APPELLIDOS Y NOMBRES DEL APODOADO

GARCIA RAMON

FECHA DE NACIMIENTO Y LUGAR DE NACIMIENTO

BRIONES MANTUANO DELIA MARGARITA

(FECHA Y LUGAR DE NACIMIENTO)

QUAYAGUAL

2011-05-20

FECHA DE EXPIRACIÓN

2021-05-20


[Signature]

REVISIÓN POPULAR EN
QUEHACER, DOMESTICOS



[Signature]

V34214747

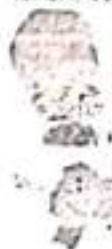

[Signature]



CNE

REPÚBLICA DEL ECUADOR
CONSEJO NACIONAL ELECTORAL

CERTIFICADO DE VOTACIÓN

REFERENDUM Y CONSULTA POPULAR 2011

087-0024
NUMERO

0902534031
CEDULA

GARCIA BRIONES EULALIA
AUXILIADORA

QUAYAS

EL EMPALME

PROVINCIA

CANTÓN

VELASCO MARRA

PARRQUIA

[Signature]

SECRETARÍA DE LA JUNTA

**ESPACIO
EN BLANCO**

Ab. Marlene Vélez Macías
NOTARIA INTERINA

Avda. Quesado No. 141 Auhing
Telefax: 04-2961830
El Empalme - Guayas - Ecuador



comparecientes por mi la Notaria, en alta voz, éstos la
aprueban en todas sus partes, se ratifican se afirman
y firman en unidad de acto conmigo la Notaria de todo
lo cual DOY FE.

Y.C.CH.

Eusebia D. Garcia Briones

EUSEBIA D. GARCIA BRIONES

Vendedora

C. C. No. 130312661-7

C. V. No. 088-0024

Eulalia A. Garcia Briones

EULALIA A. GARCIA BRIONES

Vendedora

C. C. No. 090253403-1

C. V. No. 087-0024

Rosa F. Garcia Briones

ROSA F. GARCIA BRIONES

Vendedora

C. C. No. 130224993-1

C. V. No. 095-0024

Laureano C. Garcia Briones

LAUREANO C. GARCIA BRIONES

Vendedor

C. C. No. 130214495-9

C. V. No. 135-0026

Marlene Vélez Macías
NOTARIA INTERINA

Lucia V. Garcia Briones

LUCIA V. GARCIA BRIONES

Compradora

C. C. No. 120252715-4

C. V. No. 00

Solanda M. Garcia Briones

SOLANDA M. GARCIA BRIONES

Vendedora

C. C. No. 090930940-3

C. V. No. 186-0120

9


RAMÓN E. GARCIA BRIONES

Vendedor

C. C. No. 120202900-3

C. V. No. 137-0026


NOE A. CASTRO CARREÑO

Comprador

C. C. No. 130104831-8

C. V. No. 253-0015


AB. MARLENE VELEZ MACIAS
NOTARIA INTERINA

Se otorgó ante mí, en fe de ello confiero esta **SEGUNDA COPIA CERTIFICADA**, que sello, rubrico y firmo como Notaria Interina de este cantón, a los **veinte** días del mes de **diciembre** del año **dos mil once**.


AB. MARLENE VELEZ MACIAS
NOTARIA INTERINA

Número de Repertorio:

2011- 3233

EL REGISTRO DE LA PROPIEDAD Y MERCANTIL DEL CANTÓN EL EMPALME, certifica que en esta fecha se inscribió(eron) el(los) siguiente(s) acto(s):
 1.- Con fecha Veintiocho de Diciembre de Dos Mil Once queda inscrito el Acto de mandato VENTA DE DERECHOS Y ACCIONES HEREDITARIOS en el Registro de PROPIEDADES de tomo 43 de fojas 47787 a 47819 con el número de Inscripción 10392 celebrado entre: ([GARCIA BRIONES EUSEBIA DOMITILA en calidad de VENDEDOR], [GARCIA BRIONES EULALIA AUXILIADORA en calidad de VENDEDOR], [GARCIA BRIONES ROSA FILADELFIA en calidad de VENDEDOR], [GARCIA BRIONES LAUREANO CLAUDIO en calidad de VENDEDOR], [GARCIA BRIONES EULALIA MARGARITA en calidad de VENDEDOR], [GARCIA BRIONES RAMON EDUARDO en calidad de VENDEDOR], [CASTRO CARREÑO NOE ALADINO en calidad de COMPRADOR], [GARCIA BRIONES LUCIA VICTORIA en calidad de COMPRADOR]).

Que se refiere al(los) siguiente(s) bien(es):

Cada Bien	Número	Actos
Catastral/Rol/Ident.Predial/Chasis	Ficha	
Estado de bienes Inmuebles		
XXXXXXXXXXXXXXXXXXXXXXXXXXXXXXXXXXXX	10392	VDAN(1)

DESCRIPCIÓN:

VENTA DE DERECHOS Y ACCIONES HEREDITARIOS



Dr. Jhonny Alcivar Vdaez
 Registrador de la Propiedad.