
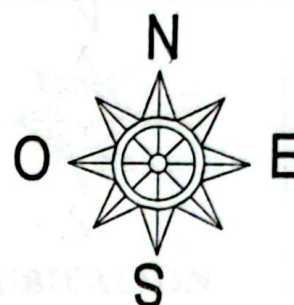
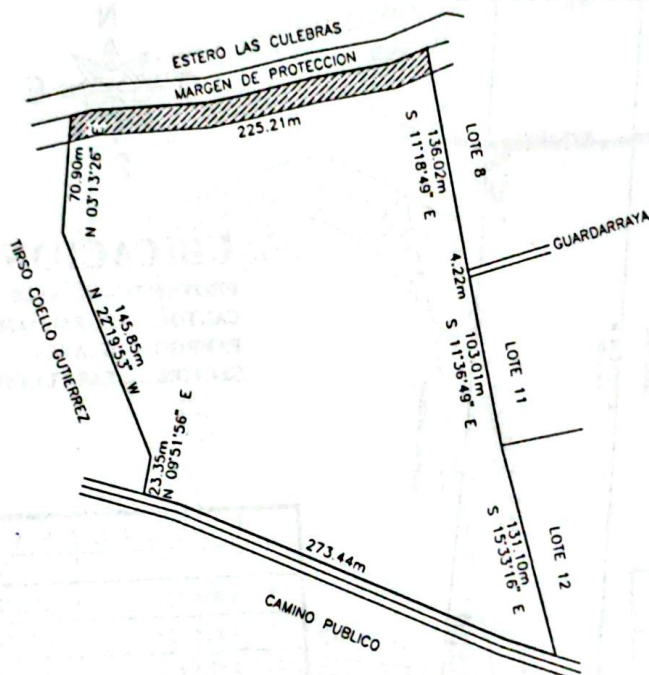


LINDEROS Y MEDIDAS	
NORTE:	Con Estero Las Culebras en 225.21m. Siguiendo su curso.
SUR:	Con Camino publico en 273.44m. Siguiendo su trazado.
ESTE:	Con Lote 8 en 136.02m. S 11°18'49" E; ancho de guardarraya en 4.22m; Lote 11 en 103.01m. S 11°36'49" E; Lote 12 en 131.10m. S 15°33'16" E.
OESTE:	Con Tirso Coello Gutierrez en 23.35m. N 09°51'56" E; 145.85m. N 22°19'53" W; 70.90m. N 03°13'26" E.

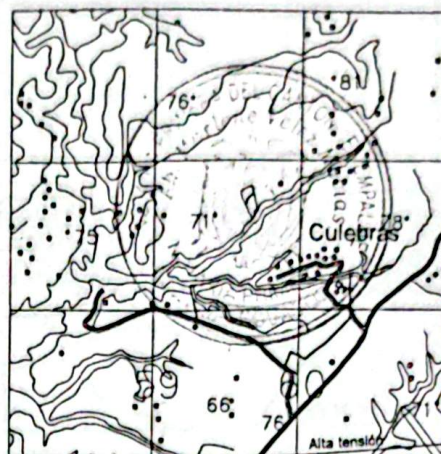

UBICACION

PROVINCIA — GUAYAS
CANTON — EL EMPALME
PARROQ. — GUAYAS
SECTOR. — LAS CULEBRAS

CUADRO DE AREAS

AREA UTIL	65520.88m ²
Margen de protección	3407.53m ²

V	COORDENADAS	
?	X	Y
?	9.884.183	659.258
?	9.884.184	659.261
?	9.884.171	659.355
?	9.884.175	659.355
?	9.884.186	659.309
?	9.884.194	659.447
?	9.884.204	659.470
?	9.884.070	659.497
?	9.884.068	659.497
?	9.883.965	659.518
?	9.883.948	659.523
?	9.883.839	659.553
?	9.883.849	659.522
?	9.883.928	659.320
?	9.883.934	659.297
?	9.883.957	659.301
?	9.884.092	659.246
?	9.884.183	659.250
Datos Tomados con GPS		
Datum: WGS 84		
Coordenadas UTM		
Zona: 17 Sur		



LEVANTAMIENTO PLANIMETRICO DEL TERRENO RURAL DE:

HDROS. DE IGNACIO JOSE DAVILA ZAMARRAGA
REMANENTE 1

Area:

65520.88m²
(6,5520HAS)

Fecha:

FEBRERO/2017

Revisó y Aprueba:

Mercedes Herrera
ARQ. MERCEDES HERRERA
DIRECTOR DE ORDENAMIENTO TERRITORIAL

Levantamiento planimetrico:

CARLOS PINCAY
TECNICO DE PLANIFICACION

Dibujó:

Nery Mora Burgos
NERY MORA BURGOS
TECNICO DE PLANIFICACION




Escala:

1:4000



LINDEROS Y MEDIDAS

NORTE	Con Estero Las Culebras en 77.09m. Siguiendo su curso.
SUR	Con Camino publico en 132.19m Siguiendo su trazado.
ESTE	Con Angel Davila Goya en 186.78m. S 07°14'02" E; 314.67m. S 08°58'29" E.
OESTE	Con Olga Suarez en 408.05m. N 07°14'34" W.

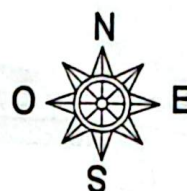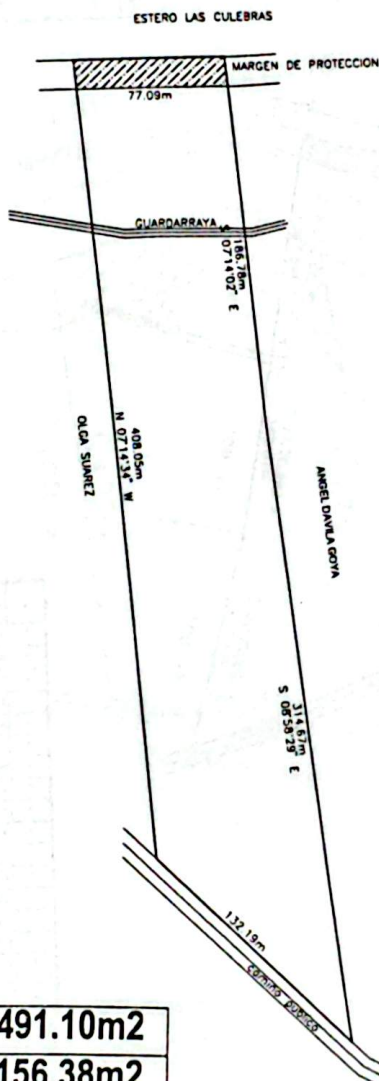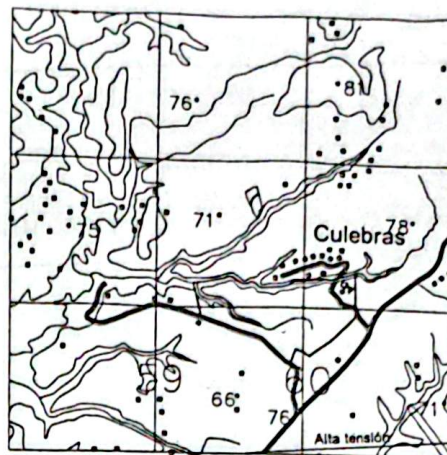

UBICACION

PROVINCIA — GUAYAS
CANTON — EL EMPALME
PARROQ. — GUAYAS
SECTOR.....LAS CULEBRAS

V	COORDENADAS	
	Y	X
?	9,884,131	659,721
?	9,884,134	659,798
?	9,883,949	659,822
?	9,883,638	659,871
?	9,883,726	659,773
?	9,884,131	659,721


Datos Tomados con GPS
Datum: WGS 84
Coordenadas UTM
Zona: 17 Sur

CUADRO DE AREAS



AREA UTIL	34491.10m ²
Margen de protección	1156.38m ²
AREA DE VIA	317.57m ²

	LEVANTAMIENTO PLANIMETRICO DEL TERRENO RURAL DE:		Area:	
	HDROS. DE IGNACIO JOSE DAVILA ZAMARRAGA REMANENTE 2		34491.10m ² (3,4491HAS)	
	Fecha:	Revisó y Aprueba:	Levantamiento planimetrico:	Dibujó:
FEBRERO/2017				
Escala:	ARQ. MERCEDES HERRERA DIRECTOR DE ORDENAMIENTO TERRITORIAL	CARLOS PINCAY TECNICO DE PLANIFICACION	NERY MORA BURGOS TECNICO DE PLANIFICACION	
1:4000				

LINDEROS Y MEDIDAS	
NORTE:	Con Estero Las Culebras en 69.00m. Siguiendo su curso.
SUR:	Con Guardarraya en 66.85m.
ESTE:	Con Olga Suarez Piloza en 117.74m.
OESTE:	Con Lote 9 en 104.75m.

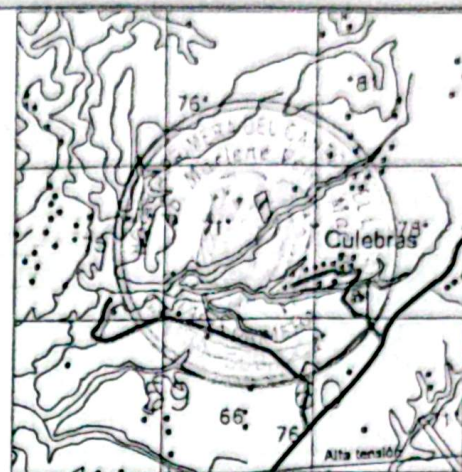

ESTERO LAS CULEBRAS
MARGEN DE PROTECCION

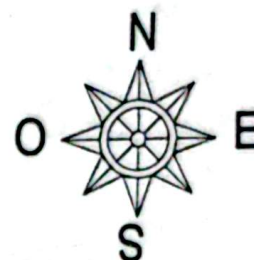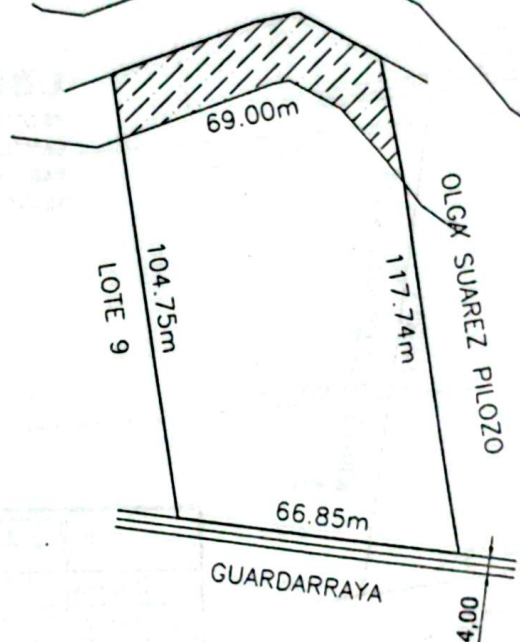

UBICACION

PROVINCIA — GUAYAS
CANTON — EL EMPALME
PARROQ. — GUAYAS
SECTOR — LAS CULEBRAS

Ab. Marlene Vélez Macías
NOTARIA PRIMERA

CUADRO DE AREAS

AREA UTIL	6482.10m ²
Margen de protección	1111.18m ²

V	COORDENADAS	
	Y	X
?	9,884,158	659,604
?	9,884,163	659,616
?	9,884,171	659,638
?	9,884,173	659,648
?	9,884,183	659,668
?	9,884,133	659,674
?	9,884,082	659,685
?	9,884,047	659,688
?	9,884,055	659,621
?	9,884,055	659,621
?	9,884,158	659,604



Datos Tomados con GPS
Datum: WGS 84
Coordenadas UTM
Zona: 17 Sur



LEVANTAMIENTO PLANIMETRICO DEL TERRENO RURAL DE:		Area	
LOTE 10		6482.10m ² (0,6482Has)	
Fecha:	Revisó y Aprobó:	Levantamiento planimétrico:	Dibujo:
FEBRERO/2017	<i>[Firma]</i>		<i>[Dibujo]</i>
Escala:	ARQ. MERCEDES HERRERA DIRECTOR DE ORDENAMIENTO TERRITORIAL	CARLOS PINCAY TECNICO DE PLANIFICACION	NERVY MORA BURGOS TECNICO DE PLANIFICACION
1:4000			


LINDEROS Y MEDIDAS

NORTE:	Con Guardarraya en 65.56m.
SUR:	Con Lote 12 en 59.98m.
ESTE:	Con Elsa Consuegra Davila en 118.77m.
OESTE:	Con Ignacio Davila en 120.78m.

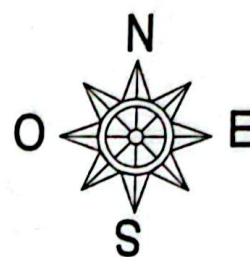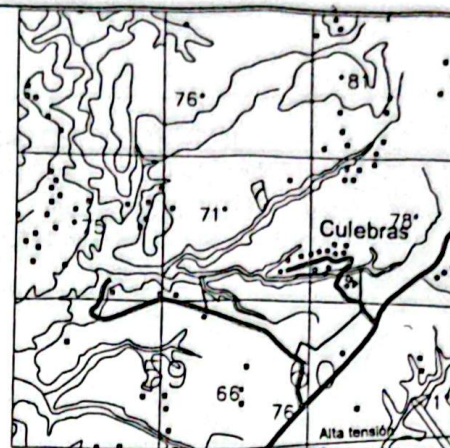

UBICACION

PROVINCIA — GUAYAS
CANTON — EL EMPALME
PARROQ. — GUAYAS
SECTOR.....LAS CULEBRAS

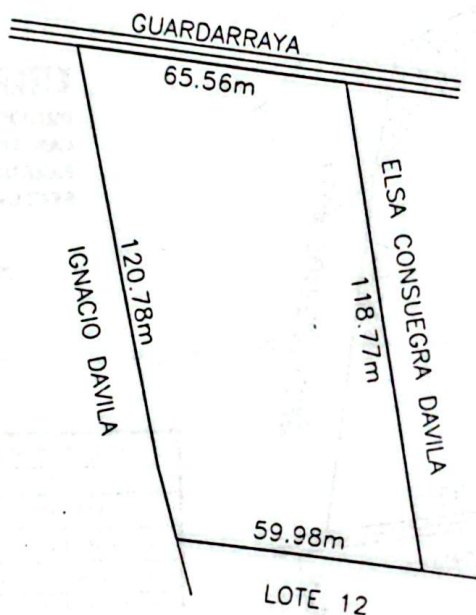

V	COORDENADAS	
	Y	X
?	9,884,066	659,497
?	9,884,060	659,545
?	9,884,058	659,562
?	9,883,941	659,582
?	9,883,948	659,523
?	9,883,965	659,518
?	9,884,066	659,497

Datos Tomados con GPS
Datum: WGS 84
Coordenadas UTM
Zona: 17 Sur

LEVANTAMIENTO PLANIMETRICO DEL TERRENO RURAL DE:

LOTE 11

Area:

**7208.74m2
(0,7208Has)**

Fecha:

FEBRERO/2017

Revisa y Aprueba:

Arq. Mercedes Herrera
ARQ. MERCEDES HERRERA
DIRECTOR DE ORDENAMIENTO TERRITORIAL

Levantamiento planimetrico:



CARLOS PINCAY
TECNICO DE PLANIFICACION

Dibuja:

Nery Mora Burgos
NERY MORA BURGOS
TECNICO DE PLANIFICACION




LINDEROS Y MEDIDAS	
NORTE:	Con Lotes 1-5-2-6 en 185.23m.
SUR:	Con Lote 3 en 182.85m.
ESTE:	Con Victoria Davila Arreaga en 48.55m ; Guardarraya en 15.21m.
OESTE:	Con Betty Davila Pilozo en 64.06m.

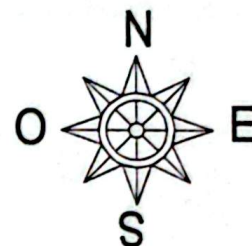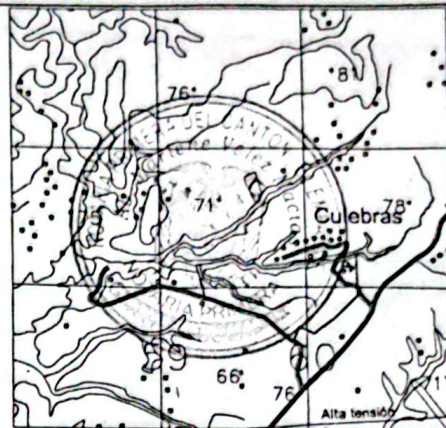

UBICACION

PROVINCIA -- GUAYAS
CANTON -- EL EMPALME
PARROQ. -- GUAYAS
SECTOR.....LAS CULEBRAS

Ab. Marlene Vélez Maci
NOTARIA PRIMERA

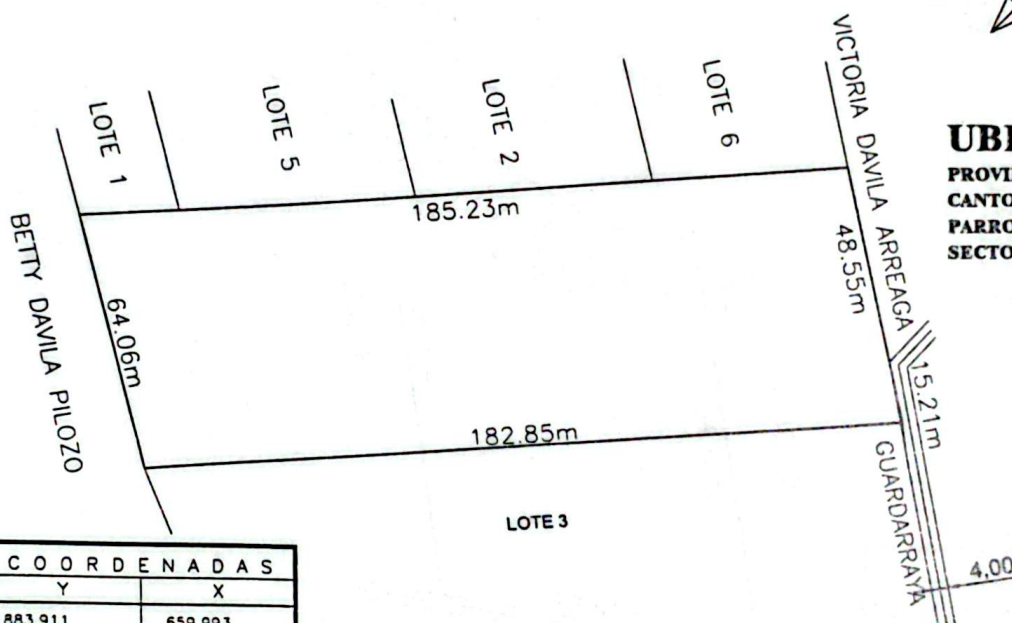

V	COORDENADAS	
	Y	X
?	9.883.911	659.993
?	9.883.927	660.175
?	9.883.927	660.175
?	9.883.876	660.183
?	9.883.861	660.184
?	9.883.846	660.004
?	9.883.888	660.002
?	9.883.888	660.002
?	9.883.911	659.993

Datos Tomados conGPS
Datum: WGS 84
Coordenadas UTM
Zona: 17 Sur



LEVANTAMIENTO PLANIMETRICO DEL TERRENO RURAL DE:

LOTE 7

Area:

11655.30m2
(1,1655Has)

Fecha:

FEBRERO/2017

Revisó y Aprobó:

Arq. Mercedes Herrera
ARQ. MERCEDES HERRERA
DIRECTOR DE ORDENAMIENTO TERRITORIAL

Levantamiento planimetrico:

CARLOS PINCAY
TECNICO DE PLANIFICACION



Dibujó:

Nery Mora Burgos
NERY MORA BURGOS
TECNICO DE PLANIFICACION

Escala:

1:4000


LINDEROS Y MEDIDAS	
NORTE:	Con Estero Las Culebras en 89.50m. Siguiendo su curso.
SUR:	Con Guardarraya en 76.81m.
ESTE:	Con Lote 10 en 104.75m.
OESTE:	Con Lote 8 en 130.64m.

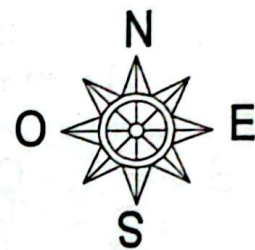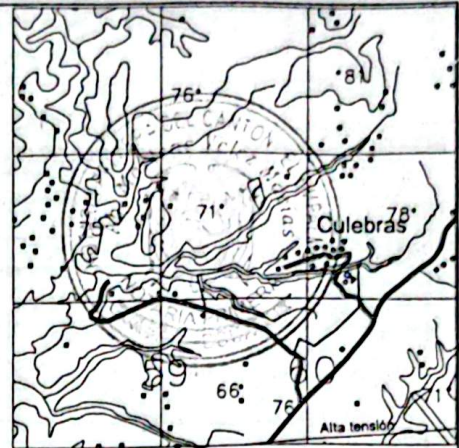

UBICACION

PROVINCIA -- GUAYAS
CANTON -- EL EMPALME
PARROQ. -- GUAYAS
SECTOR.....LAS CULEBRAS

Ab. Marlene Vélez Maci
NOTARIA PRIMERA

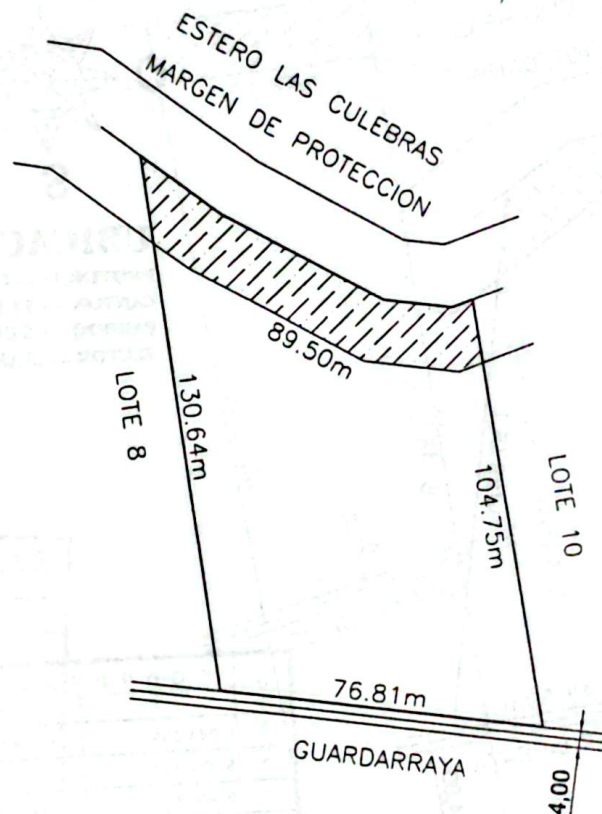

CUADRO DE AREAS

AREA UTIL	6816.93m ²
Margen de protección	1320.35m ²

V	COORDENADAS	
	Y	X
?	9,884,194	659,525
?	9,884,188	659,532
?	9,884,179	659,544
?	9,884,158	659,582
?	9,884,156	659,599
?	9,884,158	659,604
?	9,884,055	659,621
?	9,884,062	659,562
?	9,884,064	659,545
?	9,884,194	659,525

Datos Tomados conGPS
Datum: WGS 84
Coordenadas UTM
Zona: 17 Sur



LEVANTAMIENTO PLANIMETRICO DEL TERRENO RURAL DE:

LOTE 9

Area:

6816.93m²
(0,6816Has)

Fecha:

FEBRERO/2017

Revisó y Aprobó:

Arq. Mercedes Herrera
ARQ. MERCEDES HERRERA
DIRECTOR DE ORDENAMIENTO TERRITORIAL

Levantamiento planimétrico:

CARLOS PINCAY
TECNICO DE PLANIFICACION




Diseño:

Nery Mora Burgos
NERY MORA BURGOS
TECNICO DE PLANIFICACION

Escala:

1:4000

LINDEROS Y MEDIDAS	
NORTE:	Con Estero Las Culebras en 60.00m. Siguiendo su curso.
SUR:	Con Guardarraya en 48.50m.
ESTE:	Con Lote 9 en 130.64m.
OESTE:	Con Ignacio Davila en 136.02m.

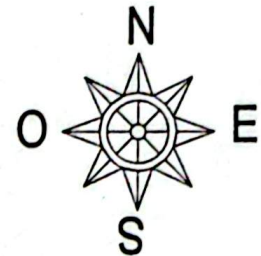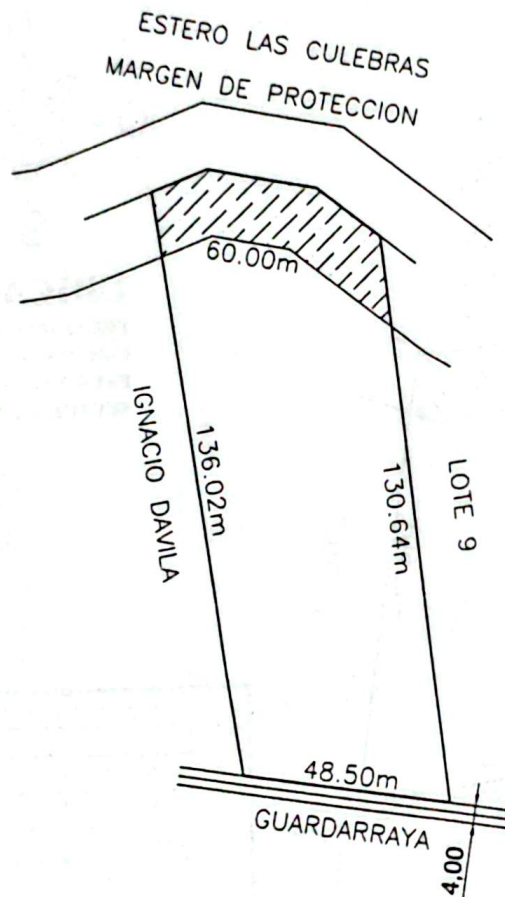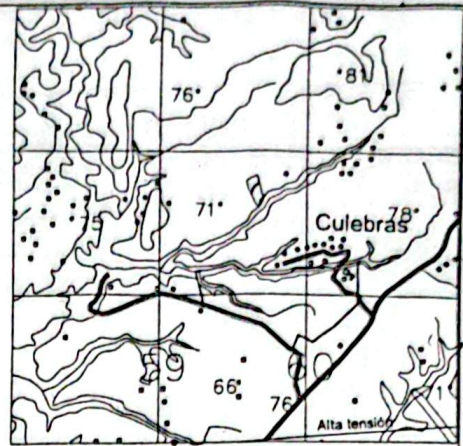

UBICACION

PROVINCIA --- GUAYAS
CANTON --- EL EMPALME
PARROQ. --- GUAYAS
SECTOR.....LAS CULEBRAS

CUADRO DE AREAS

AREA UTIL	5980.85m ²
Margen de protección	916.97m ²

V	COORDENADAS	
	Y	X
?	9,884,204	659,470
?	9,884,209	659,483
?	9,884,205	659,509
?	9,884,194	659,525
?	9,884,064	659,545
?	9,884,070	659,497
?	9,884,204	659,470

Datos Tomados con GPS
Datum: WGS 84
Coordenadas UTM
Zona: 17 Sur

LEVANTAMIENTO PLANIMETRICO DEL TERRENO RURAL DE:

LOTE 8

Area:

5980.85m²
(0,5980Has)

Fecha:

FEBRERO/2017

Revisó y Aprueba:

Arq. Mercedes Herrera
ARQ. MERCEDES HERRERA
DIRECTOR DE ORDENAMIENTO TERRITORIAL

Levantamiento planimetrico:

CARLOS PINCAY
TECNICO DE PLANIFICACION

Dibuja:

Nery Mora Burgos
NERY MORA BURGOS
TECNICO DE PLANIFICACION

Escala:




1:4000





LINDEROS Y MEDIDAS

NORTE:	Con Estero Las Culebras en 52.67m. Siguiendo su curso.
SUR:	Con Lote 7 en 47.05m.
ESTE:	Con Victoria Davila Arreaga en 212.77m.
OESTE:	Con Lote 2 en 209.96m.

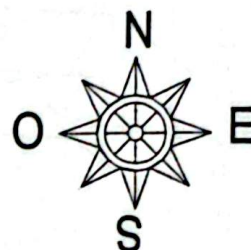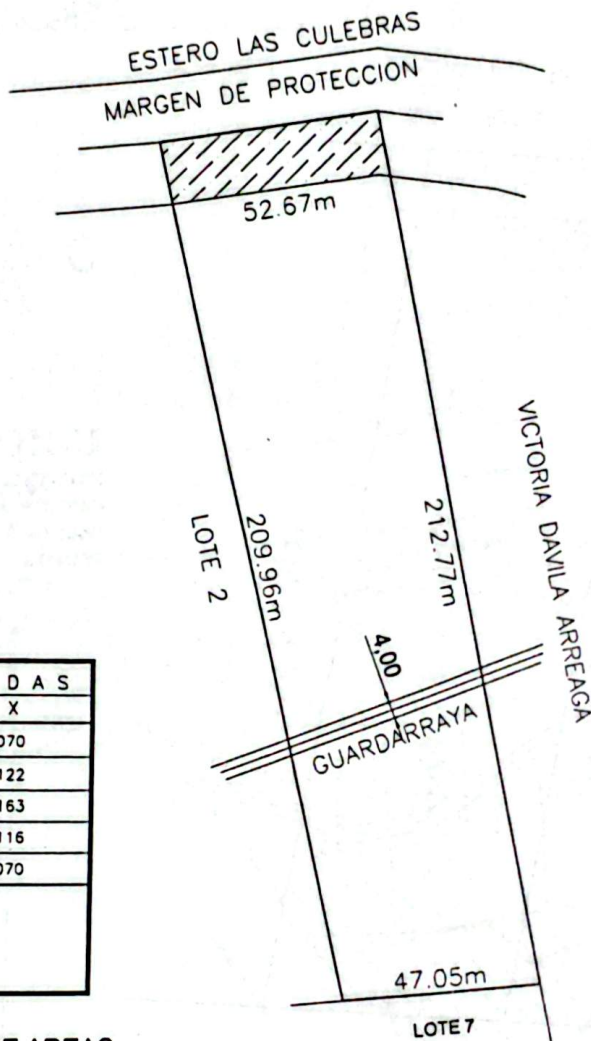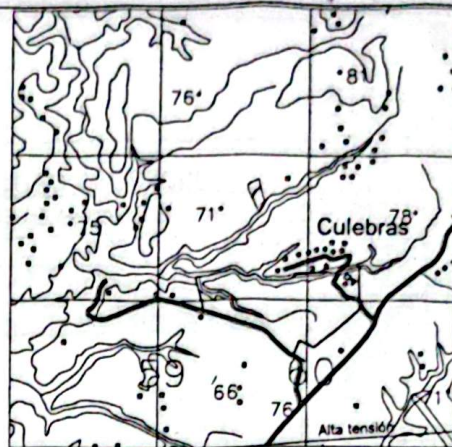

UBICACION


PROVINCIA --- GUAYAS
CANTON --- EL EMPALME
PARROQ. --- GUAYAS
SECTOR.....LAS CULEBRAS

V	COORDENADAS	
	Y	X
?	9,884,190	660,070
?	9,884,198	660,122
?	9,883,989	660,163
?	9,883,985	660,116
?	9,884,190	660,070

Datos Tomados con GPS
Datum: WGS 84
Coordenadas UTM
Zona: 17 Sur




CUADRO DE AREAS

AREA UTIL	9507.80m ²
Margen de protección	787.94m ²
AREA DE VIA	196.65m ²

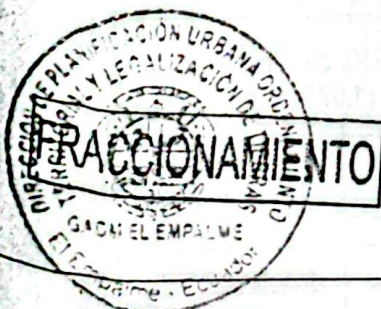

LEVANTAMIENTO PLANIMETRICO DEL TERRENO RURAL DE		Area	
LOTE 6		9507.80m ² (0,9507Has)	
Fecha:	Revisó y Aprobó	Levantamiento planimétrico	Dibujó
FEBRERO/2017	<i>Por Mercedes Herrera</i>		<i>[Signature]</i>
Escala:	ARQ. MERCEDES HERRERA DIRECTOR DE ORDENAMIENTO TERRITORIAL	CARLOS PINCAY TECNICO DE PLANIFICACION	NERY MORA BURGOS TECNICO DE PLANIFICACION
1:4000			

LINDEROS Y MEDIDAS	
NORTE:	Con Estero Las Culebras en 57.21m. Siguiendo su curso.
SUR:	Con Lote 7 en 57.25m.
ESTE:	Con Lote 2 en 209.45m.
OESTE:	Con Lote 1 en 208.93m.

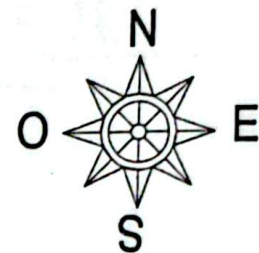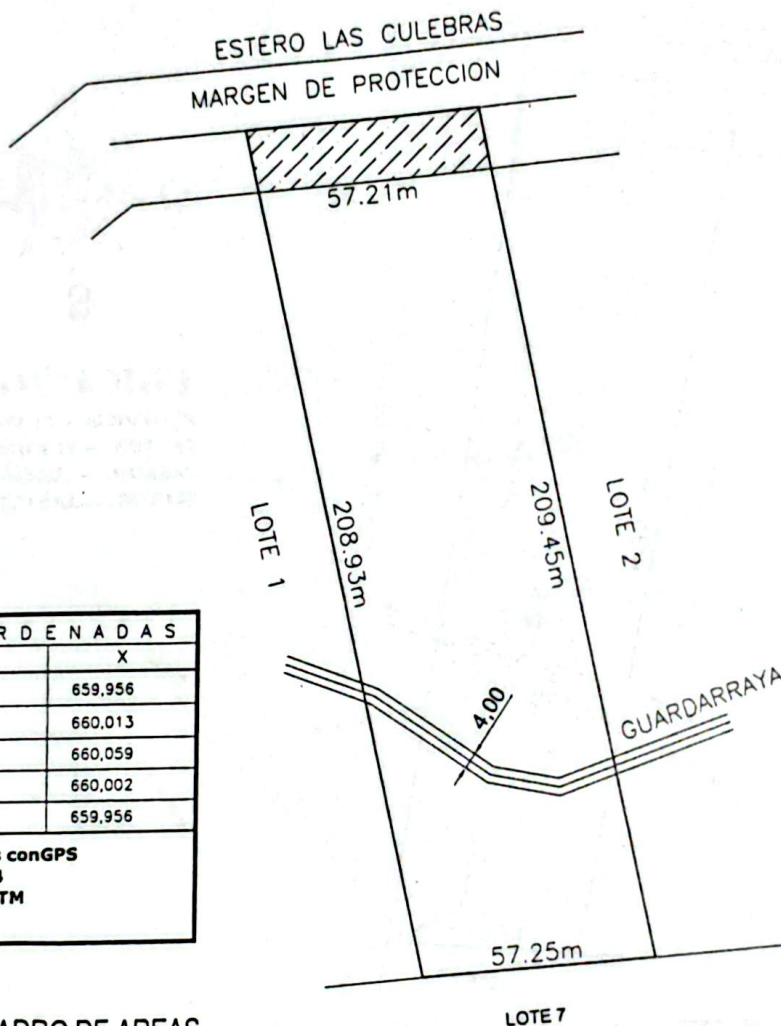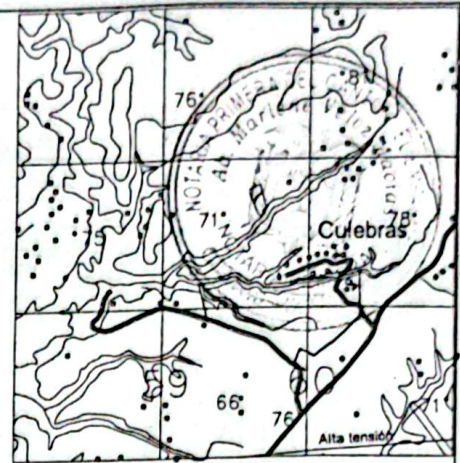

UBICACIÓN

PROVINCIA --- GUAYAS
 CANTÓN --- EL EMPALME
 PARROQUIA --- Santa Vilela Macías
 SECTOR --- LAS CULEBRAS
 NOTARÍA PRIMERA

V	COORDENADAS	
	Y	X
?	9,884,179	659,956
?	9,884,185	660,013
?	9,883,980	660,059
?	9,883,976	660,002
?	9,884,179	659,956

Datos Tomados conGPS
 Datum: WGS 84
 Coordenadas UTM
 Zona: 17 Sur




CUADRO DE AREAS

AREA UTIL	10736.22m2
Margen de protección	858.59m2
AREA DE VIA	276.81m2

	LEVANTAMIENTO PLANIMETRICO DEL TERRENO RURAL DE		Area	
	LOTE 5		10736.22m2 (1,0736Has)	
	Fecha:	Revisó y Aprobó:	Levantamiento planimétrico:	Dibujo:
	FEBRERO/2017	<i>Mercedes Herrera</i>		<i>Nery Mora Burgos</i>
Escala:	ARQ. MERCEDES HERRERA DIRECTOR DE ORDENAMIENTO TERRITORIAL	CARLOS PINCAY TECNICO DE PLANIFICACION	NERY MORA BURGOS TECNICO DE PLANIFICACION	
1:4000				

LINDEROS Y MEDIDAS	
NORTE	Con Estero Las Culebras en 1154.27 m Siguiendo su curso
SUR	Con Camino publico en 700.16m Siguiendo su trazado
ESTE	Con Hidros. Goya Sanchez en 296.56m S 00° 20'02" E, 224.96m S 43° 58'17" W, 128.35m S 54° 04'41" W; 54.15m S 48° 46'23" W, Tirso Coello Gutierrez en 31.78m N 54° 03'50" W, 76.16m N 67° 19'01" W, 109.70m S 21° 47'46" W.
OESTE	Con Tirso Coello Gutierrez en 23.35m N 09° 51'56" E, 145.85m N 22° 19'53" W, 70.90m N 03° 13'26" E

UBICACION
 PROVINCIA - GUAYAS
 CANTON - EL EMPALME
 PARROQ. - GUAYAS
 SECTOR - LAS CULEBRAS

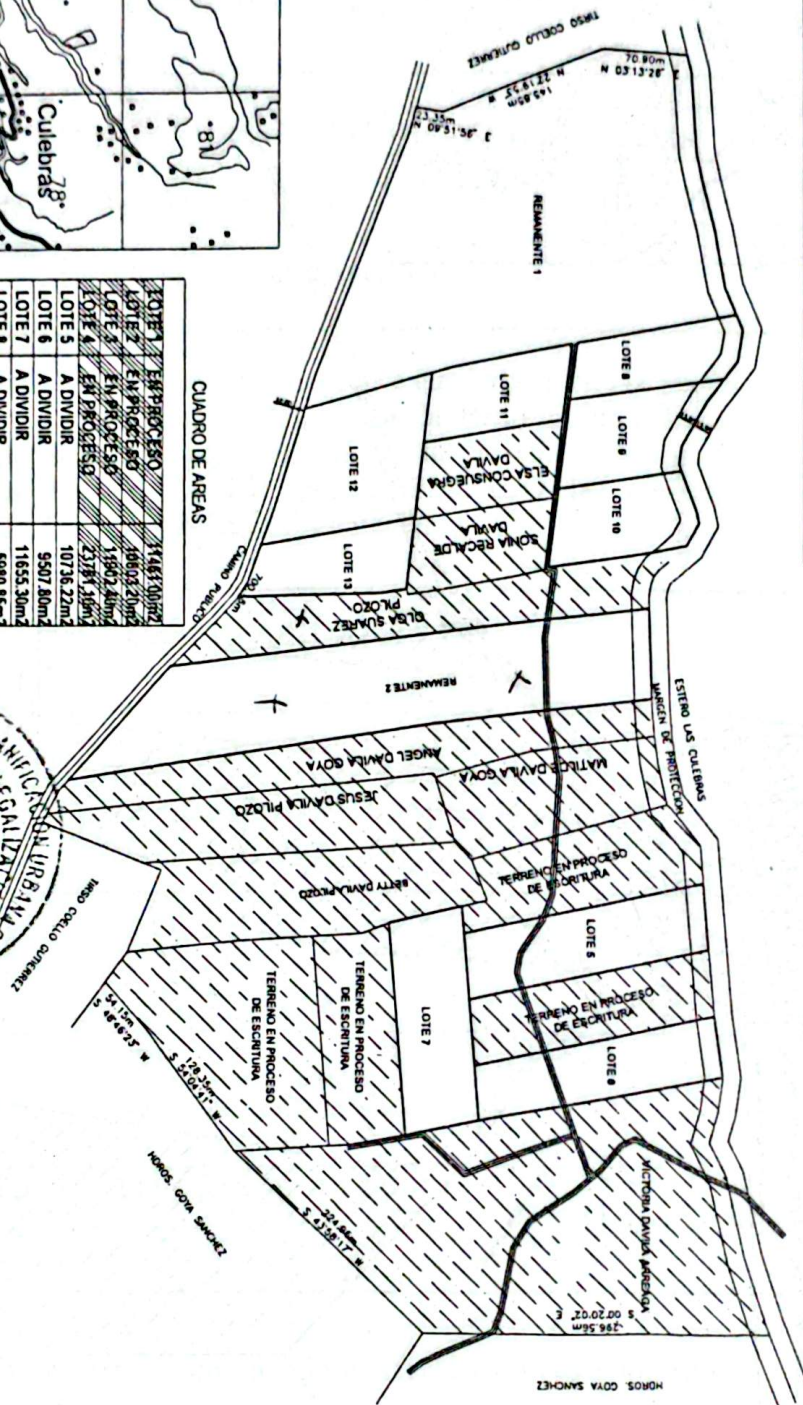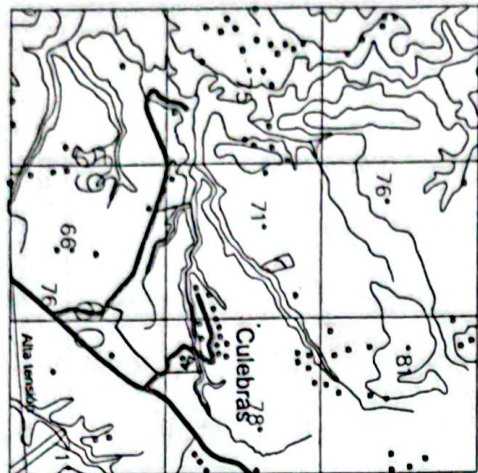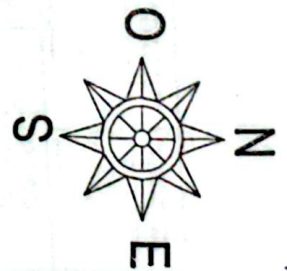

CUADRO DE AREAS

LOTE 1	EN PROCESO	11483.00m ²
LOTE 2	EN PROCESO	10603.20m ²
LOTE 3	EN PROCESO	15602.40m ²
LOTE 4	EN PROCESO	23785.10m ²
LOTE 5	A DIVIDIR	10736.22m ²
LOTE 6	A DIVIDIR	9507.80m ²
LOTE 7	A DIVIDIR	11655.30m ²
LOTE 8	A DIVIDIR	5980.85m ²
LOTE 9	A DIVIDIR	6816.93m ²
LOTE 10	A DIVIDIR	6482.10m ²
LOTE 11	A DIVIDIR	7208.74m ²
LOTE 12	A DIVIDIR	13638.45m ²
LOTE 13	A DIVIDIR	7113.69m ²
REMANENTE 1		65520.88m ²
REMANENTE 2		34491.10m ²
AREA DE VIAS		2021.61m ²
Margen de proteccion		11844.59m ²
TOTAL		250972.14m ²

COORDENADAS	1	2	3	4	5	6	7	8	9	10	11	12	13	14	15	16	17	18	19	20	21	22	23	24	25	26	27	28	29	30	31	32	33	34	35	36	37	38	39	40	41	42	43	44	45	46	47	48	49	50	51	52	53	54	55	56	57	58	59	60	61	62	63	64	65	66	67	68	69	70	71	72	73	74	75	76	77	78	79	80	81	82	83	84	85	86	87	88	89	90	91	92	93	94	95	96	97	98	99	100	
N	9.864.163	659.750	9.864.164	659.751	9.864.165	659.752	9.864.166	659.753	9.864.167	659.754	9.864.168	659.755	9.864.169	659.756	9.864.170	659.757	9.864.171	659.758	9.864.172	659.759	9.864.173	659.760	9.864.174	659.761	9.864.175	659.762	9.864.176	659.763	9.864.177	659.764	9.864.178	659.765	9.864.179	659.766	9.864.180	659.767	9.864.181	659.768	9.864.182	659.769	9.864.183	659.770	9.864.184	659.771	9.864.185	659.772	9.864.186	659.773	9.864.187	659.774	9.864.188	659.775	9.864.189	659.776	9.864.190	659.777	9.864.191	659.778	9.864.192	659.779	9.864.193	659.780	9.864.194	659.781	9.864.195	659.782	9.864.196	659.783	9.864.197	659.784	9.864.198	659.785	9.864.199	659.786	9.864.200	659.787	9.864.201	659.788	9.864.202	659.789	9.864.203	659.790	9.864.204	659.791	9.864.205	659.792	9.864.206	659.793	9.864.207	659.794	9.864.208	659.795	9.864.209	659.796	9.864.210	659.797	9.864.211	659.798	9.864.212	659.799	9.864.213	659.800	9.864.214	659.801	9.864.215	659.802	9.864.216	659.803	9.864.217	659.804	9.864.218	659.805	9.864.219	659.806	9.864.220	659.807	9.864.221	659.808	9.864.222	659.809	9.864.223	659.810	9.864.224	659.811	9.864.225	659.812	9.864.226	659.813	9.864.227	659.814	9.864.228	659.815	9.864.229	659.816	9.864.230	659.817	9.864.231	659.818	9.864.232	659.819	9.864.233	659.820	9.864.234	659.821	9.864.235	659.822	9.864.236	659.823	9.864.237	659.824	9.864.238	659.825	9.864.239	659.826	9.864.237	659.827	9.864.238	659.828	9.864.239	659.829	9.864.240	659.830	9.864.241	659.831	9.864.242	659.832	9.864.243	659.833	9.864.244	659.834	9.864.245	659.835	9.864.246	659.836	9.864.247	659.837	9.864.248	659.838	9.864.249	659.839	9.864.250	659.840	9.864.251	659.841	9.864.252	659.842	9.864.253	659.843	9.864.254	659.844	9.864.255	659.845	9.864.256	659.846	9.864.257	659.847	9.864.258	659.848	9.864.259	659.849	9.864.260	659.850	9.864.261	659.851	9.864.262	659.852	9.864.263	659.853	9.864.264	659.854	9.864.265	659.855	9.864.266	659.856	9.864.267	659.857	9.864.268	659.858	9.864.269	659.859	9.864.270	659.860	9.864.271	659.861	9.864.272	659.862	9.864.273	659.863	9.864.274	659.864	9.864.275	659.865	9.864.276	659.866	9.864.277	659.867	9.864.278	659.868	9.864.279	659.869	9.864.280	659.870	9.864.281	659.871	9.864.282	659.872	9.864.283	659.873	9.864.284	659.874	9.864.285	659.875	9.864.286	659.876	9.864.287	659.877	9.864.288	659.878	9.864.289	659.879	9.864.290	659.880	9.864.291	659.881	9.864.292	659.882	9.864.293	659.883	9.864.294	659.884	9.864.295	659.885	9.864.296	659.886	9.864.297	659.887	9.864.298	659.888	9.864.299	659.889	9.864.300	659.890	9.864.301	659.891	9.864.302	659.892	9.864.303	659.893	9.864.304	659.894	9.864.305	659.895	9.864.306	659.896	9.864.307	659.897	9.864.308	659.898	9.864.309	659.899	9.864.310	659.900	9.864.311	659.901	9.864.312	659.902	9.864.313	659.903	9.864.314	659.904	9.864.315	659.905	9.864.316	659.906	9.864.317	659.907	9.864.318	659.908	9.864.319	659.909	9.864.320	659.910	9.864.321	659.911	9.864.322	659.912	9.864.323	659.913	9.864.324	659.914	9.864.325	659.915	9.864.326	659.916	9.864.327	659.917	9.86

Distancia (km) 539,350

Coordenadas UTM

Latitud 9.862333333333333

Longitud 659.75

UBICACION
PROVINCIA — GUAYAS
CANTON — EL EMPALME
PARROQ. — GUAYAS
SECTOR — LAS CUEBRAS

UBICACION
PROVINCIA — GUAYAS
CANTON — EL EMPALME
PARROQ. — GUAYAS
SECTOR — LAS CUEBRAS

UBICACION
PROVINCIA — GUAYAS
CANTON — EL EMPALME
PARROQ. — GUAYAS
SECTOR — LAS CUEBRAS

