
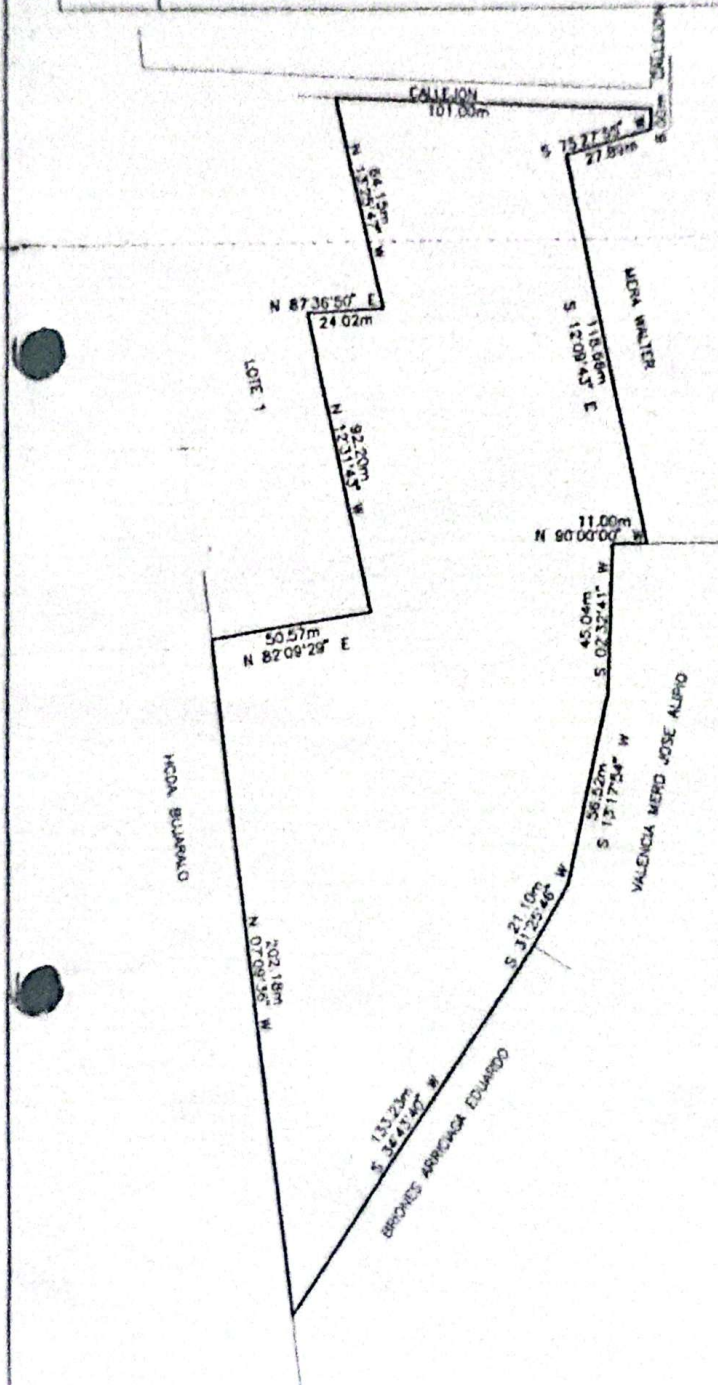


LINDEROS Y MEDIDAS ACTUALES

NORTE: Con Callejon en 101.00m.
ESTE: Con Vértice formado por linderos Este - Oeste
 Con Callejon en 6.00m, Mera Walter en 27.89m. S 75° 27' 55" W,
 118.66m S 12° 09' 43" E, Valencia Mero Jose Alpio en 11.00m.
 N 90° 00' 00" W, 45.04m S 02° 32' 41" W, 56.52m S 13° 17' 54" W,
 21.10m S 31° 25' 46" W, Briones Arriaga Eduardo en 133.23m.
 S 34° 43' 40" W.
OESTE: Con Hoda. Bujaralo en 202.18m N 07° 09' 36" W, Lote 1 en 50.57m.
 N 82° 09' 29" E, 92.20m N 12° 31' 43" W, 24.02m N 87° 36' 50" E,
 64.15m N 13° 25' 47" W.

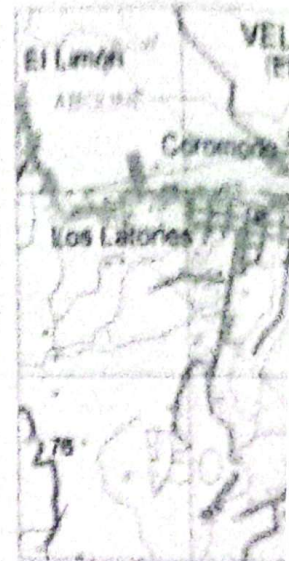



?	9,883,703.40
?	9,883,699.00
?	9,883,693.00
?	9,883,686.00
?	9,883,570.00
?	9,883,570.00
?	9,883,525.00
?	9,883,470.00
?	9,883,452.00
?	9,883,342.50
?	9,883,543.10
?	9,883,550.00
?	9,883,640.00
?	9,883,641.00
?	9,883,703.40

NOMBRE

ESPINOZA ALAVA PLACIDO BERCELIO
 RFMANFENTE

LINDEROS Y MEDIDAS ACTUALES

NORTE:	Con Callejon en 101.00m.
SUR:	Con Vertice formado por linderos Este - Oeste
ESTE:	Con Callejon en 6.00m; Mera Walter en 27.89m. S 75°27'55" W; 118.66m. S 12°09'43" E; Valencia Mero Jose Alpio en 11.00m. N 90°00'00" W; 45.04m. S 02°32'41" W; 56.52m. S 13°17'54" W; 21.10m. S 31°25'46" W; Briones Arriaga Eduardo en 133.23m. S 34°43'40" W.
OESTE:	Con Hcda. Bujaralo en 202.18m. N 07°09'36" W; Lote 1 en 50.57m. N 82°09'29" E; 92.20m. N 12°31'43" W; 24.02m. N 87°36'50" E; 64.15m. N 13°25'47" W.

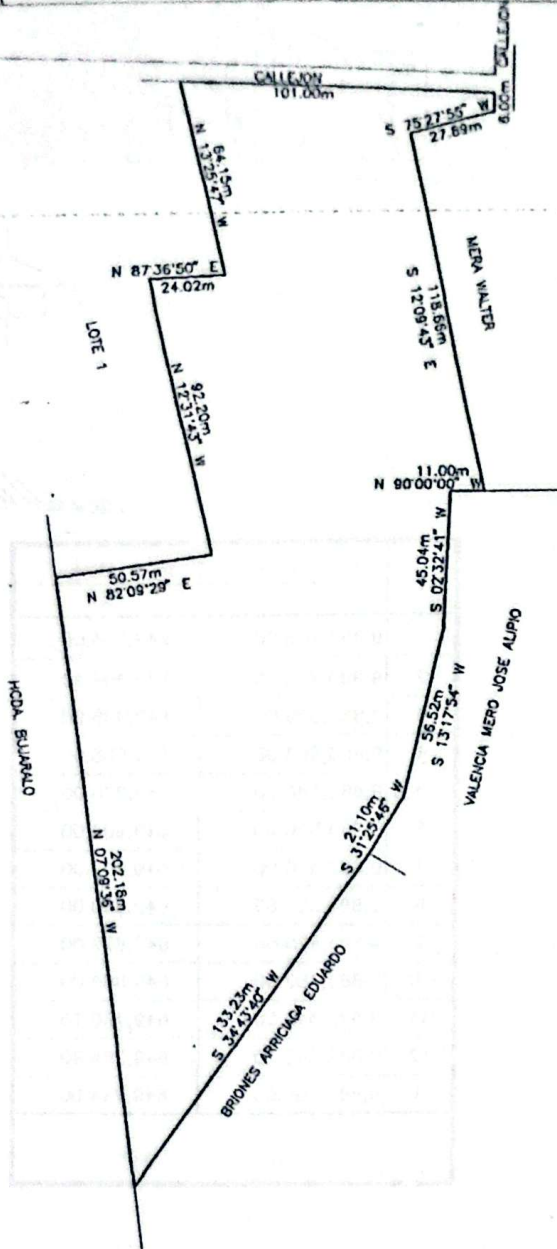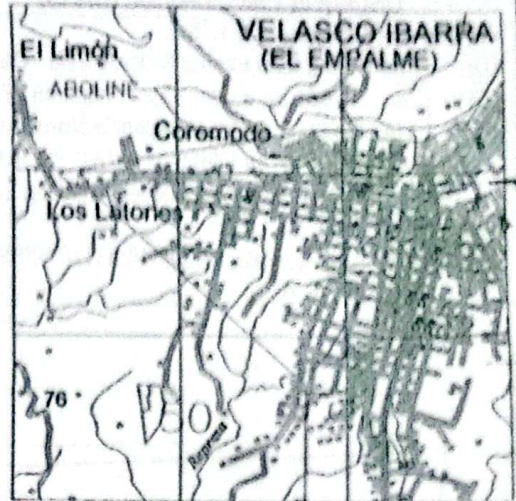

	Y	X
?	9,883,703.40	649,804.10
?	9,883,699.00	649,905.00
?	9,883,693.00	649,905.00
?	9,883,686.00	649,878.00
?	9,883,570.00	649,903.00
?	9,883,570.00	649,892.00
?	9,883,525.00	649,890.00
?	9,883,470.00	649,877.00
?	9,883,452.00	649,866.00
?	9,883,342.50	649,790.10
?	9,883,543.10	649,764.90
?	9,883,550.00	649,815.00
?	9,883,640.00	649,795.00
?	9,883,641.00	649,819.00
?	9,883,703.40	649,804.10

NOMBRE:



**ESPINOZA ALAVA PLACIDO BERCELIO
REMANENTE**

Provincia: GUAYAS	Cantón: EL EMPALME	Parroquia: VELASCO IBARRA	Sector: SAN MIGUEL DE ADENTRO	Propietario:
Fecha: ENERO / 2021	Escala: 1:3000	Superficie: 28459.60m2	Levantó y Dibujó: 	

ING. WILLIAM PACHECO BARRERA
REG. SENECT. 1006-02-29410

LINDEROS Y MEDIDAS ACTUALES

NORTE:	Con Callejon en 161.15m.
SUR:	Con Vertice formado por linderos Este - Oeste
ESTE:	Con Callejon en 6.00m; Mera Walter en 27.89m. S 75°27'55" W; 118.66m. S 12°09'43" E; Valencia Mero Jose Alipio en 11.00m. N 90°00'00" W; 45.04m. S 02°32'41" W; 56.52m. S 13°17'54" W; 21.10m. S 31°25'46" W; Briones Arriaga Eduardo en 133.23m. S 34°43'40" W.
OESTE:	Con Hoda. Bujaralo en 202.18m. N 07°09'36" W; 164.24m. N 07°18'39" W.

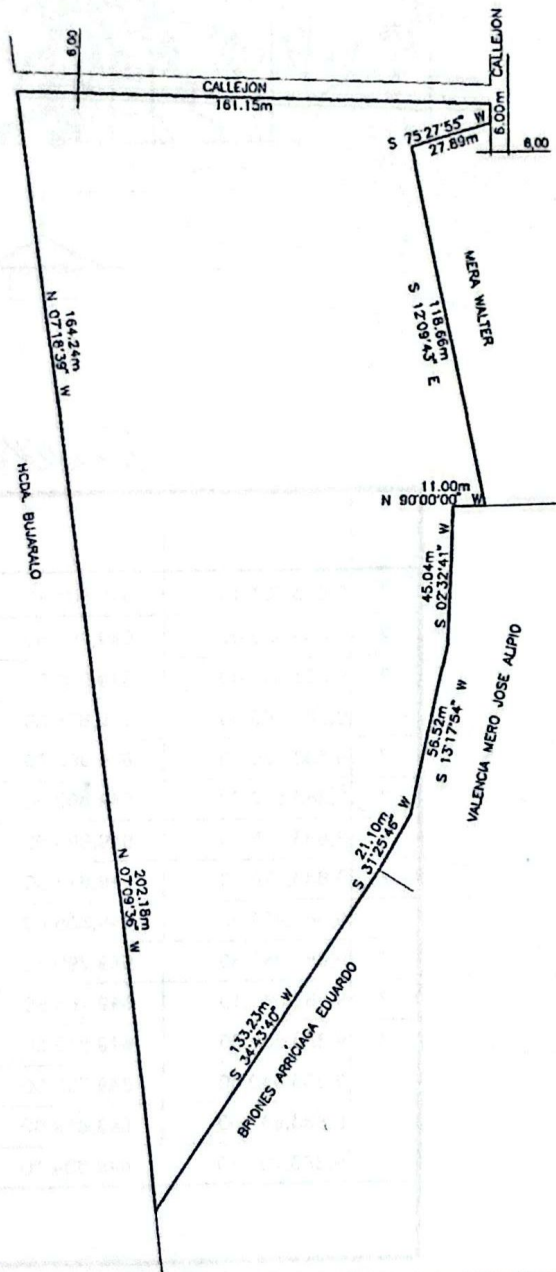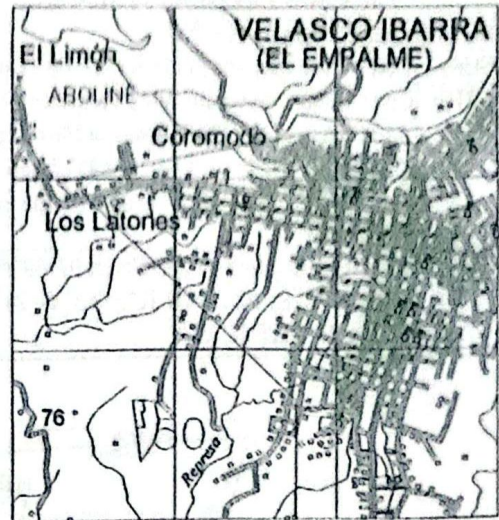

V	COORDENADAS	
	Y	X
1	9,883,706.00	649,744.00
2	9,883,703.40	649,804.10
3	9,883,699.00	649,905.00
4	9,883,693.00	649,905.00
5	9,883,686.00	649,878.00
6	9,883,570.00	649,903.00
7	9,883,570.00	649,892.00
8	9,883,525.00	649,890.00
9	9,883,470.00	649,877.00
10	9,883,452.00	649,866.00
11	9,883,342.50	649,790.10
12	9,883,543.10	649,764.90
1	9,883,706.00	649,744.00

NOMBRE:

ESPINOZA ALAVA PLACIDO BERCELIO

Provincia: GUAYAS	Cantón: EL EMPALME	Parroquia: VELASCO IBARRA	Sector: SAN MIGUEL DE ADENTRO	Propietario:
Fecha: ENERO / 2021	Escala: 1:3000	Superficie: 36920.60m2	Levantó y Dibujó: ING. WILLIAM PACHECO BARRERA REG. SENEYT. 1006 02 29410	