
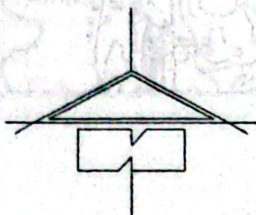


LINDEROS Y MEDIDAS ACTUALES

NORTE	Con Guardarraya Publica en 62.22m siguiendo su trazado.
SUR:	Con Abdon Alcivar Ponce en 6.32m S 74°28'33" W.
ESTE:	Con Herederos de Manuel Intriago en 44.15m S 13°05'30" E; Lote 4 en 33.06m S 03°28'05" W; Herederos de Manuel Intriago en 38.05m S 03°00'46" W; Ernesto Cedeño en 169.00m. S 00°20'20" W.
OESTE:	Con Lote 6 en 275.53m N 12°23'43" W.

AREA 10433.81m2

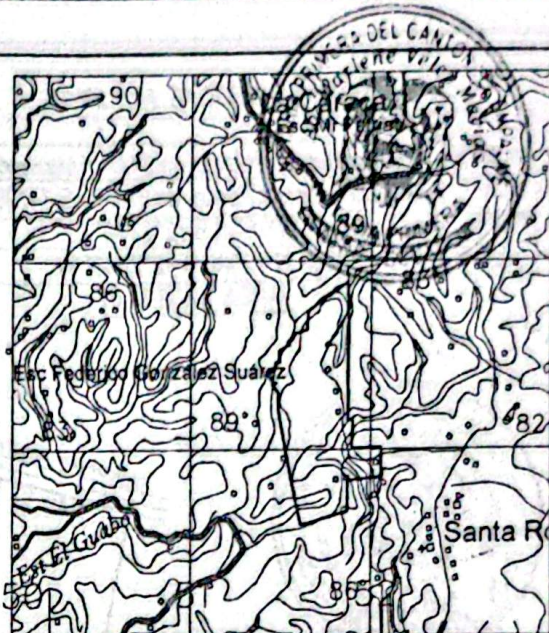

UBICACION

PROVINCIA --- GUAYAS
CANTON --- EL EMPALME
PARROQ. --- GUAYAS
SECTOR SANTA ROSA

987.138	987.138
987.138	987.138
LEVANTAMIENTO PLANIMETRICO
PARA DIVISION RURAL

Escala: 1:200

ABDON ALCIVAR PONCE

V	COORDENADA X	COORDENADA Y
?	9.889.934	651.865
?	9.889.950	651.865
?	9.889.907	651.875
?	9.889.874	651.873
?	9.889.836	651.871
?	9.889.667	651.870
?	9.889.665	651.864
?	9.889.934	651.805



LEVANTAMIENTO PLANIMETRICO DEL TERRENO DE:

LOTE 5

Area:

10433.81m2
(1,0433Has.)

Fecha:

FEBRERO/2018

Revisó y Aprobó:

ARG. MERCEDES HERRERA
DIRECTOR DE ORDENAMIENTO TERRITORIAL

Levantamiento planimetrico:

CARLOS PINCAT
TECNICO DE CAMPO

Dibujó:

MERY MORA BURGOS
TECNICO DE PLANIFICACION

Escala:

1:4000

LINDEROS Y MEDIDAS ACTUALES



NORTE:	Con Guardarraya Publica en 37.84m siguiendo su trazado.
SUR:	Con Abdon Alcivar Ponce en 37.87m. S 74°28'33" W.
ESTE:	Con Lote 5 en 275.57m. S 12°23'43" E.
OESTE:	Con Lote 7 en 276.28m. N 12°23'43" W.

AREA 10433.81m2



UBICACION

PROVINCIA --- GUAYAS
CANTON --- EL EMPALME
PARROQ. --- GUAYAS
SECTOR SANTA ROSA

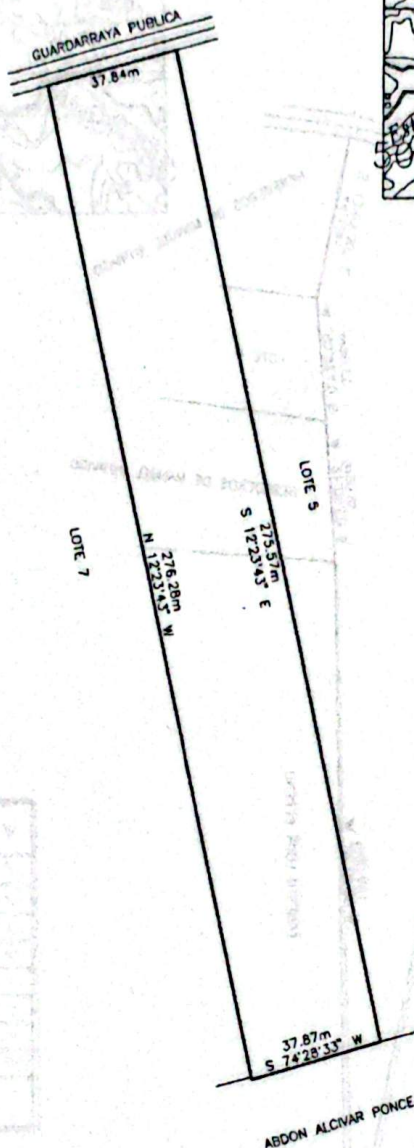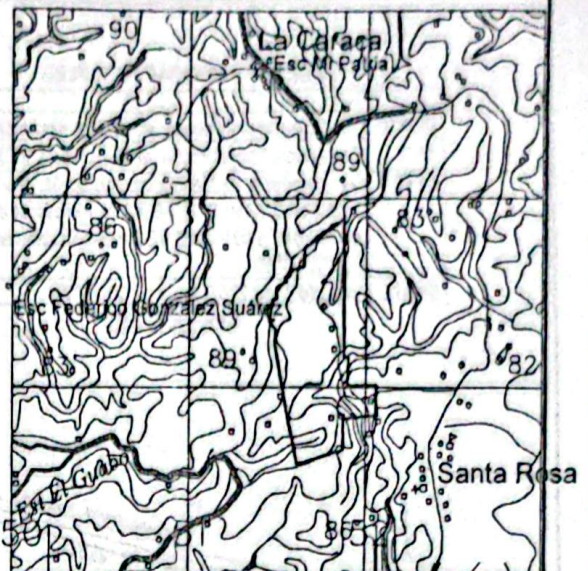

V	COORDENADAS	
	Y	X
?	9,889,925	651,768
?	9,889,934	651,805
?	9,889,665	651,864
?	9,889,655	651,827
?	9,889,925	651,768

LEVANTAMIENTO PLANIMETRICO
PARA DIVISION RURAL

Escala: 1:200



LEVANTAMIENTO PLANIMETRICO DEL TERRENO DE:

LOTE 6

Area:

10433.81m2
(1,0433Has.)

Fecha:

FEBRERO/2018

Revisó y Aprobó:

[Signature]
ARG. MERCEDES HERRERA
DIRECTORA DE MANEJO TERRITORIAL

Levantamiento planimetrico:

CARLOS PINCAY
TECNICO DE CAMPO

Dibujó:

[Signature]
NERY MORA BURGOS
TECNICO DE PLANIFICACION



Escala:

1:4000

LINDEROS Y MEDIDAS ACTUALES


NORTE:	Con Lote 1 en 169.86m.S 77°45'50" E; 72.06m.N 02°23'09" E; 264.91m.N 57°19'47" E.
SUR:	Con Lote 2 en 303.98m.S 56°40'33" W; 135.68m.N 70°37'48" W.
ESTE:	Con camino publico en 190.01m. siguiendo su trazado; Jose Ruiz en 59.08m.S 02°54'39" W; 28.16m.S 83°53'04" E.
OESTE:	Con Arturo Alcivar Ponce en 198.48m. N 10°44'37" W.

AREA 90470.50m2

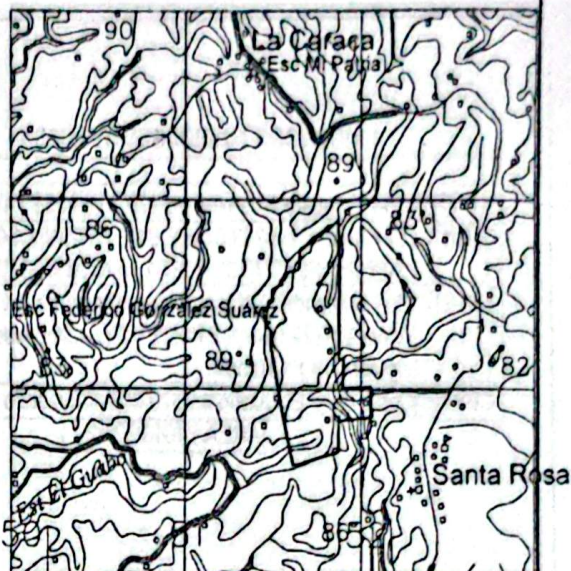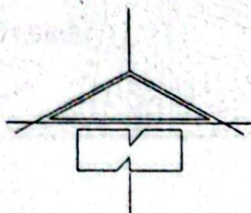

UBICACION

PROVINCIA --- GUAYAS
CANTON --- EL EMPALME
PARROQ. --- GUAYAS
SECTOR SANTA ROSA

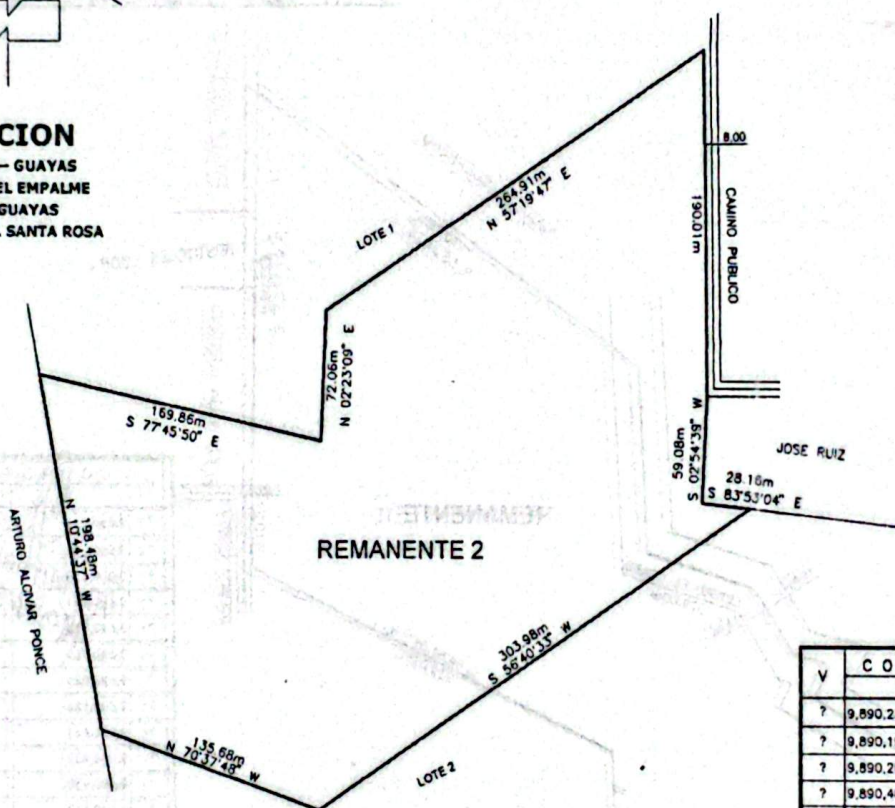

V	COORDENADAS	
	Y	X
?	9,890,230	651,481
?	9,890,194	651,647
?	9,890,268	651,530
?	9,890,409	651,873
?	9,890,219	651,875
?	9,890,180	651,872
?	9,890,157	651,900
?	9,889,990	651,646
?	9,890,035	651,518
?	9,890,230	651,481

LEVANTAMIENTO PLANIMETRICO
PARA DIVISION RURAL
Escala: 1:200



LEVANTAMIENTO PLANIMETRICO DEL TERRENO DE

REMANENTE 2

Area:



90470.50m2
(9,0470Has.)

Fecha:	Revisar y Aprobar	Levantamiento planimetrico	Obra:
FEBRERO/2018			
Escala:	ARQ. MERCEDES HERRERA DIRECTOR DE ORGANIZACION TERRITORIAL	CARLOS PINCAY TECNICO DE CAMPO	NERY MORA BURGOS TECNICO DE PLANIFICACION
1:4000			

LINDEROS Y MEDIDAS ACTUALES


NORTE:	Con Augusto Guerrero en 270.76m. N 55°04'38" E.
SUR:	Con Lote 1 en 233.07m. S 64°51'51" W, 94.05m. S 01°49'40" W, 90.09m. N 87°27'18" W, 84.15m. N 69°50'32" W.
ESTE:	Con Alejandro Macias, Temistocles Loo, y Carmelo Vera Alava en 222.08m. S 01°32'53" E; camino publico en 45.01m. siguiendo su trazado.
OESTE:	Con Estero El Guabo en 379.00m. Siguiendo su curso.

AREA 74048.32m²

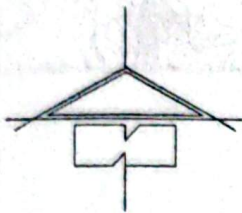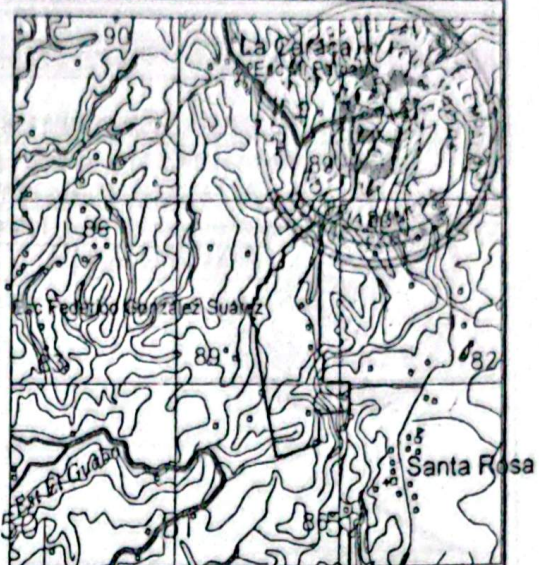

UBICACION

PROVINCIA --- GUAYAS
CANTON --- EL EMPALME
PARROQ. --- GUAYAS
SECTOR SANTA ROSA

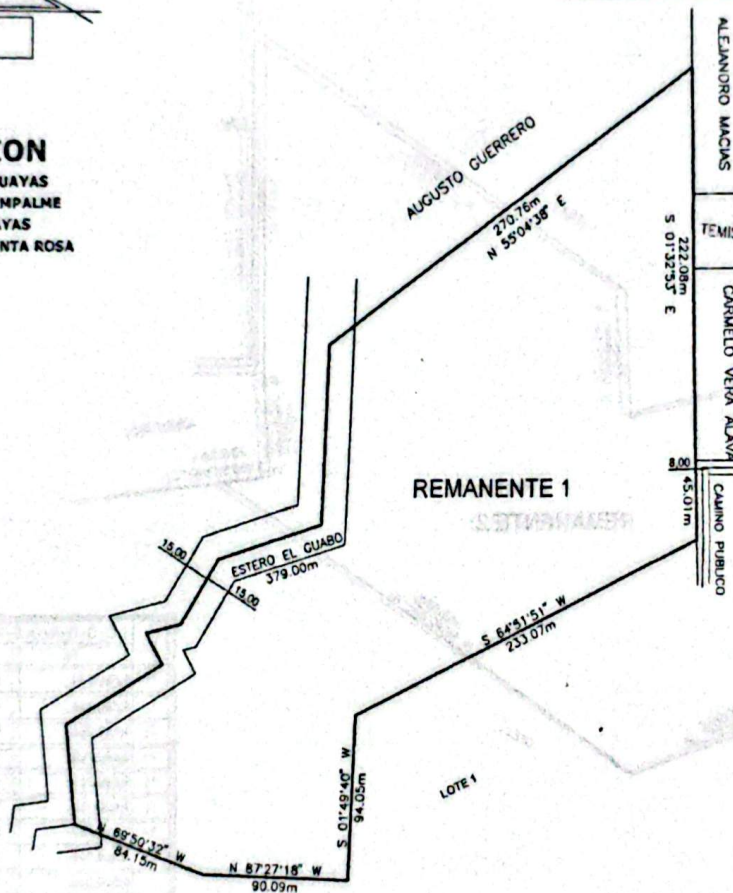

V	COORDENADAS	
?	9,890,747	851,802
?	9,890,894	851,870
?	9,890,810	851,892
?	9,890,811	851,872
?	9,890,811	851,873
?	9,890,869	851,876
?	9,890,624	851,877
?	9,890,525	851,886
?	9,890,431	851,863
?	9,890,435	851,573
?	9,890,458	851,510
?	9,890,513	851,504
?	9,890,549	851,567
?	9,890,583	851,560
?	9,890,565	851,567
?	9,890,602	851,591
?	9,890,623	851,659
?	9,890,735	851,663
?	9,890,747	851,663

LEVANTAMIENTO PLANIMETRICO
PARA DIVISION RURAL
Escala: 1:200



LEVANTAMIENTO PLANIMETRICO DEL TERRENO DE:

REMANENTE 1

Area:

74048.32m²
(7,4048Has.)

Fecha: FEBRERO/2018	Revis y Apruebo <i>[Signature]</i>	Levantamiento planimetrico CARLOS PINCAY TECNICO DE CAMPO	Dibujo <i>[Signature]</i> NERY MORA BURGOS TECNICO DE PLANIFICACION
Escala: 1:4000	ARG. MERCEDES HERRERA DIRECTOR DE ORDENAMIENTO TERRITORIAL		