



LINDEROS Y MEDIDAS ACTUALES

NORTE	Con Hdros. Bonilla en 73.50m. N 82°29'38" E; 111.60m. S 89°50'02" E; 48.00m. S 87°36'50" E; 36.00m. S 88°24'31" E; Luis Viteri en 28.50m. N 84°40'31" E; 41.10m. S 66°07'17" E.
SUR	Con Odilia Alvarez y Hernando Alvarez en 197.20m. N 74°08'00" W; Colon Alvarez en 154.60m. N 62°37'35" W; Elvia Alvarez en 88.00m. N 81°30'05" W.
ESTE	Con Armando Rivera en 32.00m. S 38°39'35" W; 53.30m. S 30°24'39" E; 37.30m. S 20°22'35" W; 32.30m. S 16°11'21" E; 26.10m. S 04°23'55" W; 43.50m. S 23°01'31" E; 52.60m. S 14°18'01" E; 31.30m. S 07°21'08" E; 38.40m. S 38°39'35" E; 26.90m. S 38°39'35" E; 34.10m. S 31°49'38" E; 19.70m. S 43°01'30" E; 116.00m. S 35°52'55" E.
OESTE	Con Wilson Zambrano en 86.30m. N 10°00'28" W; Ramon Candelario y camino de acceso en 87.10m. N 12°36'00" W; Antonio Pincay en 80.30m. N 18°53'09" W; Jessica Mendieta en 43.70m. N 10°32'21" W; Jorge Mendieta en 62.50m. N 17°12'52" W.

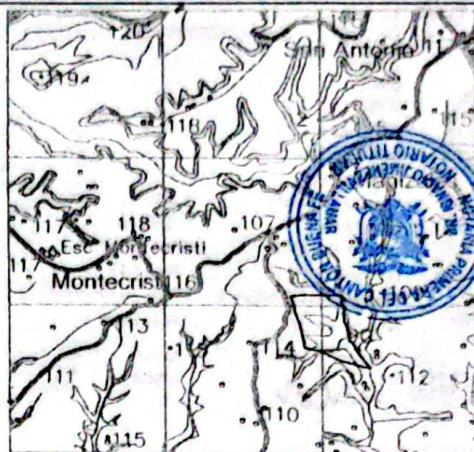

HDROS. BONILLA

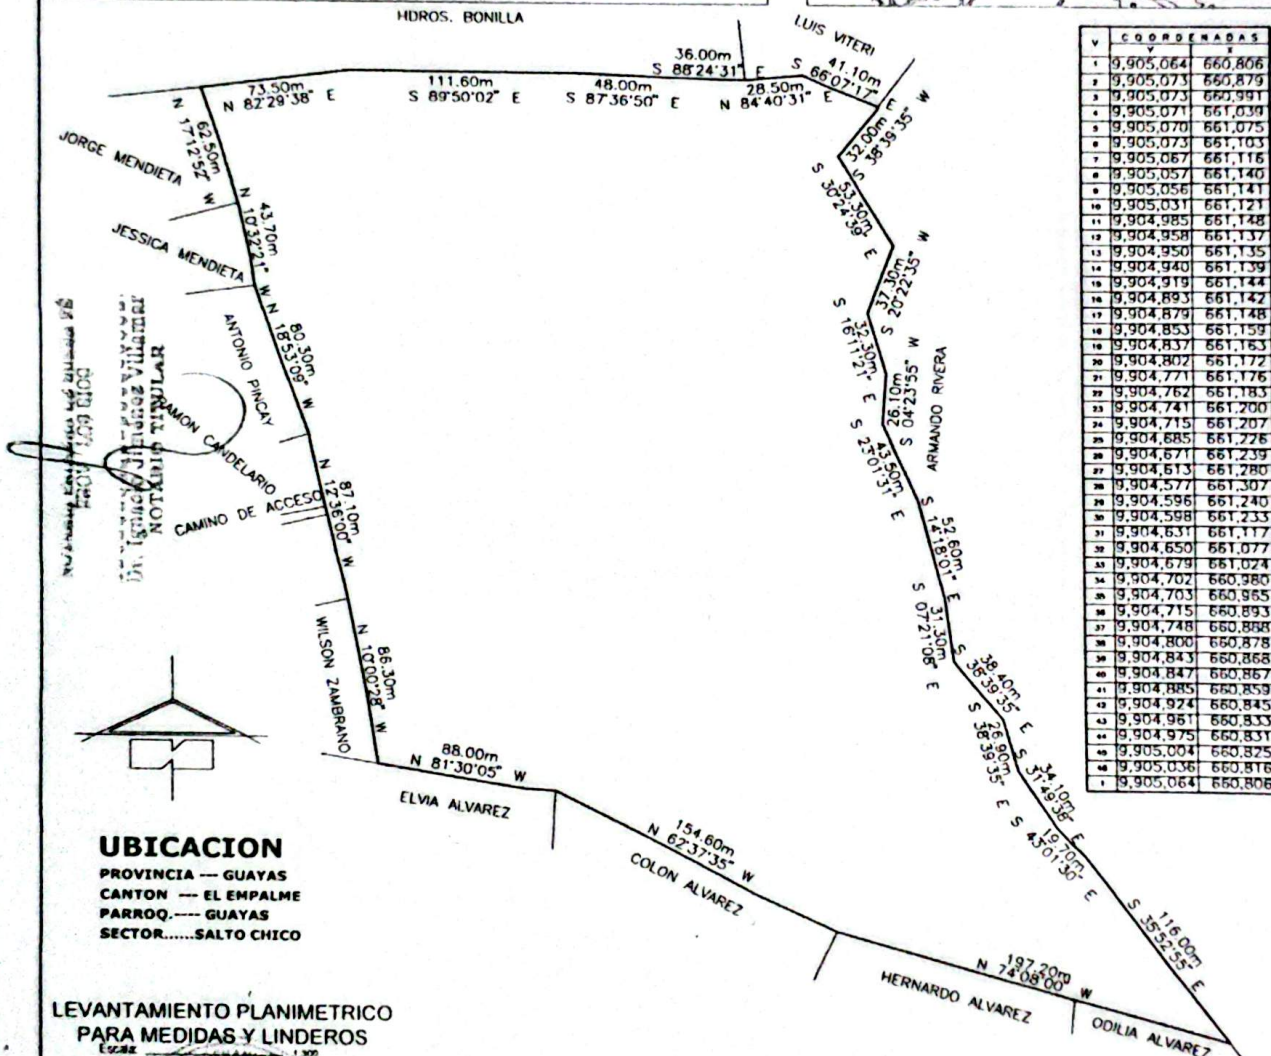

V	COORDENADAS
1	9.905.064 660.806
2	9.905.073 660.879
3	9.905.073 661.991
4	9.905.071 661.039
5	9.905.070 661.075
6	9.905.073 661.103
7	9.905.067 661.116
8	9.905.057 661.140
9	9.905.056 661.141
10	9.905.031 661.121
11	9.904.985 661.148
12	9.904.958 661.137
13	9.904.950 661.135
14	9.904.940 661.139
15	9.904.919 661.144
16	9.904.893 661.142
17	9.904.879 661.148
18	9.904.853 661.159
19	9.904.837 661.163
20	9.904.802 661.172
21	9.904.771 661.176
22	9.904.762 661.183
23	9.904.741 661.200
24	9.904.715 661.207
25	9.904.685 661.226
26	9.904.671 661.239
27	9.904.613 661.280
28	9.904.577 661.307
29	9.904.596 661.240
30	9.904.598 661.233
31	9.904.631 661.117
32	9.904.650 661.077
33	9.904.679 661.024
34	9.904.702 660.980
35	9.904.703 660.965
36	9.904.715 660.893
37	9.904.748 660.898
38	9.904.800 660.878
39	9.904.843 660.868
40	9.904.847 660.867
41	9.904.885 660.859
42	9.904.924 660.845
43	9.904.961 660.833
44	9.904.975 660.831
45	9.905.004 660.825
46	9.905.036 660.816
47	9.905.064 660.806

UBICACION

PROVINCIA — GUAYAS
CANTON — EL EMPALME
PARROQ. — GUAYAS
SECTOR.....SALTO CHICO

LEVANTAMIENTO PLANIMETRICO
PARA MEDIDAS Y LINDEROS



LEVANTAMIENTO PLANIMETRICO
CALDERON MONTENEGRO JOVITA ARCENIA

Area
13,000 Has.

Fecha
MAYO/2025

Revisó y Aprobó

Levantamiento Planimetrico

Dibujó

Escala
1:300

ARQ. MELANY VELEZ L.
JEFE DE URBANISMO Y CONSTRUCCION

NERY MORA BURGOS
DIBUJANTE

NERY MORA BURGOS
DIBUJANTE