
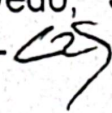


49671 - C


ABOGADO JULIO CESAR YEPEZ ESPINOZA, REGISTRADOR DE LA PROPIEDAD DEL CANTON BUENA FÉ, ENCARGADO DEL REGISTRO DE LA PROPIEDAD DEL CANTON QUEVEDO, PROVINCIA DE LOS RIOS, CERTIFICA: Que, con el No.775 del Registro de Propiedades y anotado al Nr.1925 del Libro Repertorio, el 14 de Mayo del 2007, consta inscrita la Protocolización de la Providencia de Adjudicación dictada por el Instituto Nacional de Desarrollo Agrario INDA, el 29 de Marzo del 2007, Protocolizada en la Notaria Tercera de Quevedo, a cargo del Abogado Abel Germán León León, el 27 de Abril del 2007, por la cual se **ADJUDICA** a favor de la señora **MORAN AROCA GLORIA PILAR** la superficie de CINCO HECTAREAS, CUARENTA Y SEIS AREAS de terreno, ubicado en la Parroquia y Cantón Quevedo, Sector Pro maiz de la Provincia de Los Ríos, el mismo que queda circunscrito dentro de los siguientes linderos y medidas: NORTE, con línea petrolera en 108,41m R.S. 80 - 44 - 771 E, y 174,27m. R.S. 80 - 44 - 771E: SUR, con lote de la escuela Walter Andrade en 126,44m. R.N. 76 - 26 - 27W, y en 70, 61m.R.N. 36 - 16 - 13E, con vía Empalme Quevedo, en 91,61m., R.N. 79 - 245 - 37 W, y con una Vía Pública de 59,93m. R.S. 64 - 17 - 24 - 17 W; ESTE, lote de Italo Triviño Arteaga en 200,26m., R.S. 8 - 36 - 56 - 33W; y, OESTE, con el lote de Compañía Tabacalera en 164,24m., R.N. 4 - 30 - 50 - 36W.- Certifico además, que el lote descrito se encuentra libre de Hipotecas, Prohibiciones Judiciales de Enajenar y Embargo.- Quevedo, Septiembre 29 del año 2008.- Revisado por: Clara Sevillano.- 

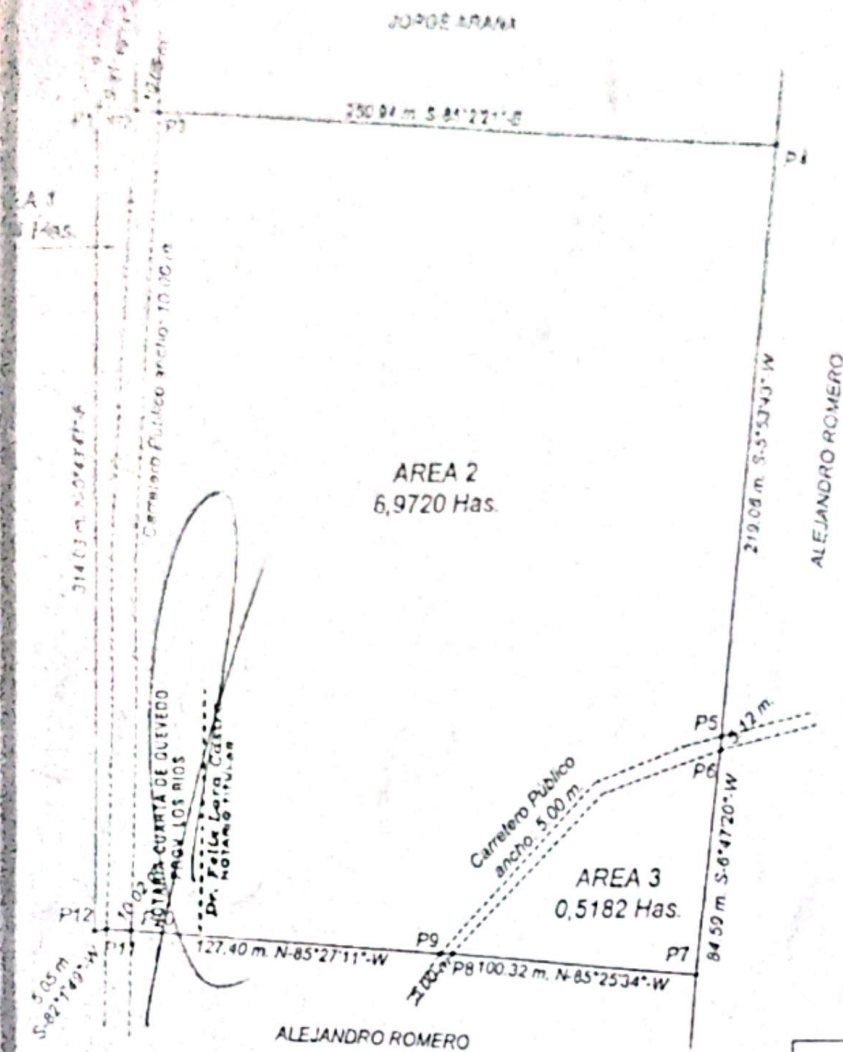

COORDENADAS		
Vertice	X(m)	Y(m)
P1	557432	9878571
P2	558448	9878668
P3	557454	9878667
P4	557708	9878648
P5	557885	9878428
P6	557685	9878423
P7	557575	9878319
P8	557575	9878347
P9	557570	9878347
P10	557443	9878357
P11	557433	9878357
P12	557429	9878357

Datos tomados con GPS
Datum: WGS-84
Proyección Cartográfica: UTM
Zona: 17 Sur

UBICACION

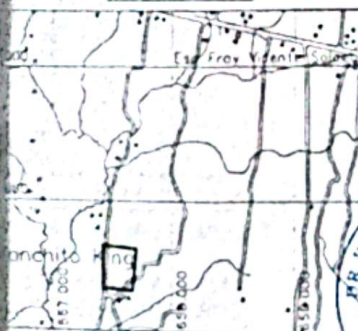

CARTA TOPOGRAFICA VELASCO IBARRA
CODIGO NIV-A2

José Federico Bravo B.
INGENIERO CIV
Reg. Prof. 094253

AREA 1: 0,2774 Has
AREA 2: 6,9720 Has.
AREA 3: 0,5182 Has.
AREA TOTAL: 7,7676 Has.


LINDEROS Y MEDIDAS

NORTE: JORGE ARANA en 16 16 m. S-81°49'11"-E. ANCHO DE CARRETERO en 10.05 m. JORGE ARANA en 250 94 m. S-85°2'21"-E.
SUR: ALEJANDRO ROMERO en 100.32 m. N-85°25'34"-W. ANCHO DE CARRETERO en 5.00 m. ALEJANDRO ROMERO en 127.40 m. N-85°27'11"-W. ANCHO DE CARRETERO en 10.02 m. ALEJANDRO ROMERO en 5.05 m. S-82°1'49"-W.
ESTE: ALEJANDRO ROMERO en 219.06 m. S-5°53'43"-W. ANCHO DE CARRETERO en 5.12 m. ALEJANDRO ROMERO en 84.59 m. S-6°47'20"-W.
OESTE: PRIMITIVO ROMERO en 314.03 m. N-0°43'47"-E.


NTAMIENTO PLANIMETRICO

GLORIA PILAR MORAN AROCA

Cantón	Parroquia	Sector
MOCACHE	MOCACHE	HUANCABILCA
Superficie	Levanto y Dibujo:	Reviso y Aprobó:
7,7676 Has.	José Federico Bravo B. INGENIERO CIV Reg. Prof. 094253	

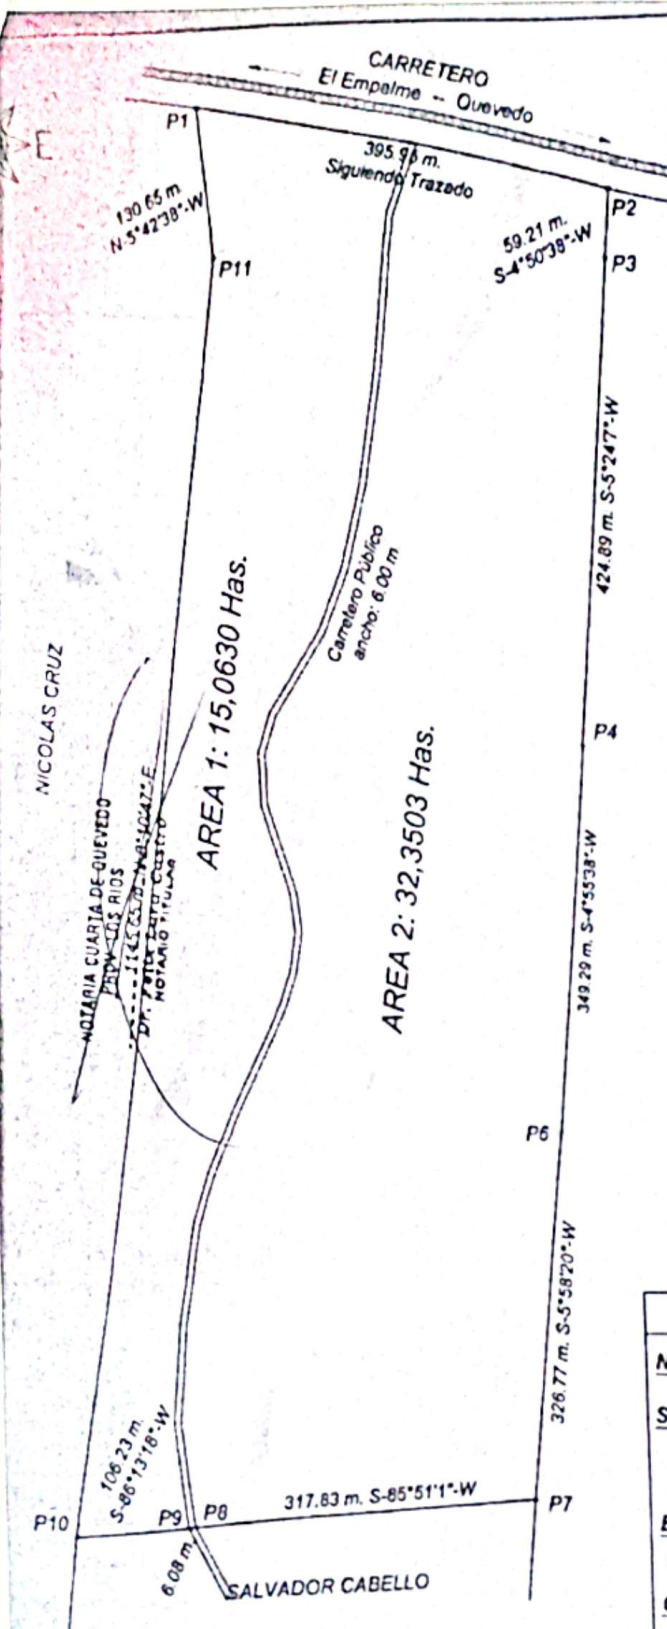

UBICACION

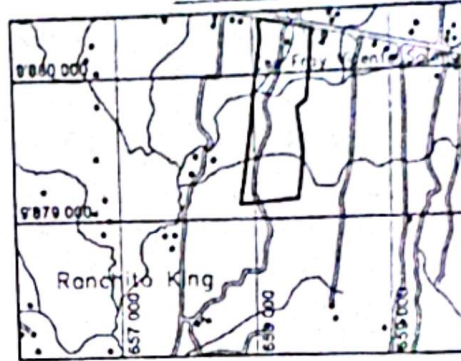

CARTA TOPOGRAFICA VELASCO IBARRA
CODIGO NIV-A2

COORDENADAS		
Vertice	X(m)	Y(m)
P1	658046	9880373
P2	658434	9880295
P3	658429	9880236
P4	658389	9879813
P5	658359	9879465
P6	658325	9879140
P7	658008	9879117
P8	658002	9879116
P9	657896	9879109
P10	658059	9880243

Datos tomados con GPS
Datum WGS 84
Proyección Cartográfica UTM
Zona 17 Sur

AREA 1:	15,0630 Has.
AREA 2:	32,3503 Has.
AREA TOTAL:	47,4133 Has.

LINDEROS Y MEDIDAS	
NORTE:	CARRETERO EL EMPALME - QUEVEDO en 395.95 m. Siguiendo Trazado.
SUR:	SALVADOR CABELLO en 317.83 m. S-85°51'1"-W; ANCHO DE CARRETERO en 6.08 m SALVADOR CABELLO en 106.23 m. S-85°13'18"-W.
ESTE:	MANUEL ANTON en 59.21 m S-4°50'38"-W; 424.89 m. S-5°24'7"-W; 349.29 m. S-4°55'38"-W; 326.77 m. S-5°58'20"-W
OESTE:	NICOLAS CRUZ en 130.65 m. N-5°42'38"-W

AMBIENTE PLANIMETRICO

GLORIA PILAR MORAN AROCA


OS RIOS	Cantón MOCACHE	Parroquia MOCACHE	Sector HUANCAVILCA
Escala 1:6000	Superficie 47,4133 Has.	Levanto y Dibujo <i>Jose Federico Bravo Bravo</i> INGENIERO CIVIL Reg. Prof. 694650	Reviso y Aprobo.



PTO.	X	Y
1	657313.00	9881214.00
2	657565.00	9881165.00
3	657565.00	9880870.00
4	657611.00	9880844.00
5	657287.00	9881082.00

ZONA 17
COORDENADAS IGN EN SAD 68

UBICACION
ESCALA: 1:25 000
C.T. LAS CUERBAS
CODIGO NIV. A28

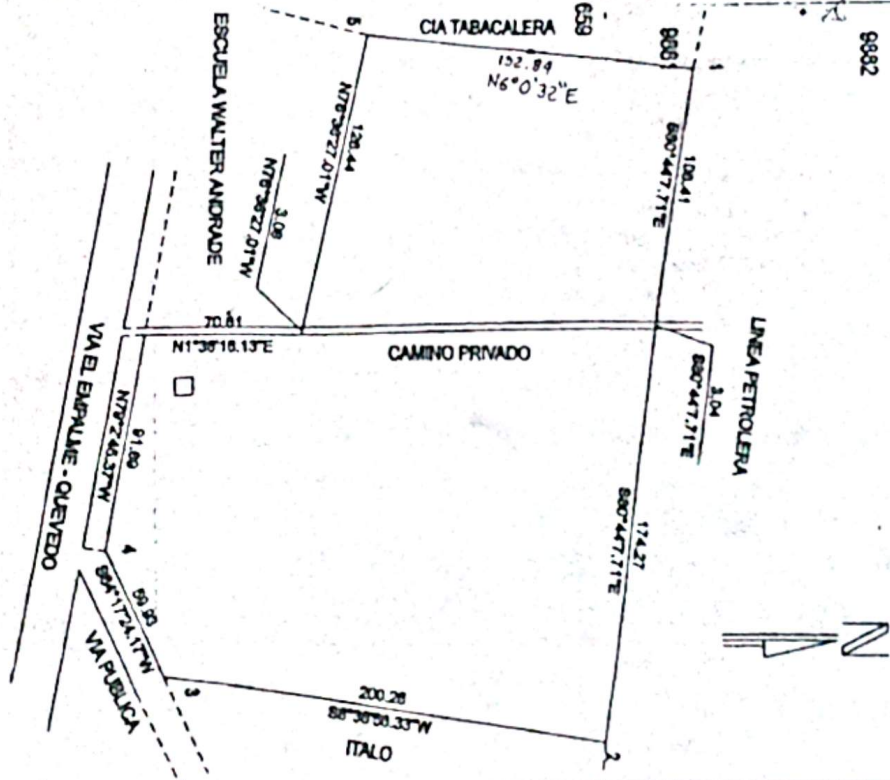

LEVANTAMIENTO PLANIMETRICO

Propietario:

SRA. GLORIA MORAN AROCA

Ubicacion:

PROVINCIA: LOS RIOS
CANTON: QUEVEDO
PARROQUIA: QUEVEDO
SECTOR: PROMAZ

Responsable:

Esteban Echeverri
Ing. Esteban Echeverri
L.P. 17 65330

Propietario:

SRA. GLORIA MORAN AROCA

PROYECTO: T. 20030

FECHA: 5.08.2013

OTRO: 2013

APROBADO:

[Signature]

Indice Nacional de
Documentos - INDI