


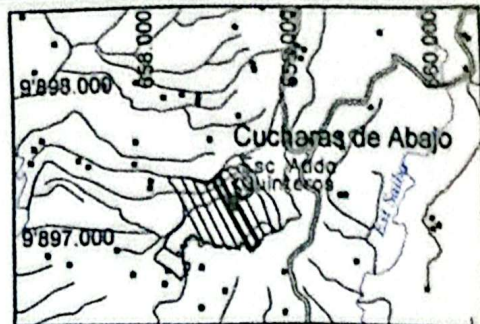


UBICACION

PROVINCIA DEL GUAYAS
CANTON EL EMPALME
PARROQUIA GUAYAS
SECTOR CUCHARAS DE ABAJO

CUADRO DE COORDENADAS		
ESTE	NORTE	PTO
658379.60	9897449.79	P1
658421.77	9897489.15	P2
658493.10	9897350.36	P3
658495.51	9897342.53	P4
658501.38	9897290.68	P5
658543.38	9897290.68	P6
658693.00	9897035.00	P7
658641.38	9896809.21	P8
658443.63	9897335.05	P9
658439.40	9897342.44	P10

Datos tomados con GPS
Datum: WGS 84
Proyección Cartográfica UTM
Zona: 17 Sur

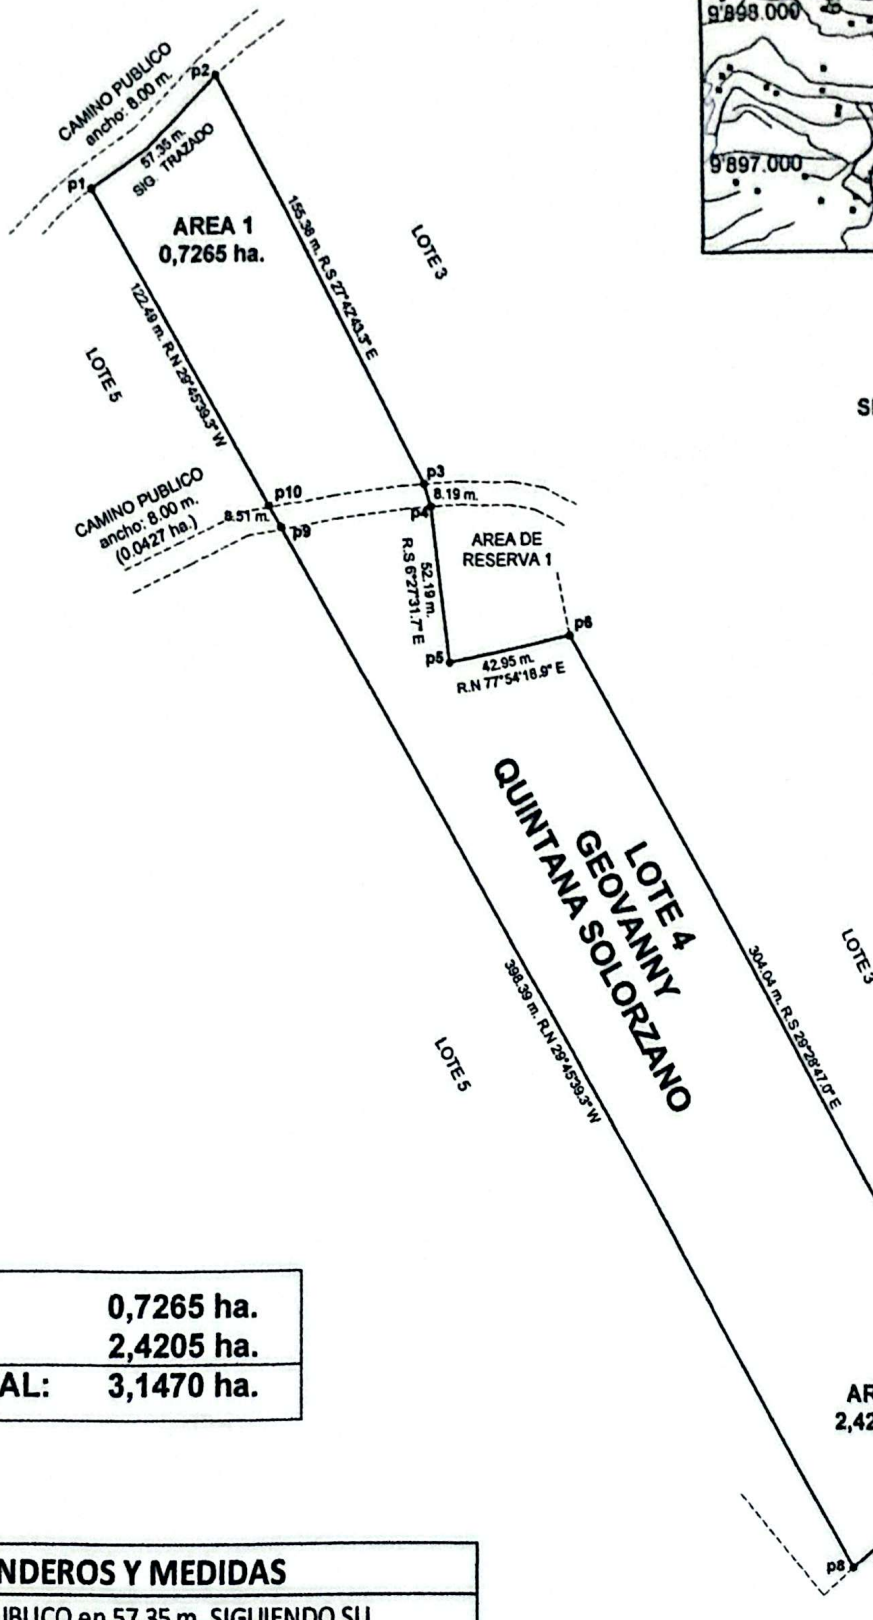

AREA 1:	0,7265 ha.
AREA 2:	2,4205 ha.
AREA TOTAL:	3,1470 ha.



LINDEROS Y MEDIDAS

NORTE	CAMINO PUBLICO en 57.35 m. SIGUIENDO SU TRAZADO
SUR	MAURO SEGOVIA en 69.00 m. R.S 48°25'25.9" W.
ESTE	LOTE 3 en 155.38 m. R.S 27°42'43.3" E; ANCHO DE CAMINO en 8.19 m: AREA DE RESERVA 1 en 52.19 m. R.S 6°27'31.7" E; 42.95 m. R.N 77°54'18.9" E: LOTE 3 en 304.04 m. R.S-29°28'47"-E.
OESTE	LOTE 5 en 398.39 m. R.N 29°45'39.3" W: ANCHO DE CAMINO en 8.51 m: LOTE 5 en 122.49 m. R.N 29°45'39.3" W.

FRACCIONAMIENTO

JOSE BENIGNO QUINTANA MURILLO

FECHA: Diciembre del 2024
ESCALA: 1: 2500
Lev. y calculó

Ing. Guido Canslang Vera
Reg. Senescyt 1008-10-100452