




LEVANTAMIENTO PLANIMETRICO

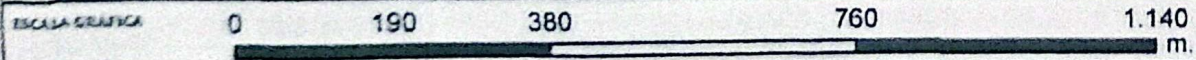

COORDENADAS PLANAS	ESCALA 1:9.500	Ref. Carta Top. IGM 1:50.000	FECHA:
Forma de Proyección: UTM	Proy. del Mapa: WGS 84	VELASCO IBARRA NIV - A2 - 3690 - 1	30 / 05 / 2024
	ÁREA: 17.6110 Ha.		

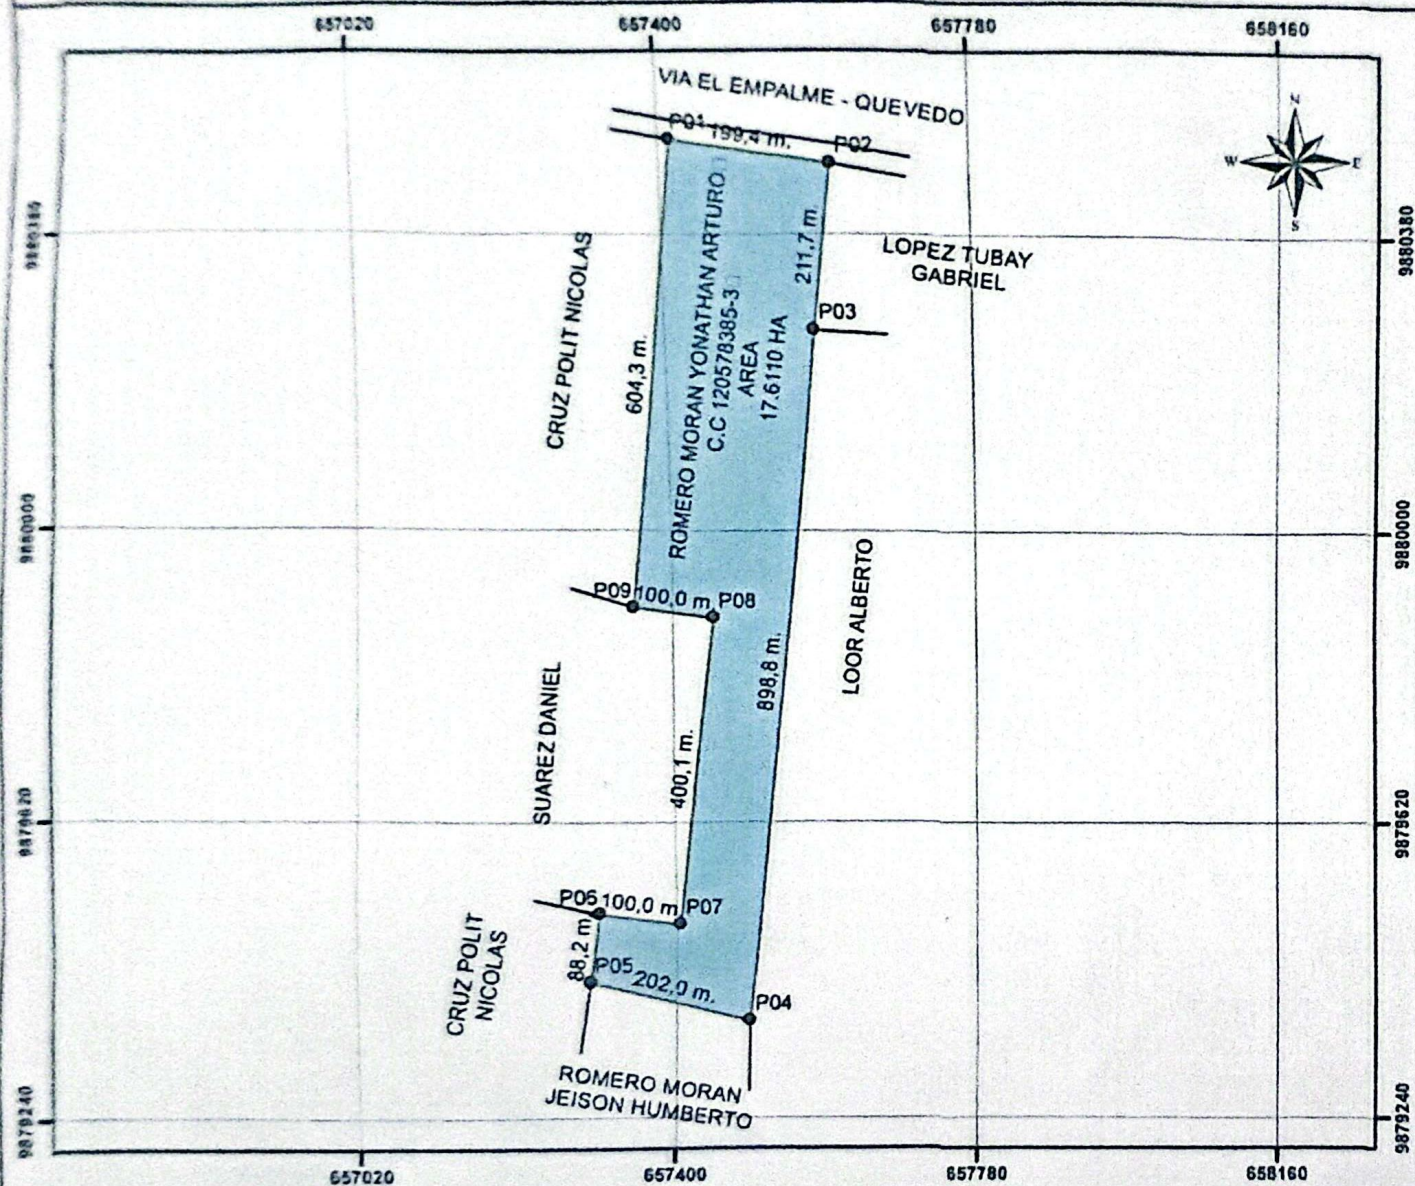

PROVINCIA	CANTÓN	PARROQUIA	SECTOR
LOS RIOS	MOCACHE	MOCACHE	HUANCABILCA
NOMBRE DEL POSESIONARIO:		NOMBRE DEL PREDIO:	
ROMERO MORAN YONATHAN ARTURO C.C. 120578385-3		S/N	
CÓDIGO PROVISIONAL		CÓDIGO CATASTRAL	

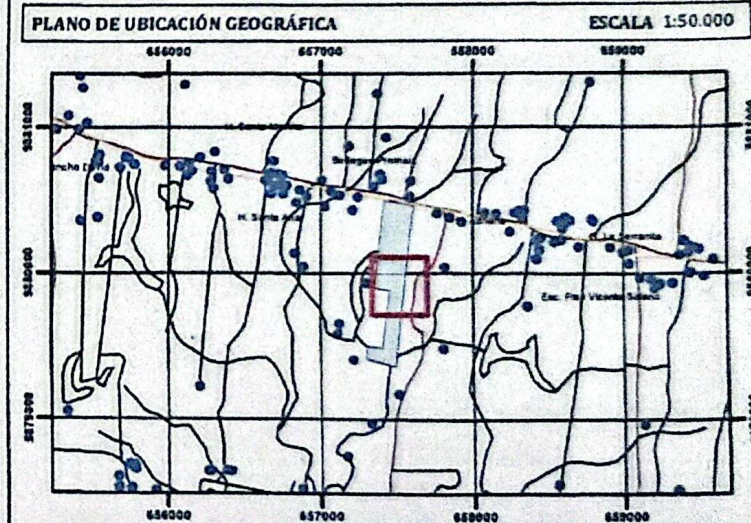

RESPONSABILIDAD TÉCNICA:	REVISADO Y APROBADO POR:
ING. ENRIQUE ZAMORA RENDON. Reg. SENESCYT: 1018-15-1362321	TÉCNICO AUTORIDAD AGRARIA NACIONAL

INFORME DE LINDERACION

DESCRIPCION DE LINDERACION

COLINDANTE NORTE

Del P01-P02 con una distancia de 199,4 m Siguiendo el trazado de la Via el Empalme - Quevedo;

COLINDANTE SUR

Del P04-P05 con una distancia de 202,0 m rumbo N 75° 57' 50" O Romero Moran Jeison Humberto ;

COLINDANTE ESTE

Del P02-P03 con una distancia de 211,7 m rumbo S 07° 19' 35" O Lopez Tubay Gabriel;
Del P03-P04 con una distancia de 898,8 m rumbo S 05° 56' 20" O Loor Alberto ;

COLINDANTE OESTE

Del P05-P06 con una distancia de 88,2 m rumbo N 06° 33' 14" E Cruz Polit Nicolas ;
Del P06-P07 con una distancia de 100,0 m rumbo S 82° 12' 25" E Suarez Daniel ; Del P07-P08 con una distancia de 400,0 m rumbo N 06° 35' 34" E Suarez Daniel ; Del P08-P09 con una distancia de 100,0 m rumbo N 82° 14' 07" O Suarez Daniel ; Del P09-P01 con una distancia de 604,3 m rumbo N 05° 59' 03" E Cruz Polit Nicolas ;

RESPONSABILIDAD TECNICA:

REVISADO Y APROBADO POR:

ING. ENRIQUE ZAMORA REMBON


Rol: SENESCYT 1018-15-1362321

AUTORIDAD AGRARIA NACIONAL

CUADRO DE DATOS


Vértices	Coord. Plano (UTM, WGS84)		Distancia (m)	Rumbo de Cuadrícula	Colindante
	Norte	Este			
P01-P02	657415,0	657415,0	199,4	Siguiendo el trazado de la	Via el Empalme - Quevedo
P02-P03	657412,0	657412,0	211,7	S 07° 19' 35" O	Lopez Tubay Gabriel
P03-P04	657585,0	657585,0	898,8	S 05° 56' 20" O	Loor Alberto
P04-P05	657492,0	657492,0	202,0	N 75° 57' 50" O	Romero Moran Jeison Humberto
P05-P06	657296,0	657296,0	88,2	N 06° 33' 14" E	Cruz Polit Nicolas
P06-P07	657306,1	657306,1	100,0	S 82° 12' 25" E	Suarez Daniel
P07-P08	657405,2	657405,2	400,0	N 06° 35' 34" E	Suarez Daniel
P08-P09	657431,1	657431,1	100,0	N 82° 14' 07" O	Suarez Daniel
P09-P01	657352,0	657352,0	604,3	N 05° 59' 03" E	Cruz Polit Nicolas
P01-	657415,0	657415,0			

EQUIPO TÉCNICO DE CATASTRO
ESTUDIO DE COBERTURA - CARTA TOPOGRÁFICA
EN VIRTUD AL OFICIO N° MAP-SUBACUA-2018-0722-O
Y COORDENADAS ADJUNTAS AL DOCUMENTO

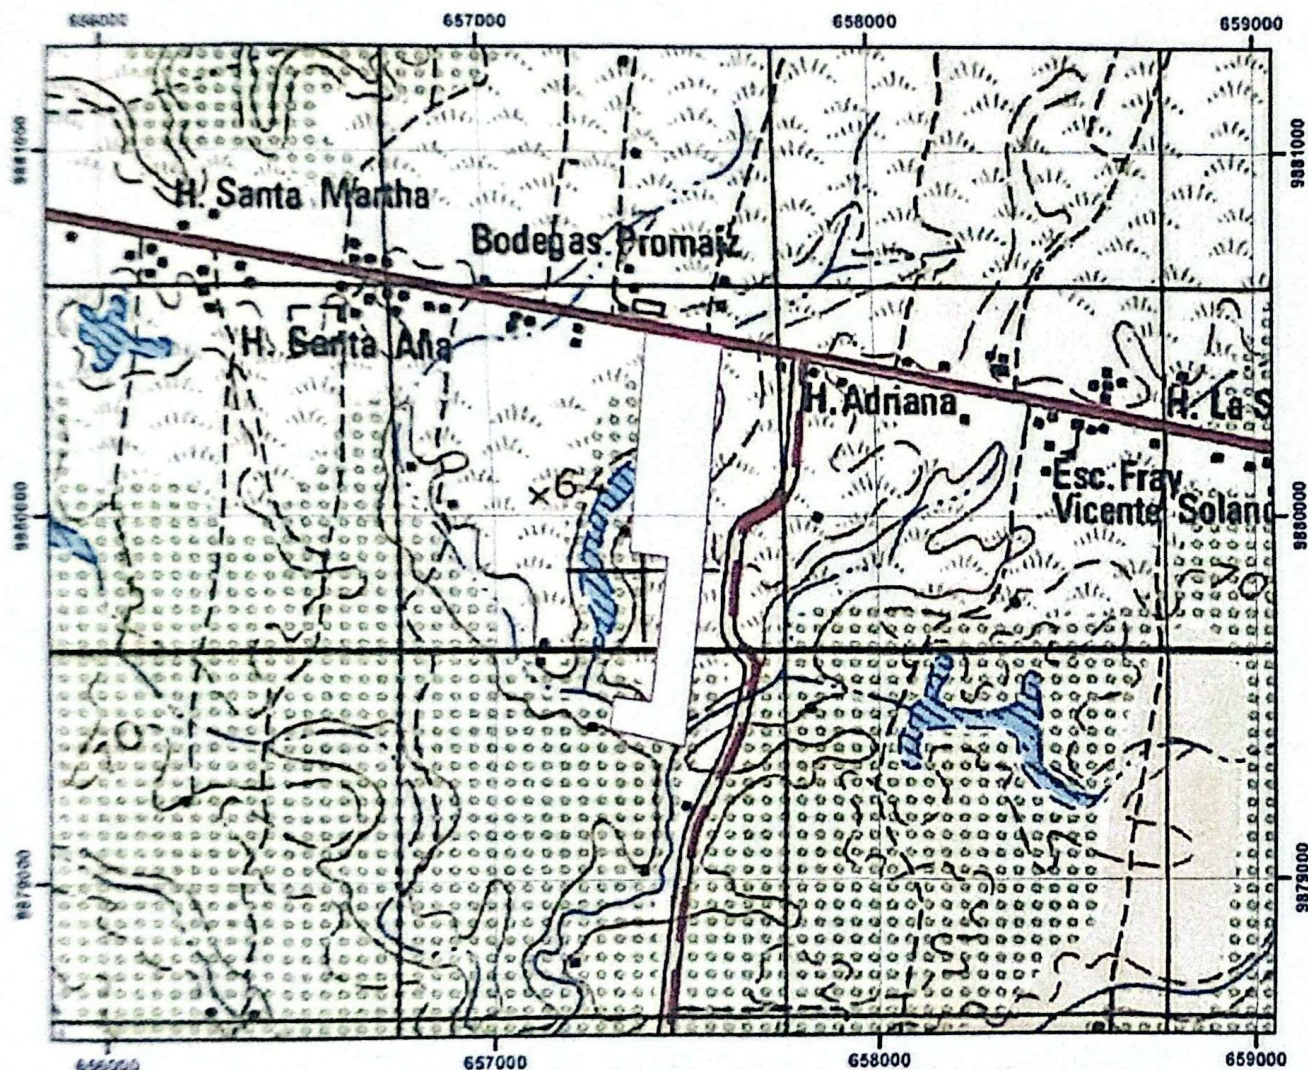

ESCALA GRAFICA 0 250 500 1.000 1.500 m.

COORDENADAS PLANAS	ESCALA 1:20.000	Ref. Carta Top. IGM 1:50.000	FECHA:
ÁREA DEL PREDIO 17.6110 Ha.	MOCACHE NIV - A4 - 3690 - II	30 / 05 / 2024	

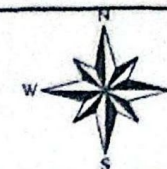

VERTICE	ESTES (X)	NORTES (Y)
P01	657415.0	9880500.0
P02	657612.0	9880445.0
P03	657545.0	9880299.0
P04	657492.0	9879365.0
P05	657296.0	9879414.0

MINISTERIO DE AGRICULTURA Y GANADERÍA
SUBSECRETARÍA DE TIERRAS Y REFORMA AGRARIA

CERTIFICACIÓN GEOGRÁFICA
ESTUDIO DE COBERTURA DE SUELO

PROVINCIA	CANTÓN	PARROQUIA	SECTOR
LOS RIOS	MOCACHE	MOCACHE	HUANCABILCA

NOMBRE DEL POSESIONARIO:	NOMBRE DEL PREDIO:
ROMERO MORAN YONATHAN ARTURO C.C 120578385-3	S/N
CÓDIGO PROVISIONAL	CÓDIGO CATASTRAL

VERIFICADO EN IMÁGENES SATELITALES Y CARTAS TEMÁTICAS
 SE CERTIFICA QUE EL PREDIO NO SE ENCUENTRA AFECTANDO
 ZONAS DE PLAYAS, BAHÍA Y MANGLAR DE LA PROVINCIA DE LOS RÍOS.

COBERTURAS

AREA DE MANGLAR:	0,0000 Ha.	TOTAL DE ZONA DEL PLAYA: 0,0000 Ha.
AREA DE SALITRAL:	0,0000 Ha.	
ZONA ALTA	0,0000 Ha.	TOTAL DE ZONA ALTA 0,0000 Ha.

AREA TOTAL: 0,0000 Ha.

RESPONSABILIDAD TÉCNICA:

AUTORIDAD AGRARIA NACIONAL