


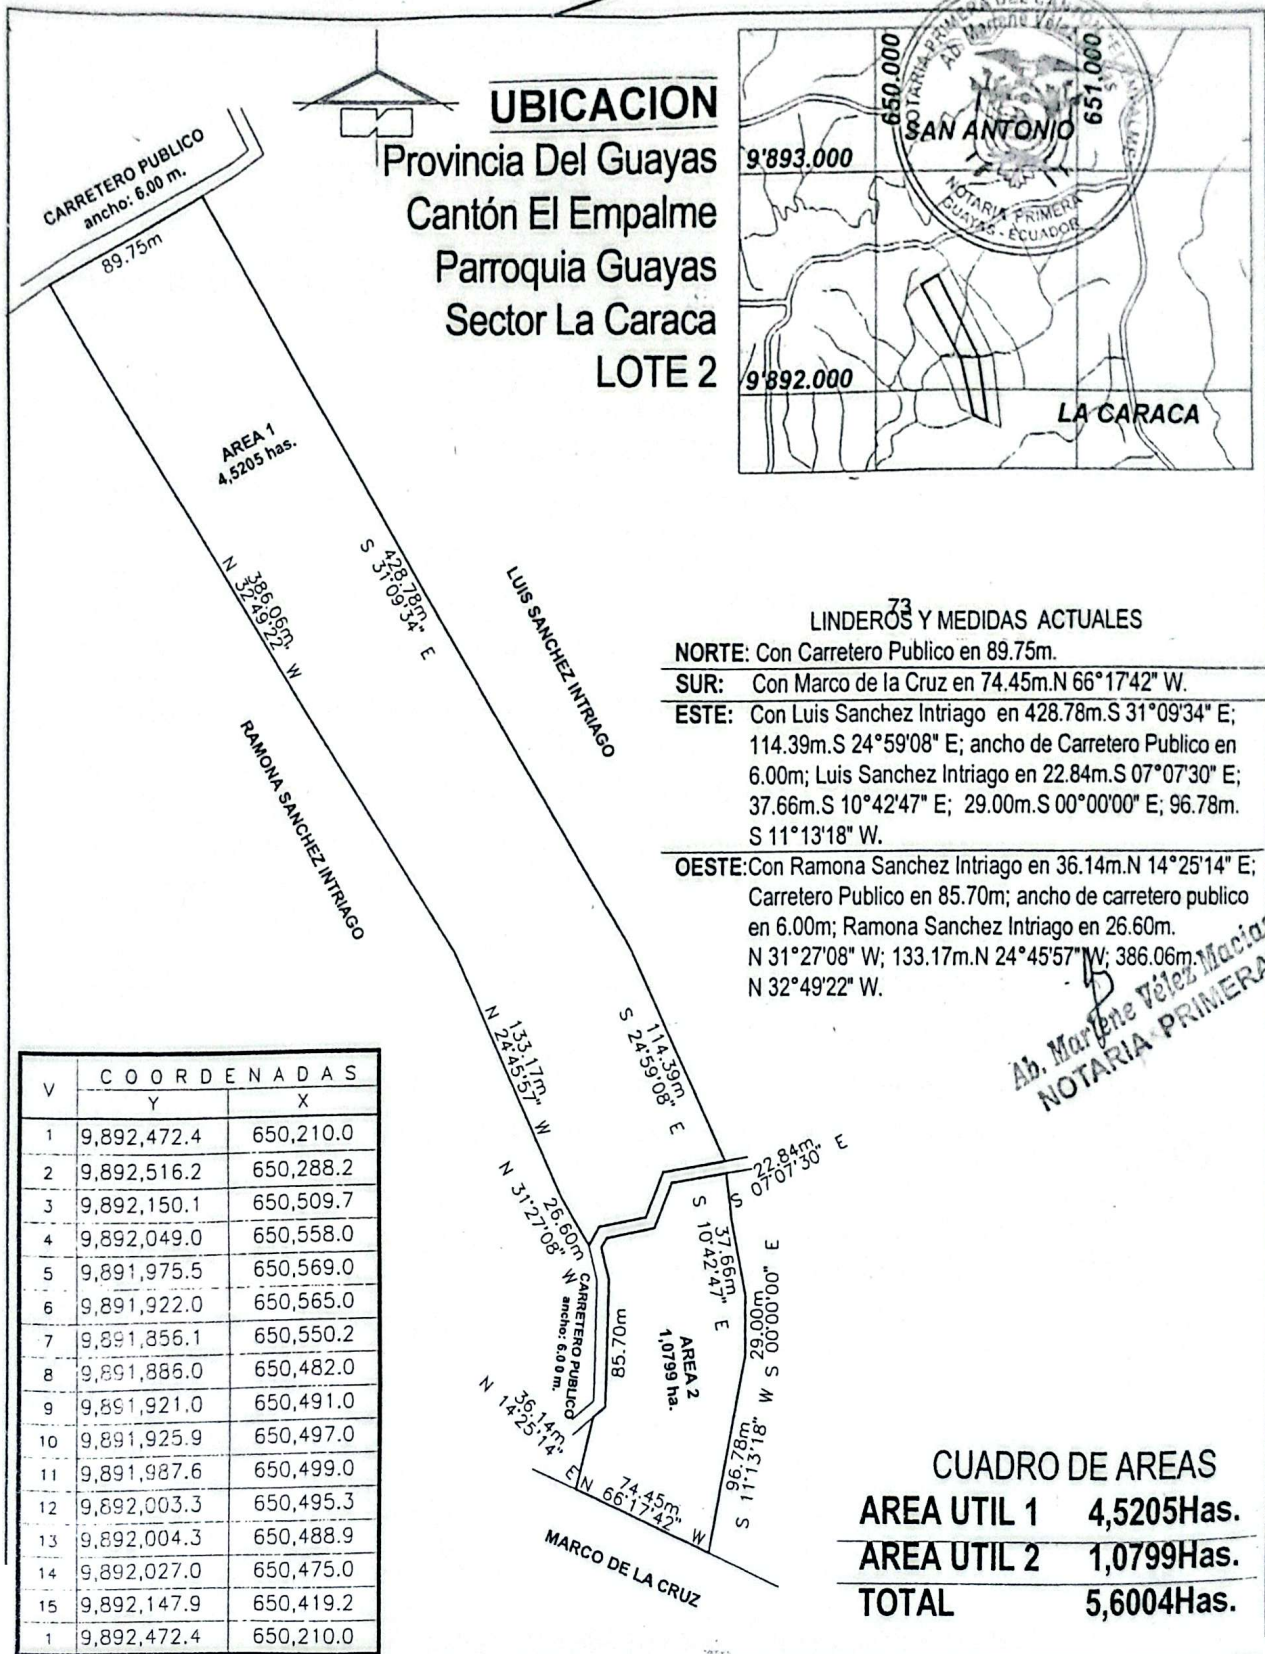

LEVANTAMIENTO PLANIMETRICO DEL TERRENO DE:

WALTER SANCHEZ INTRIAGO

Area

5,6004Has.

Fecha:

OCT./2024

Revisó y Aprobó:

[Firma]

Levantamiento planimetrico y Dibujo:

[Firma]

LAMINA

1/4

Escala:

1:300

ARQ. RICARDO LOOR C.
DIRECTOR DE ORDENAMIENTO TERRITORIAL

NERY MORA BURGOS
DIBUJANTE



CERTIFICADO DE DEFUNCIÓN

La Dirección General de Registro Civil, Identificación y Cedulación, en base a la información que tiene registrada, emite el presente certificado:

Apellidos y nombres del/la fallecido/a:

SANCHEZ INTRIAGO WALTER OSWALDO

NUI/Pasaporte: 0901991901

Sexo: HOMBRE

Edad: 65

Estado civil: SOLTERO

Nacionalidad: ECUATORIANA

Fecha de fallecimiento: 8 DE NOVIEMBRE DE 2017

Lugar de fallecimiento (país/provincia/cantón/parroquia):

ECUADOR/PICHINCHA/QUITO/COTOCOLLAO

Fecha de registro de defunción: 9 DE NOVIEMBRE DE 2017

Lugar de registro de defunción (país/provincia/cantón/parroquia):

ECUADOR/GUAYAS/EL EMPALME/VELASCO IBARRA

Tomo / Página / Acta: 15 / 53 / 53

Datos del padre: LEOVILDO SANCHEZ

Datos de la madre: RINA INTRIAGO

Nombre del / la cónyuge o conviviente: No Registra

Causas del fallecimiento: INSUFICIENCIA HEPATICA

Información certificada a la fecha: 5 DE DICIEMBRE DE 2024

Emissor: INTRIAGO ARIAS JEAN CARLOS

N° de certificado: 240-087-21703



240-087-21703

Ldo. Ottón José Rivadeneira González
Director General del Registro Civil, Identificación y Cedulación
Documento firmado electrónicamente

