



LEVANTAMIENTO PLANIMETRICO

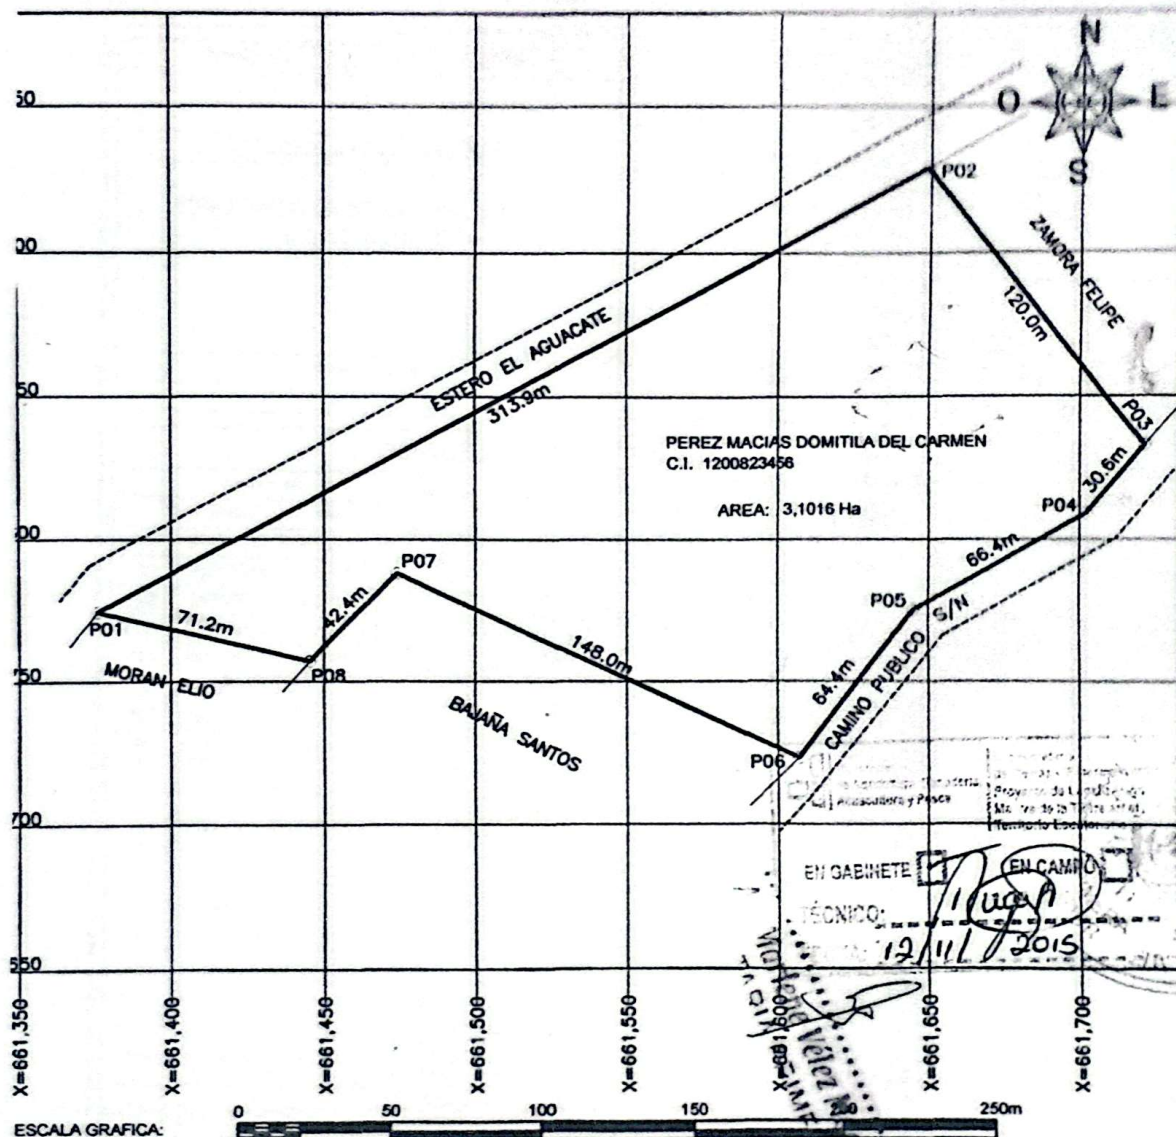

SISTEMA NACIONAL DE REFORMACION Y GESTION DE TIERRAS RURALES
E INFORMATICA TECNOLÓGICA

PROVINCIA	CANTON	PARROQUIA	SECTOR
GUAYAS	EL EMPALME	GUAYAS	EL AGUACATE
NOMBRE DEL POSESIONARIO		NOMBRE DEL PRECIO	
PEREZ MACIAS DOMITILA DEL CARMEN C.I. 1200823456		S/N	

REFERENCIA CARTOGRAFICA PARA LA UBICACION

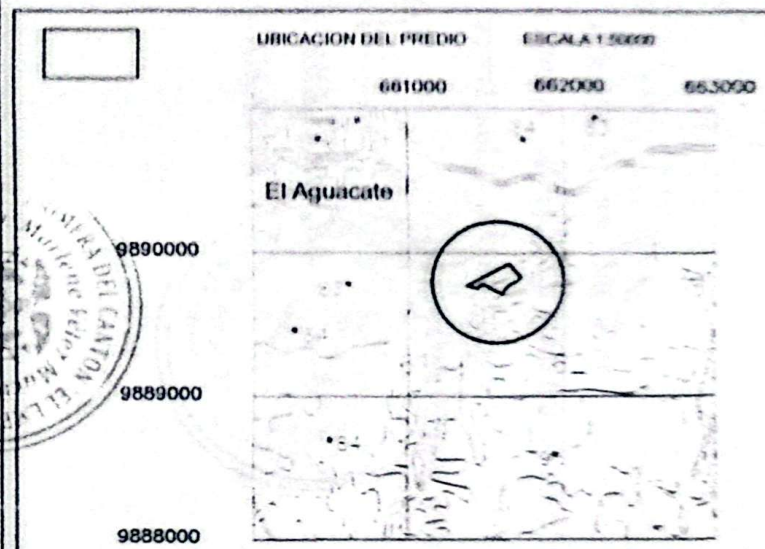

ESCALA GRAFICA:



ORDENADAS PLANAS UTM

TEMA WGS84 ZONA 17S

ESCALA

1:2500

AREA

3,1016 Ha

REF. CARTA TOP. IGM 1:50,000

GUAYAS NIII-E4,3691-II

FECHA

08/11/2015

ELABORADO POR

JESSICA P. MUÑOZ N.

ING. MUÑOZ NIVELA JESSICA PAOLA
Reg. Prof. Reg. SENESCYT 1006-07-751854

REVISADO Y APROBADO POR

1. MUÑOZ N.

Subsecretaría de Tierras y Reforma Agraria

INFORME DE LINDERACIÓN			
Provincia	Cantón	Parroquia	Sector
GUAYAS	EL EMPALME	GUAYAS	EL AGUACATE
Nombre del Posesionario		Nombre del predio	
PEREZ MACIAS DOMITILA DEL CARMEN C.I. 1200823456		S/N	
Código Provisional		Código Catastral	

[illegible]

DESCRIPCION DE LINDERACIÓN	
COLINDANTE NORTE	
Del P01-P02 con una distancia de 313.9 m rumbo SIGUIENDO SU CURSO ESTERO EL AGUACATE;	
COLINDANTE SUR	
Del P03-P04 con una distancia de 30.6 m rumbo SIGUIENDO SU TRAZADO CAMINO PUBLICO S/N; Del P04-P05 con una distancia de 66.4 m rumbo SIGUIENDO SU TRAZADO CAMINO PUBLICO S/N; Del P05-P06 con una distancia de 64.4 m rumbo SIGUIENDO SU TRAZADO CAMINO PUBLICO S/N; Del P06-P07 con una distancia de 148.0 m rumbo N 63° 57' 15" O BAJANA SANTOS; Del P07-P08 con una distancia de 42.4 m rumbo S 43° 05' 27" O BAJANA SANTOS;	
COLINDANTE ESTE	
Del P02-P03 con una distancia de 120.0 m rumbo S 36° 52' 12" E ZAMORA FELIPE;	
COLINDANTE OESTE	
Del P08-P01 con una distancia de 71.2 m rumbo N 76° 00' 21" O MORAN ELIO;	
RESPONSABLE TÉCNICO: Jessica P. Muñoz M. ING. MARCO NOVELA JESSICA PAOLA REG. SEMECOT. 1008-87-75161	REVISADO Y APROBADO POR: Subsecretaría de Tierras y Reforma Agraria