


REPUBLICA DEL ECUADOR

807-940
23/Julio/2015



GAD. MUNICIPAL DE MOCACHIZ
DEP. AVALUOS Y CATASTROS
CATASTRADA

Fecha 14/09/2015 Area 2-20/11/15
Clave Ant. 12643 RC
Clave Ant. 12643 RC
Ident. Parcela 03-614

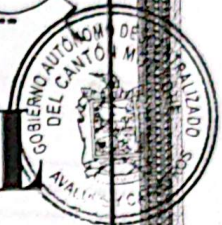

**NOTARIA TERCERA DEL
CANTON QUEVEDO**

PRIMERA

TESTIMONIO DE LA ESCRITURA PUBLICA

COMPRVENTA:- DE UN SOLAR DE TERRENO URBANO QUE HACE LA SEÑAL
DEYSI VALERIA VELIZ CEDEÑO A FAVOR DEL SEÑOR PABLO ALFREDO
VELIZ CARCAMO.

CUANTIA:- \$ 2.938,00

DEL REGISTRO DE ESCRITURAS PUBLICAS DEL AÑO 201 5

**AB. ABEL GERMAN LEON LEON
NOTARIO**

Quevedo, 10 de Julio

del 201 5



Factura: 001-003-000008060




20151205003P03973

NOTARIO(A) ABEL GERMAN LEON LEON
NOTARÍA TERCERA DEL CANTON QUEVEDO
EXTRACTO

Escritura N°:	20151205003P03973						
ACTO O CONTRATO:							
COMPRAVENTA							
FECHA DE OTORGAMIENTO:	10 DE JULIO DEL 2015						
OTORGANTES							
OTORGADO POR							
Persona	Nombres/Razón social	Tipo interviniente	Documento de Identidad	No. Identificación	Nacionalidad	Calidad	Persona que le representa
Natural	VELIZ CEDEÑO DEYSI VALERIA	POR SUS PROPIOS DERECHOS	CÉDULA	1203426208	ECUATORIANA	VENDEDOR(A)	
A FAVOR DE							
Persona	Nombres/Razón social	Tipo Interviniente	Documento de Identidad	No. Identificación	Nacionalidad	Calidad	Persona que representa
Natural	VELIZ CARCAMO PABLO ALFREDO	POR SUS PROPIOS DERECHOS	CÉDULA	1204154577	ECUATORIANA	COMPRADOR (A)	
UBICACIÓN							
Provincia		Cantón			Parroquia		
LOS RIOS		QUEVEDO			QUEVEDO		
DESCRIPCIÓN DOCUMENTO:							
OBJETO/OBSERVACIONES:							
CUANTIA DEL ACTO O CONTRATO:	2938.00						

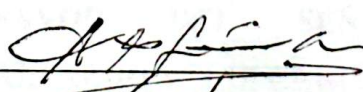


NOTARIO(A) ABEL GERMAN LEON LEON
NOTARÍA TERCERA DEL CANTON QUEVEDO



**VENTA DE UN SOLAR DE TERRENO
URBANO QUE HACE LA SEÑORA
DEYSI VALERIA VELIZ CEDEÑO A
FAVOR DEL SEÑOR PABLO
ALFREDO VELIZ CARCAMO.-----**

CUANTÍA: \$ 2.938.00.-----

**En Quevedo, cabecera del Cantón del mismo nombre, Provincia
de Los Ríos, República del Ecuador, el día de hoy Viernes diez
de Julio del año dos mil quince, ante mí, Abogado ABEL
GERMÁN LEÓN LEÓN, Notario Titular Tercero del Cantón**

Quevedo, comparecen: por una parte, por sus propios derechos, la señora **DEYSI VALERIA VELIZ CEDEÑO**, quien declara ser ecuatoriana, de ocupación quehaceres domésticos; y su cónyuge señor **ROBERTO BERNARDO MACIAS GUEVARA**, quien declara ser ecuatoriano, de ocupación estudiante; y, por otra parte, por sus propios derechos, el señor **PABLO ALFREDO VELIZ CARCAMO**, quien declara ser ecuatoriano, de estado civil soltero, de ocupación estudiante; nacionalidad Ecuatoriana, mayores de edad, con domicilio y residencia en el Cantón Mocache, de tránsito en esta Ciudad, capaces para obligarse y contratar a quienes de conocer doy fe. Bien instruidos en el objeto y resultados de esta escritura de **COMPRAVENTA**, a la que proceden con amplia y entera libertad, para su otorgamiento me presentaron la minuta del tenor siguiente.- **MINUTA:- SEÑOR NOTARIO.-** En el Registro de escrituras públicas que se encuentran a su cargo, sírvase usted autorizar una de Compraventa, de conformidad con las siguientes cláusulas.-----

PRIMERA: INTERVINIENTES.- Comparecen a la celebración de la presente escritura Pública de Compraventa, por una parte, por sus propios derechos, la señora **DEYSI VALERIA VELIZ CEDEÑO** y su cónyuge señor **ROBERTO BERNARDO MACIAS GUEVARA**; a quien en adelante se le denominara simplemente **LA PARTE VENDEDORA**; y, por otra parte, por sus propios derechos, el señor **PABLO ALFREDO VELIZ CARCAMO**, a quien en adelante se le denominará simplemente **LA PARTE COMPRADORA**.-----



SEGUNDA: ANTECEDENTES.-Que con el número quinientos treinta y seis en el Registro de Propiedades, quedando anotada al número setecientos veintinueve del Libro Repertorio, el diecinueve de noviembre del año dos mil ocho, consta inscrita la escritura celebrada ante el Notario Primero del Cantón Quevedo, Abogado Marcos Baratau Murillo, el Viernes veintidós de Agosto del año dos mil ocho, en la que se adjudicó a favor de la heredera **DEYSI VALERIA VELIZ CEDEÑO**, en pago de su cuota hereditaria un lote de terreno ubicado en el sector correspondiente a la Pre-Cooperativa John F. Kennedy, Jurisdicción del Cantón Mocache, Provincia de Los Ríos, el mismo que está signado el número DOS de la superficie de **DOS HECTAREAS, VEINTISÉIS AREAS**; circunscrito dentro de los siguientes linderos; **por el NORTE:** Con lote uno, en cuatrocientos veintiocho metros; **por el SUR:** Con lote tres, en cuatrocientos cuarenta y ocho metros; **por el ESTE:** Con terreno de otros propietarios, en cincuenta y seis metros; y, **por el OESTE:** Propiedad de Simón Álvarez, en sesenta metros. - - - - -

TERCERA:- COMPRAVENTA.- Con los antecedentes pormenorizados en la Cláusula Segunda de esta escritura, la vendedora señora **DEYSI VALERIA VELIZ CEDEÑO**, debidamente autorizada por su cónyuge señor **ROBERTO BERNARDO MACIAS GUEVARA**, por sus propios derechos, tienen a bien, dar en venta real y enajenación perpetua, a favor del señor **PABLO ALFREDO VELIZ CARCAMO**, el lote de terreno ubicado en el sector correspondiente a la Pre-Cooperativa John F Kennedy, Jurisdicción del Cantón Mocache, Provincia de

Los Ríos, el mismo que está signado el número DOS de la superficie de DOS HECTAREAS VEINTISÉIS AREAS. ----

CUARTA:- PRECIO.- El precio pactado entre la vendedora y la compradora, por el inmueble o lote de terreno urbano materia de esta escritura, es de: **DOS MIL NOVECIENTOS TREINTA Y OCHO DÓLARES AMERICANOS**, el mismo que la vendedora declara, que lo recibe en este acto, en dinero efectivo y en billetes de legal circulación, a su entera satisfacción, de manos del comprador, sin lugar a ningún reclamo posterior.-----

QUINTA:- DECLARACIONES.- a) La señora **DEYSI VALERIA VELIZ CEDEÑO**, declara, que el inmueble o lote de terreno urbano que vende por esta escritura, está libre de embargo o prohibición judicial de enajenar o gravar, pero que, no obstante, queda obligado al saneamiento por evicción o vicios redhibitorios, en los términos que señale la Ley; b) Por su parte, el comprador declara, que acepta las declaraciones del vendedor, por convenir a sus intereses, y que la compra la hace para sí, a título oneroso y con dinero de su propio peculio.-----

Usted, señor Notario se dignará agregar todas las formalidades de ley, para alcanzar su completa validez.-----

Firmado: Temis Véliz Véliz.- **ABOGADA** – Matrícula número doce – dos mil siete – doce– Foro de Abogados – Consejo de la Judicatura. -----

Se agregan los documentos habilitantes respectivos. Hasta aquí la minuta y los documentos que se agregan que, en un mismo texto quedan elevados a escritura pública.-----



REGISTRO MUNICIPAL DE LA PROPIEDAD Y MERCANTIL DEL CANTÓN MOCACHE

28 de mayo y bolívar esquina/

E-MAIL:



FICHA REGISTRAL

2319

Cod. Catastral/Rol/Ident. Predial



20

Conforme a la solicitud Número:952 certifico hasta el día de hoy la Ficha Registral Número 2.319:

Fecha de Apertura: viernes, 20 de marzo de 2015

La FICHA REGISTRAL contiene:

La historia jurídica del predio que consta en los archivos de este Registro de la Propiedad

INFORMACIÓN REGISTRAL

TIPO DE PREDIO: Inmueble Rural

PROPIETARIO(S): VELIZ CEDEÑO DEYSI VALERIA

CARACTERISTICAS Y LINDEROS REGISTRALES:

PARROQUIA: Mocache

TERRENO

Norte: con camino en 220m. lote No.54 en 110.- N. 00°00'S, 250m. 90°00'E, Estero, en 425m. lote No.54m. 135m. N. 90°00'E

Sur: con lote No.71. 418m. S. 90°00'W

Este: con lote No.66 en 124m. S. 10°45'W; lote No. 70 en 200m. S. 10°45'W

Oeste: con lote No.64 en 750m. N. 20°20'W

ubicado en el sector correspondiente a la Pre-Cooperativa John F. Kennedy, en la Jurisdicción del Cantón Mocache, Provincia de Los Ríos

Con una Superficie Total de 2.20 HAS

Este bien inmueble, de acuerdo a los movimientos registrales, no soporta Gravamen(es) vigente(s).

RESUMEN DE MOVIMIENTOS REGISTRALES:

Libro	Acto	Número y Fecha de Inscripción	Folio Inicial
Propiedades	Partición Extrajudicial	536 19-nov-2008	9.125

DETALLE DE LOS MOVIMIENTOS REGISTRALES:

REGISTRO DE PROPIEDADES

Partición Extrajudicial

Inscrito el: miércoles, 19 de noviembre de 2008

Tomo: 10/2.008

Folio Inicial: 9.125

Folio Final: 9.196

Número de Inscripción: 536

Número de Repertorio: 729

Oficina donde se guarda el documento original: Notaría Primera

Certificación elaborada por: CINTHYA MONTOYA

Ficha No: 2319

Página 1 de 3

Cantón donde se encuentra la oficina:

Quevedo

Fecha de Otorgamiento:

viernes, 22 de agosto de 2008

Oficio/Telex/Fax:

a.- Observaciones:

b.- Apellidos, Nombres y Domicilio de las Partes:

Papel	Cédula o R.U.C.	Nombre y/o Razón Social	Estado Civil	Domicilio
Herederero	0910369707	VELIZ CEDEÑO OLINDA DE JESUS	Soltero	Mocache
Herederero	1203182108	VELIZ CEDEÑO PABLO ANTONIO	Soltero	Mocache
Herederero	1201275144	VELIZ CEDEÑO JOSE SIMON	Soltero	Mocache
Herederero	1708142193	VELIZ CEDEÑO JUANA DEL CARMEN	Soltero	Mocache
Herederero	17006510201	VELIZ CEDEÑO ANA MERCEDES	Soltero	Mocache
Herederero	0906115217	VELIZ CEDEÑO DELIA MARIA	Casado	Mocache
Herederero	1201018687	VELIZ CEDEÑO BLANCA LUPE	Soltero	Mocache
Herederero	1708066913	VELIZ CEDEÑO ERMES WILLIAMS	Casado	Mocache
Herederero	1206269035	VELIZ CEDEÑO ANGELA GERMANIA	No especific	Mocache
Herederero	1709097750	VELIZ CEDEÑO FLOR SHIRLEY	Soltero	Mocache
Herederero	1710618131	VELIZ CEDEÑO ALEXANDRA ELIZABETH	Soltero	Mocache
Herederero	1203185259	VELIZ CEDEÑO PABLA ADALBERTO	Soltero	Mocache
Herederero	1204708257	VELIZ MOREIRA OSCAR VICENTE	No especific	Mocache
Herederero	1205158007	VELIZ MOREIRA ELIO EULALIO	Soltero	Mocache
Herederero	0923910269	VELIZ MOREIRA OSCAR MIGUEL	Soltero	Mocache
Herederero	0923910277	VELIZ MOREIRA PEDRO DAVID	Soltero	Mocache
Heredereros - Propietario	1203426208	VELIZ CEDEÑO DEYSI VALERIA	Casado	Mocache

c.- Esta inscripción se refiere a la(s) que consta(n) en:

Libro	No. Inscripción	Fec. Inscripción	Folio Inicial	Folio

TOTAL DE MOVIMIENTOS REGISTRALES:

Libro	Número de Inscripciones
Propiedades	1

Gravámenes	
Libro	Número de Inscripciones

Los movimientos Registrales que constan en esta ficha registral son los únicos que se refieren al predio que se certifica.

Cualquier enmendadura, alteración o modificación al texto de este certificado lo invalida.


MOCACHE, viernes 20 de marzo de 2.015

Impreso a las: 02:20:40p.m.



20

El interesado deberá comunicar cualquier error u omisión en este Documento al Registrador de la Propiedad.

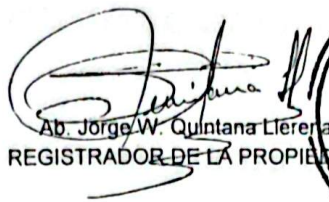
Ab. Jorge W. Quintana Llerena
REGISTRADOR DE LA PROPIEDAD





ESPACIO EN BLANCO

I. MUNICIPALIDAD DEL CANTON QUEVEDO



Nº _____ IMPUESTO DE ALCABALA Por \$ 38.48

Señor Tesorero Municipal Confiéreme CERTIFICADO DE PAGO POR IMPUESTO DE ALCABALA.

Para celebración de la escritura de Compraventa de un PREDIO RURAL de la superficie de DOS HECTAREAS, VEINTISEIS AREAS, ubicado en el sector correspondiente a la Pre-cooperativa John F. Kennedy, jurisdicción del Cantón Mocache, Provincia de Los Ríos.

Otorgado por: **LA SEÑORA DEYSI VALERIA VELIZ CEDEÑO**
A favor del señor **PABLO ALFREDO VELIZ CARCAMO**

Del predio ubicado en: EL Cantón Mocache.

Por la cuantía Total \$ 2.938,00


ALCABALA	\$ 29.38
JUNTA BENEF.	\$ 8.81
CONS. PROV.	\$ 0.29
TOTAL \$	\$ 38.48

CERTIFICO: Que en esta fecha he cobrado el valor de los

Los impuestos detallados en aviso preinserto.

Quevedo a 7 de Abril del 2015.


EL NOTARIO

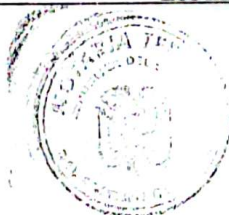

TESORERIA MUNICIPAL



Gobierno Autónomo Descentralizado
Municipal del Cantón Mocache

COMP/ BANTE INGRESO CAJA

MOCACHE

IMPUESTO PREDIAL RUSTICO	AÑO 2015	REG. CATASTRAL 12643	FIC. CATASTRAL	FECHA EMISIÓN 07-abr-2015
NOMBRE DEL CONTRIBUYENTE VELIZ CEDEÑO DEYSI VALERIA		R.U.C. / CÉDULA 0	PARROQUIA MOCACHE	
DIRECCIÓN / NOMBRE PREDIO S/N			AVALÚO DE LA PROPIEDAD \$ 2,938.00	
IMPUESTO PRINCIPAL Y ADICIONALES				
Imp. Predial Rural	0.00	Total Impuesto Causado: 4.44		
Serv. Admín.	3.00	Descuento: 0.00		
T. Seguridad	1.00	Recargo/Interes: 0.00		
C. Bomberos		TOTAL PAGO: \$ 4.44		



**GOBIERNO AUTÓNOMO DESCENTRALIZADO
MUNICIPAL DEL CANTÓN MOCACHE**
07 ABR 2015
**CANCELADO
TESORERÍA**

2015VGLX33422

CONTRIBUYENTE

Meybol Aracely

COMPROBANTE DE INGRESO A CAJA


SERIE : 001- 000068861

CONTRIBUYENTE

VELIZ CARCAMO PABLO ALFREDO

CEDULA - RUC: 000164577

FECHA DE EMISION: 07/04/2015

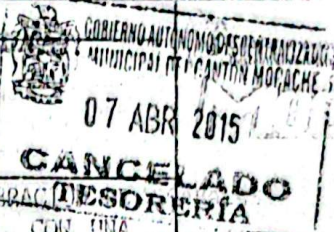

PAGO DE ALCABALAS Y SUS ADICIONALES PARA LA CELEBRACION DE ESCRITURA DE COMPRAVENTA DE UN LOTES DE TERRENO, CON UNA SUPERFICIE DE 2HAS, CON 26,00AREAS, UBICADO EN EL CANTON MOCACHE

29,20
5,23
2,94
1,00

OTORGADO VELIZ CEDENO DEYSI VALERIA



CUANTIA

67 2.938,0

RECAUDACION

SUBTOTAL:

DESCUENTO:

RECARGO/INTERES: 42,13

TOTAL A PAGAR:

ESPESIMBLANCO

REPÚBLICA DEL ECUADOR
DIRECCIÓN GENERAL DE REGISTRO CIVIL
IDENTIFICACIÓN Y CEDULACIÓN

CÉDULA DE CIUDADANÍA
Nº 120342620-8

APELLIDOS Y NOMBRES
VELIZ CEDENO
DEYSI VALERIA
LUGAR DE NACIMIENTO
LOS RIOS
MOCACHE
MOCACHE
FECHA DE NACIMIENTO 1974-09-11
NACIONALIDAD ECUATORIANA
SEXO F
ESTADO CIVIL Casada
ROBERTO BERNARDO
MACIAS GUEVARA



INSTRUCCIÓN BÁSICA
1. QUEHACER DOMESTICOS
V354319241

APELLIDOS Y NOMBRES DEL PADRE
VELIZ UNAMUNO ABSALON
APELLIDOS Y NOMBRES DE LA MADRE
CEDENO CARRIEL ANA DE JESUS
LUGAR Y FECHA DE EXPEDICIÓN
GUAYAQUIL
2009-10-28
FECHA DE EXPIRACIÓN
2019-10-28

PROFESIÓN
QUEHACER DOMESTICOS

DIRECCIÓN GENERAL
FRANCA DEL CERRADO

REPÚBLICA DEL ECUADOR
CONSEJO NACIONAL ELECTORAL
CRE

063
CERTIFICADO DE VOTACIÓN
ELECCIONES SECCIONALES 23-FEB-2014

063 - 0150
NÚMERO DE CERTIFICADO
CÉDULA
VELIZ CEDEÑO DEYSI VALERIA

LOS RIOS
PROVINCIA
VENTANAS
CANTÓN

CIRCUNSCRIPCIÓN
VENTANAS
PARROQUIA

0
E
ZONA

063-0150
PRESIDENTE DE LA JUNTA

CÍUDADANIA
No 090724008

MACIAS GUEVARA ROBERTO BERNARDO
LOS RIOS/MOCACHE/MOCACHE
PO. AGOSTO 1959
002-E 0103 01003 M
LOS RIOS/ QUEVEDO
QUEVEDO 1959

Robert Macias

ECUATORIANA*****
V354319241

CASADO
DEYSI VELIZ CEDENO
SECUNDARIA
ESTUDIANTE
FRANCISCO MACIAS
LEONARDA GUEVARA
GUAYAQUIL
11/08/2005
11/08/2017
REN 1192201
Gys

REPÚBLICA DEL ECUADOR
CONSEJO NACIONAL ELECTORAL
CRE

007
CERTIFICADO DE VOTACIÓN
ELECCIONES SECCIONALES 23-FEB-2014

007 - 0022
NÚMERO DE CERTIFICADO
CÉDULA
MACIAS GUEVARA ROBERTO BERNARDO

GUAYAS
PROVINCIA
GUAYAQUIL
CANTÓN

CIRCUNSCRIPCIÓN
FEBRES CORDERO
PARROQUIA

1
10
ZONA

ENTB
PRESIDENTE DE LA JUNTA

CÍUDADANIA (O):

Este documento acredita que usted
sufragó en las Elecciones Seccionales
23 de Febrero de 2014

ESTE CERTIFICADO SIRVE PARA TODOS
LOS TRÁMITES PÚBLICOS Y PRIVADOS



REPÚBLICA DEL ECUADOR
DIRECCIÓN GENERAL DE REGISTRO CIVIL
IDENTIFICACIÓN Y CREDULACIÓN



CÉDULA DE
CIUDADANÍA
APELLIDOS Y NOMBRES
VELIZ CARCAMO
PABLO ALFREDO
LUGAR DE NACIMIENTO
LOS RIOS
VENTANAS
VENTANAS
FECHA DE NACIMIENTO: 1977-07-20
NACIONALIDAD: ECUATORIANA
SEXO: M
ESTADO CIVIL: SOLTERO

Nº 120415457-7



INSTRUCCIÓN

BACHILLERATO

PROFESIÓN / OCUPACIÓN
ESTUDIANTE

V3131V2221

APELLIDOS Y NOMBRES DEL PADRE
VELIZ CEBEÑO PABLO ANTONIO

APELLIDOS Y NOMBRES DE LA MADRE
CARCAMO SANCHEZ FELIPA LEONOR

LUGAR Y FECHA DE EXPEDICIÓN
QUEVEDO

2013-07-18

FECHA DE EXPIRACIÓN
2023-07-18

[Signature]
DIRECTOR GENERAL

[Signature]
FRASE DEL CREDULADO



REPÚBLICA DEL ECUADOR
CONSEJO NACIONAL ELECTORAL



002

CERTIFICADO DE VOTACIÓN
ELECCIONES SECCIONALES 23-FEB-2014

002 - 0029

1204154577

NÚMERO DE CERTIFICADO

CÉDULA

VELIZ CARCAMO PABLO ALFREDO

LOS RIOS
PROVINCIA
MOCACHE

CIRCUNSCRIPCIÓN
MOCACHE

0

CANTÓN

PATRULLA

2 ZONA

[Signature]
PRESIDENTE DE LA JUNTA

CIUDADANÍA (O)

Este documento acredita que usted
sufragó en las Elecciones Seccionales

23 de Febrero de 2014

ESTE CERTIFICADO SIRVE PARA TODOS
LOS TRÁMITES PÚBLICOS Y PRIVADOS



yo, el Notario, doy fé, que después de haber leído, en alta voz, toda esta escritura a los comparecientes, éstos la aprueban y la suscriben, conmigo el Notario, en un solo acto. - *[Signature]*

[Signature]
DEYSI-VALERIA VELIZ CEDEÑO

C.de C. #.120342620-8

C. de V.#. 063-0150

[Signature]
ROBERTO BERNARDO MACIAS GUEVARA

C.de C. #. 090724088-1

C. de V.#. 007-0022

[Signature]
PABLO ALFREDO VELIZ CARCAMO

C.de C. #. 120415457-7

C. de V.#. 002-0029

EL NOTARIO.,

[Signature]
AB. ABEL GERMAN LEÓN LEÓN

Se otorgó ante mí, y en fé de ello, confiero este PRIMER TESTIMONIO, que firmo y sello, en esta Ciudad, Quevedo, en la misma fecha de su celebración. *[Signature]*



[Signature]
Abel German León León
Notario Tercera del Canton Quevedo



REGISTRO MUNICIPAL DE LA PROPIEDAD Y MERCANTIL DEL CANTÓN MOCACHE



Razón de Inscripción

Número de Repertorio: 940

Fecha de Repertorio: 23-jul-2015

EL REGISTRO MUNICIPAL DE LA PROPIEDAD DEL CANTON MOCACHE, certifica que en esta fecha se inscribió(eron) el(los) siguiente(s) acto(s):

1.- Con fecha veintitres de julio de dos mil quince queda inscrito el acto o contrato COMPRAVENTA en el Registro de PROPIEDADES No. 807 celebrado entre: ([VELIZ CEDENO DEYSI VALERIA en calidad de VENDEDOR], [MACIAS GUEVARA ROBERTO BERNARDO en calidad de VENDEDOR], [VELIZ CARCAMO PABLO ALFREDO en calidad de COMPRADOR])

Que se refiere al(los) siguiente(s) bien(es):

Tipo Bien	Cód.Catastral/Ident.Predial	No. Ficha	Actos
TERRENO		2.319	Compraventa

MOCACHE, jueves 23 de julio de 2.015

Impreso a las: 16:44:08


Elaborado por: CINTHYA MONTOYA




17

Abg. Gabriel Gallegos Franco
REGISTRADOR DE LA PROPIEDAD




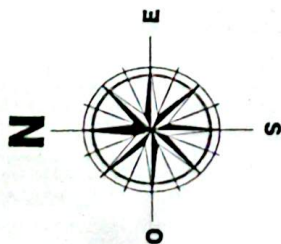

CARTA TOPOGRAFICA : MOCACHE

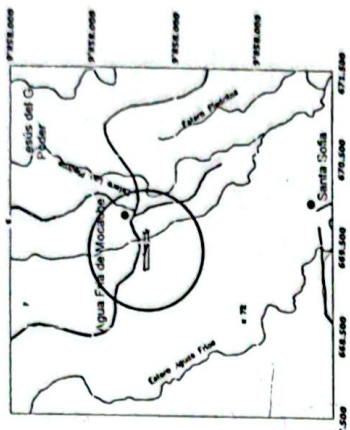

UBICACION GEOGRAFICA
ESCALA 1:75.000

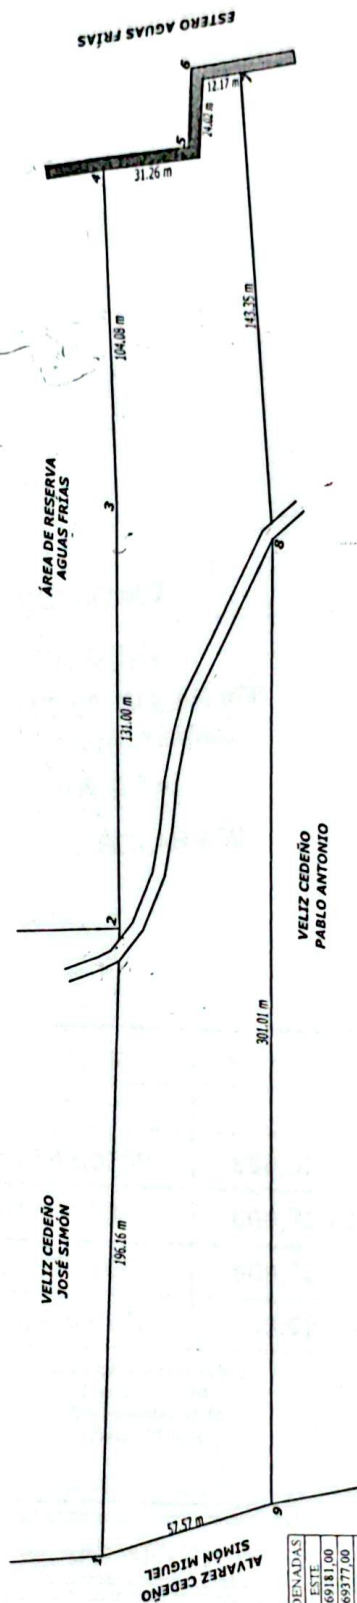

CUADRO DE COORDENADAS		
VER	NORTE	ESTE
1	9856374.00	669181.00
2	9856366.00	669377.00
3	9856366.00	669508.00
4	9856370.00	669612.00
5	9856339.00	669616.00
6	9856338.00	669640.00
7	9856326.00	669642.00
8	9856316.00	669499.00
9	9856319.00	669198.00

DATOS TOMADOS CON GPS.
DATUM WGS 84 PROYECCION
CARTOGRAFICA UTM.
ZONA 17 SUR.

LEVANTAMIENTO PLANIMETRICO

PROPIETARIO:

VELIZ CARGANO PABLO ALFREDO
C.I.B. 70411457.7

ÁREA DEL PREDIO

3.06 Cuadras

21,563.00 Mts 2.

PROYECTA LOS RIOS

CANTÓN: MOCACHE

ESCALA: 1:2000

FECHA:


28 DE SEPTIEMBRE DEL 2015.

ING. CARLOS YANEZ ZAMBRANO
Reg. INECOT 104-11-03240



LINDEROS

NORTE:	VELIZ CEDENO JOSE SIMON - ÁREA DE RESERVA AGUAS FRIAS
SUR:	VELIZ CEDENO PABLO ANTONIO
ESTE:	ESTERO AGUAS FRIAS
OESTE:	ALVAREZ CEDENO SIMON MIGUEL

UBICACIÓN GEOGRÁFICA

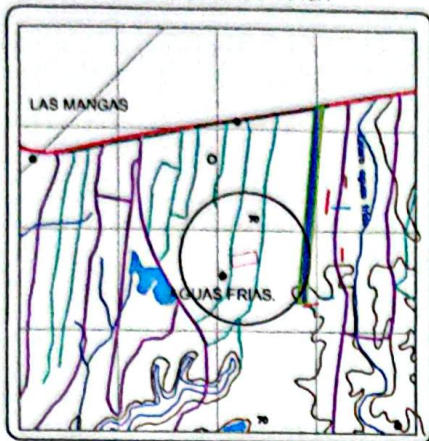

INSTITUTO GEOGRÁFICO MILITAR
CARTA TOPOGRÁFICA DEL CANTÓN MOCACHE
CT - NIV - A4 - 3090 - II
ESCALA: 1 - 50.000

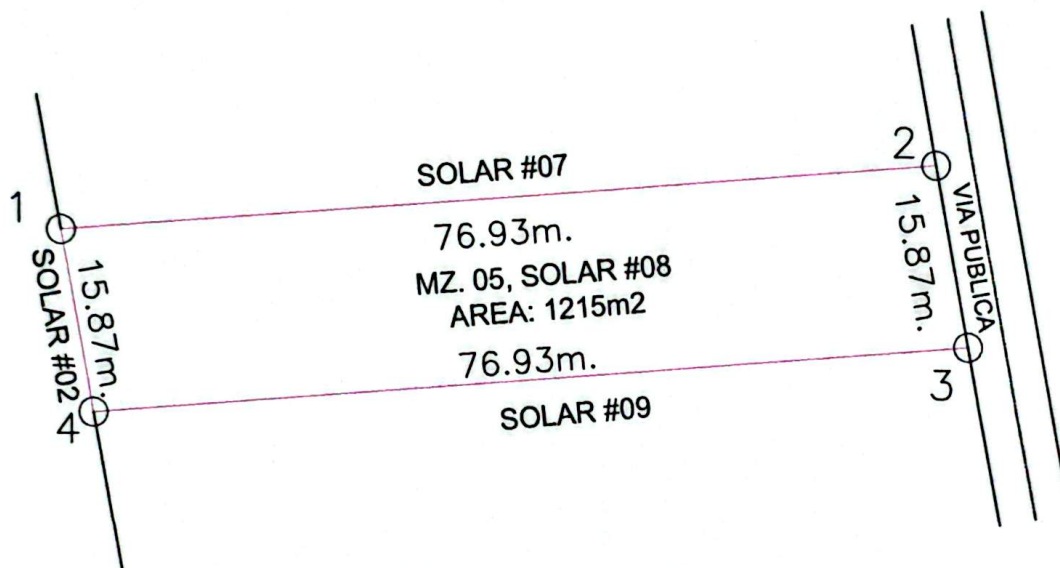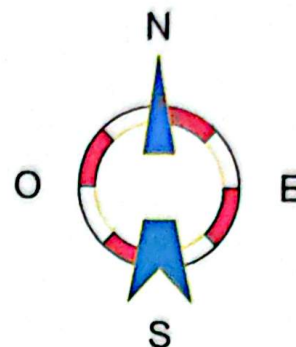

V	C O O R D E N A D A S	
	Y	X
1	9,856,542.5159	669,623.6905
2	9,856,548.7313	669,700.3668
3	9,856,533.1067	669,703.1705
4	9,856,526.8912	669,626.4919

Datos tomados con G.P.S
Datum: WGS 84
Coordenadas: UTM
Zona : 17 SUR

LEVANTAMIENTO PLANIMETRICO

ÁREA: 1215m2.

PROVINCIA: LOS RÍOS

CANTON: MOCACHE

PARROQUIA: MOCACHE

SECTOR: AGUAS FRIAS

PREDIO: S/N

FECHA: Oct -20-2025

PROPIETARIO:

VELIZ CARCAMO ALFREDO

RESP. TÉCNICA:

ING. PAUL CANSING YEPEZ
REGISTRO SENESCYT: 1014-07-772448