

UBICACION
Prov. Guayas
Cantón El Empalme
Parroquia Velasco Ibarra
Porvenir De Adentro



MARGEN DE PROTECCION DE
ESTERO
ancho: 15.00 m. desde el centro
(0.0758 ha.)

FRACCIONAMIENTO.

MELCHORA RUIZ ARANA

FECHA: Mayo del 2019
ESCALA: 1: 2000
Lav. y calculó

Melchora Ruiz Arana
Reg. Prof. 19192

NOTARIA PRIMERA
Mariane Velaz Macias
ABOGADA
AREA CAMINO PUBLICO
0,0266 ha.


FLORA RUIZ

AREA UTIL
(2,0139 has.)


CUADRO DE AREAS	
AREA UTIL	2,0139
AREA 2	1,0252
MARGEN DE PROTECCION	0,0758
AREA CAMINO PUBLICO	0,0266
AREA TOTAL (has.)	2,1163

LINDEROS Y MEDIDAS

NORTE	FLORA RUIZ en 185.38 m. R.S 61°41'45.2" E; ANCHO DE CARRETERO en 6.51 m;
	FLORA RUIZ en 47.20 m. R.S 60°5'22.0" E; 54.18 m. R.S 53°53'16.3" E; 164.10 m. R.S 52°24'33.0" E.
SUR	NILO RUIZ RIVAS en 257.60 m. R.N 57°20'3.9" W; ANCHO DE CARRETERO en 6.33 m; NILO RUIZ RIVAS en 78.39 m. R.N 61°22'29.2" W; 38.83 m. R.S 55°29'29.3" W; 121.94 m. R.N 59°25'39.5" W.
	ESTERO LA REPRESA en 62,25m. SIGUIENDO SU CAUCE
OESTE	SEGUNDO RUIZ en 105.35 m. R.N 86°12'58.6" E; 41.88 m. R.N 42°12'3.7" W.

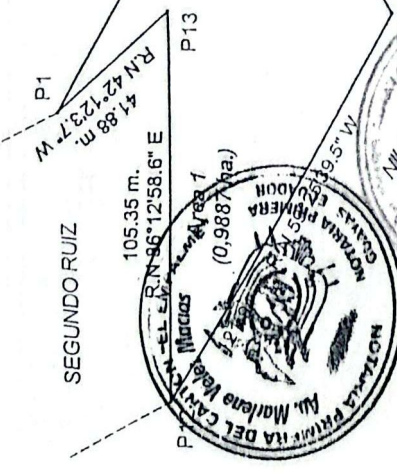


CUADRO DE COORDENADAS	
ESTE	P10
547321.00	9879256.00
547484.21	9879168.10
547489.95	9879165.02
547530.86	9879141.48
547574.63	9879109.55
547704.66	9879009.44
547672.00	9878998.00
547455.14	9879137.04
547449.81	9879140.45
547381.00	9879178.00
547349.00	9879156.00
547244.01	9879218.02
547349.13	9879224.98
Datos obtenidos con GPS, Datum: WGS - 84 Proyección Cartográfica UTM, Zona 17 Sur	

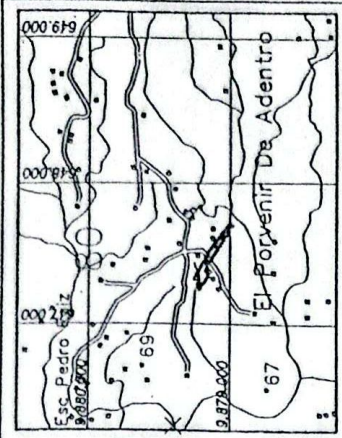

UBICACION
 Prov. Guayas
 Cantón El Empalme
 Parroquia Velasco Ibarra
 Porvenir De Adentro



FRACCIONAMIENTO.
MELCHORA RUIZ ARANA
 FECHA: Mayo del 2019
 ESCALA: 1:1250
 Lev. y cálculo

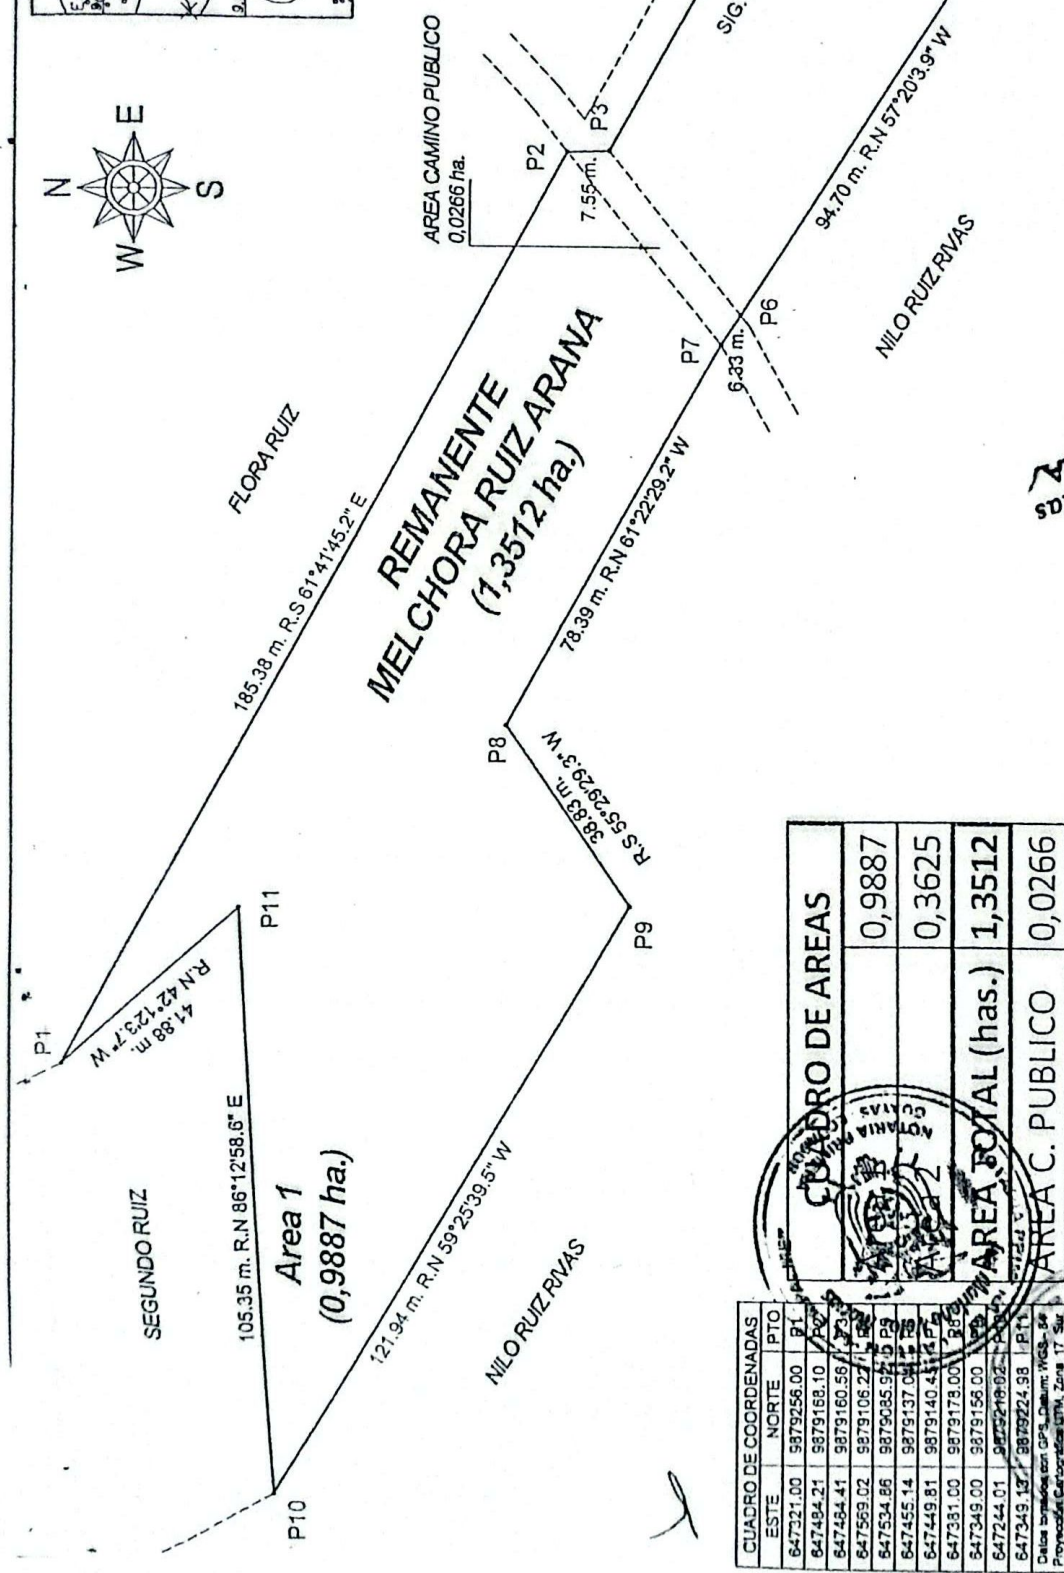

CUADRO DE COORDENADAS			
ESTE	NORTE	PTO	
647321.00	9879256.00	P1	
647494.21	9879168.10	P2	
647484.41	9879160.58	P3	
647559.02	9879106.27	P4	
647534.86	9879035.92	P5	
647455.14	9879137.04	P6	
647449.81	9879140.41	P7	
647381.00	9879178.00	P8	
647349.00	9879156.00	P9	
647244.01	9879219.02	P10	
647349.13	9879224.98	P11	

CUADRO DE AREAS	
Area 1	0,9887
Area 2	0,3625
AREA TOTAL (has.)	1,3512
AREA C. PUBLICO	0,0266

LINDEROS Y MEDIDAS	
NORTE	FLORA RUIZ en 185.38 m. R.S 61°41'45.2" E; ANCHO DE CARRETERO en 7.55 m; CARRETERO PUBLICO en 100.80 m. SIGUIENDO SU TRAZADO
SUR	NILO RUIZ RIVAS en 94.70 m. R.N 57°20'3.9" W; ANCHO DE CARRETERO en 6.33 m; NILO RUIZ RIVAS en 78.39 m. R.N 61°22'29.2" W; 38.83 m. R.S 55°29'29.3" W; 121.94 m. R.N 59°25'39.5" W.
ESTE	LOTE 1 en 39.73 m. R.S 59°17'4.4" W.
OESTE	SEGUNDO RUIZ en 105.35 m. R.N 86°12'58.6" E; 41.88 m. R.N 42°12'3.7" W.

AB. Mariana Pérez Macías
 NO TRABAJO PRIMERA

Ing. Guido Cansiang V.
 RES-201-092552
 10/05/2019